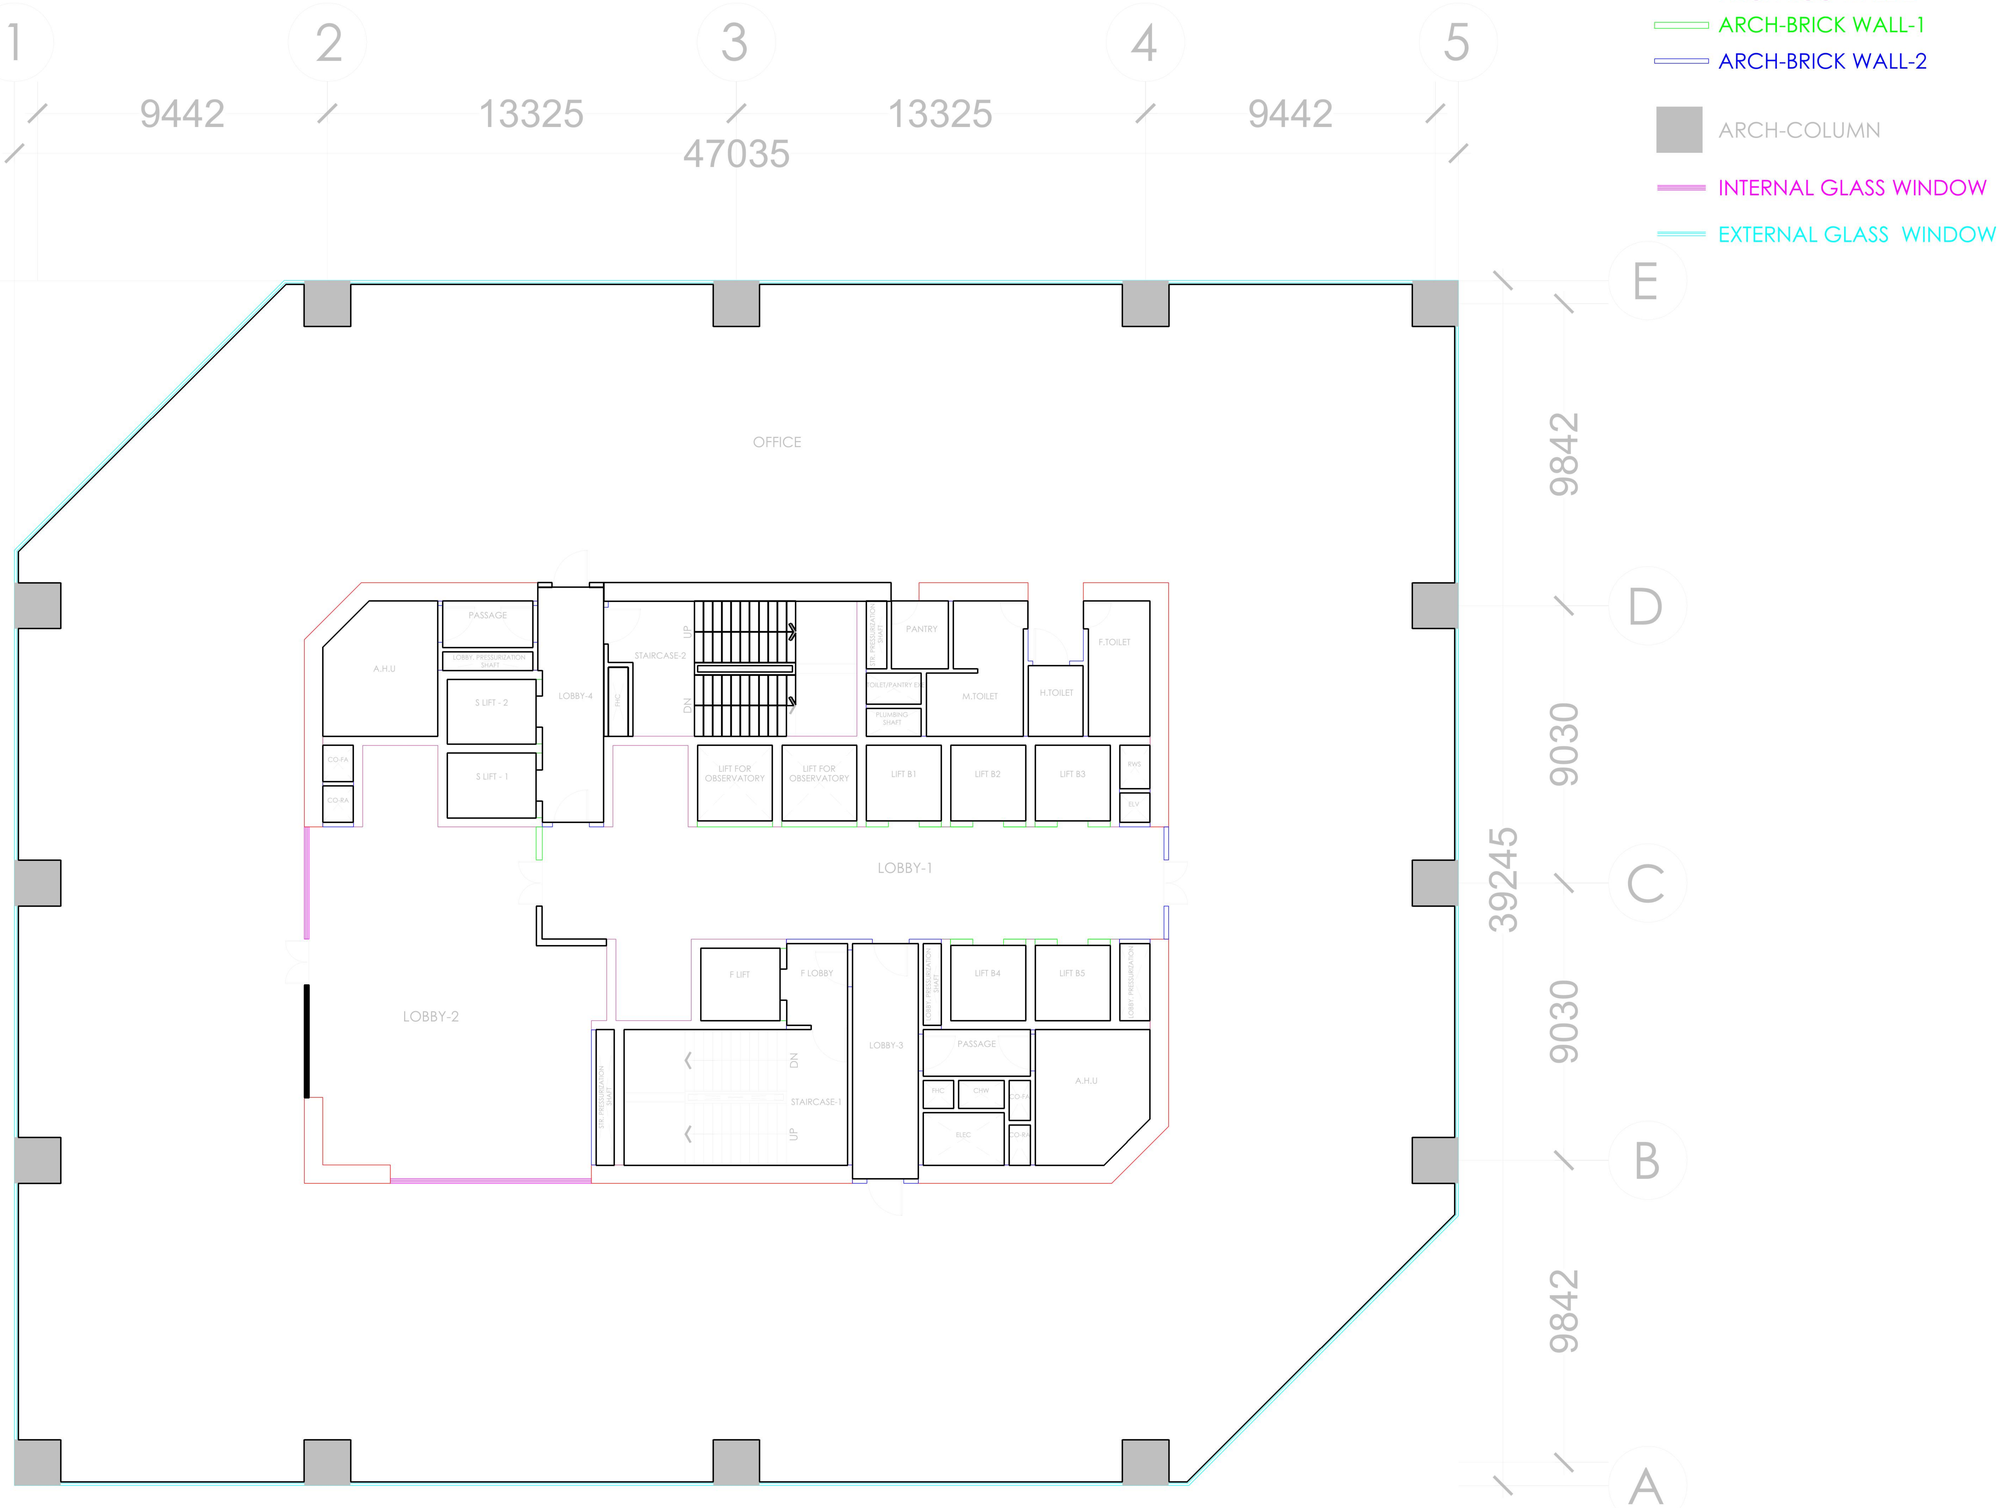

ARCH-RCC WALL-1

ARCH-RCC WALL-2

ARCH-BRICK WALL-1

ARCH-BRICK WALL-2

ARCH-COLUMN

INTERNAL GLASS WINDOW

EXTERNAL GLASS WINDOW

GENERAL NOTES :-

THIS DRAWING IS THE COPYRIGHT OF Architect Hafeez Contractor
29, Bank Street, Mumbai 400 023
Tel. 91-2661920.

IT IS NOT ALLOWED TO COPY OR REPRODUCE ITS CONTENTS IN ANY FORM EXCEPT FOR THE PURPOSE WHICH IT IS INTENDED WITHOUT THE ABOVE CONSULTANT'S AUTHORITY.

DO NOT SCALE THIS DRAWING, ONLY STATED DIMENSIONS ARE TO BE CONSIDERED.

CONTRACTOR TO VERIFY THE DETAIL / INFORMATION GIVEN IN THIS DRAWING, ANY DISCREPANCIES SHALL BE BROUGHT TO ENGINEERS ATTENTION PRIOR TO COMMENCEMENT OF WORK, FAILURE TO COMPLY WITH THE ABOVE WILL BE CONTRACTORS LIABILITY.

KEY PLAN

NOTE :-

Rev.	Date	Description.

PURPOSE OF ISSUE

PROJECT NAME

CONSTRUCTION OF JNPA OFFICE COMPLEX AT MALLET BUNDER, MUMBAI

CLIENT

JAWAHARLAL NEHRU PORT AUTHORITY

PROJECT MANAGEMENT CONSULTANT

इंजीनियर्स इंडिया लिमिटेड ENGINEERS INDIA LIMITED
R&D COMPLEX, NATIONAL HIGHWAY 8 CHANDER NAGAR, SECTOR 16, GURUGRAM, HARYANA 122001

ARCHITECTURAL CONSULTANT

PLANOSCAPES
ARCHITECTS&PLANNERSPVT.LTD.
811, 8th Floor, The Gateway Commercial Building at Atmosphere, Goregaon Mulund Link Road,Near Runwal Greens, Mulund West, Mumbai - 400080.
sarvesh@planoscapes.com

STRUCTURAL CONSULTANT

MAHIMTURA CONSULTANTS PVT. LTD
ADDRESS - 3RD FLOOR, UNIQUE HOUSE, 25, SYED ABDULLAH BRELVI MARG, KALA GHODA FORT, MUMBAI - 400001
EMAIL - BELAPUR@MAHIMTURA.NET, DHRUVA22MAHIMTURA@GMAIL.COM

SERVICES CONSULTANT

TECHFOUR ENGINEERING SOLUTIONS PVT. LTD -MEPF
ADDRESS - A-16, 1ST FLOOR, MOHAN COOPERATIVE, INDUSTRIAL ESTATES, NEW DELHI - 110044
EMAIL - PUNEET@TECHFOURSOLUTIONS.COM, BPSAMRAT@TECHFOURSOLUTIONS.COM

LANDSCAPE CONSULTANT

INTEGRAL DESIGNS INTERNATIONAL STUDIO PVT LTD - LANDSCAPE
ADDRESS - E-90, ANAND NIKETAN, NEW DELHI - 110021
EMAIL - DESIGNS@INTEGRAL@GMAIL.COM, ACCOUNTS@INTEGRALDESIGNS.IN

DRAWING TITLE

36th FLOOR - DG SHIPPING ARCH LAYOUT

DATE	SHT. SIZE	SCALE
11.02.2026	A1	1:100

DRAWN	APPROVED
Vijay Patil	Sarvesh Nandgirikar

NORTH | DOCUMENT NUMBER: JNPA-EIL-CDG-ARCH-0041 | REVISION: R0

CO-RA | vector_polygon_exact |

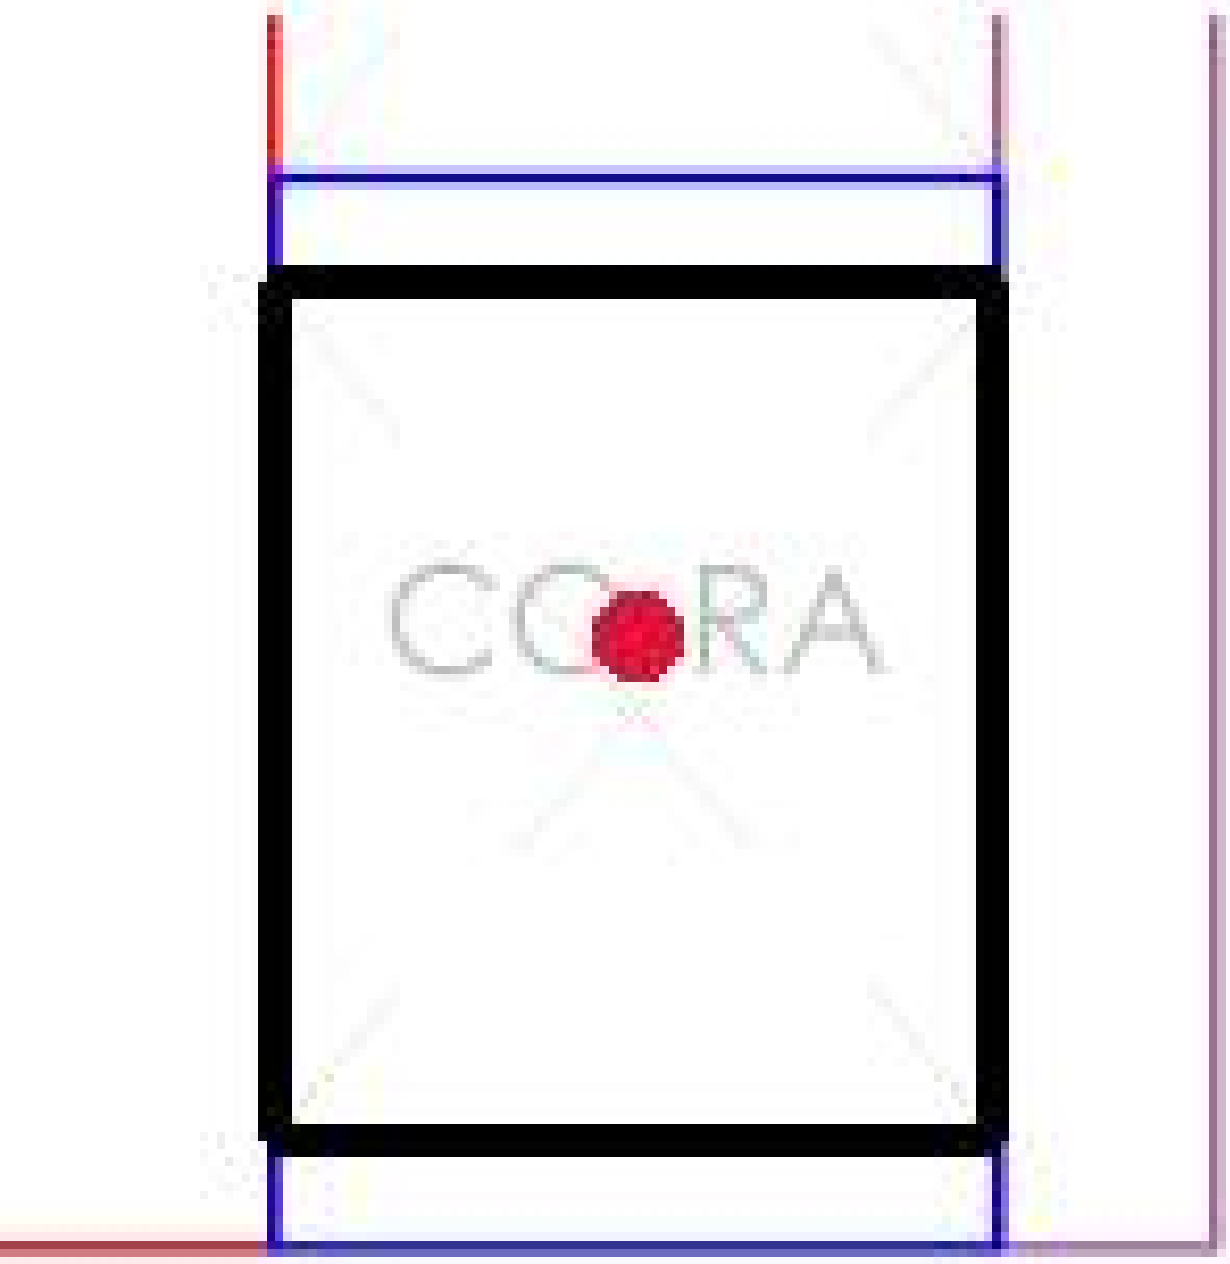

CO-FA | vector_polygon_exact |

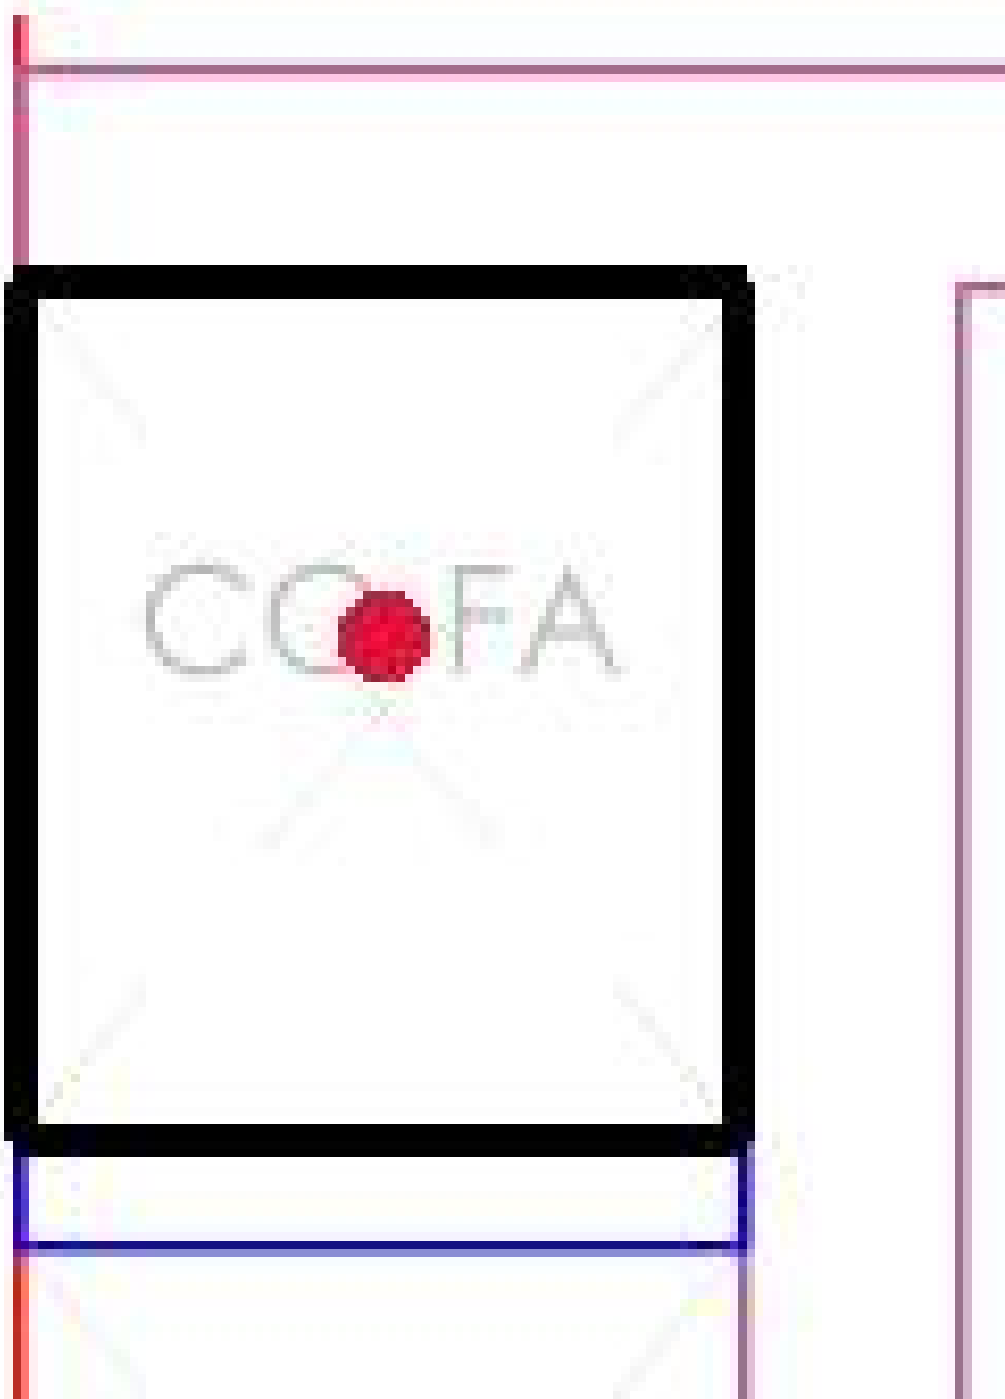

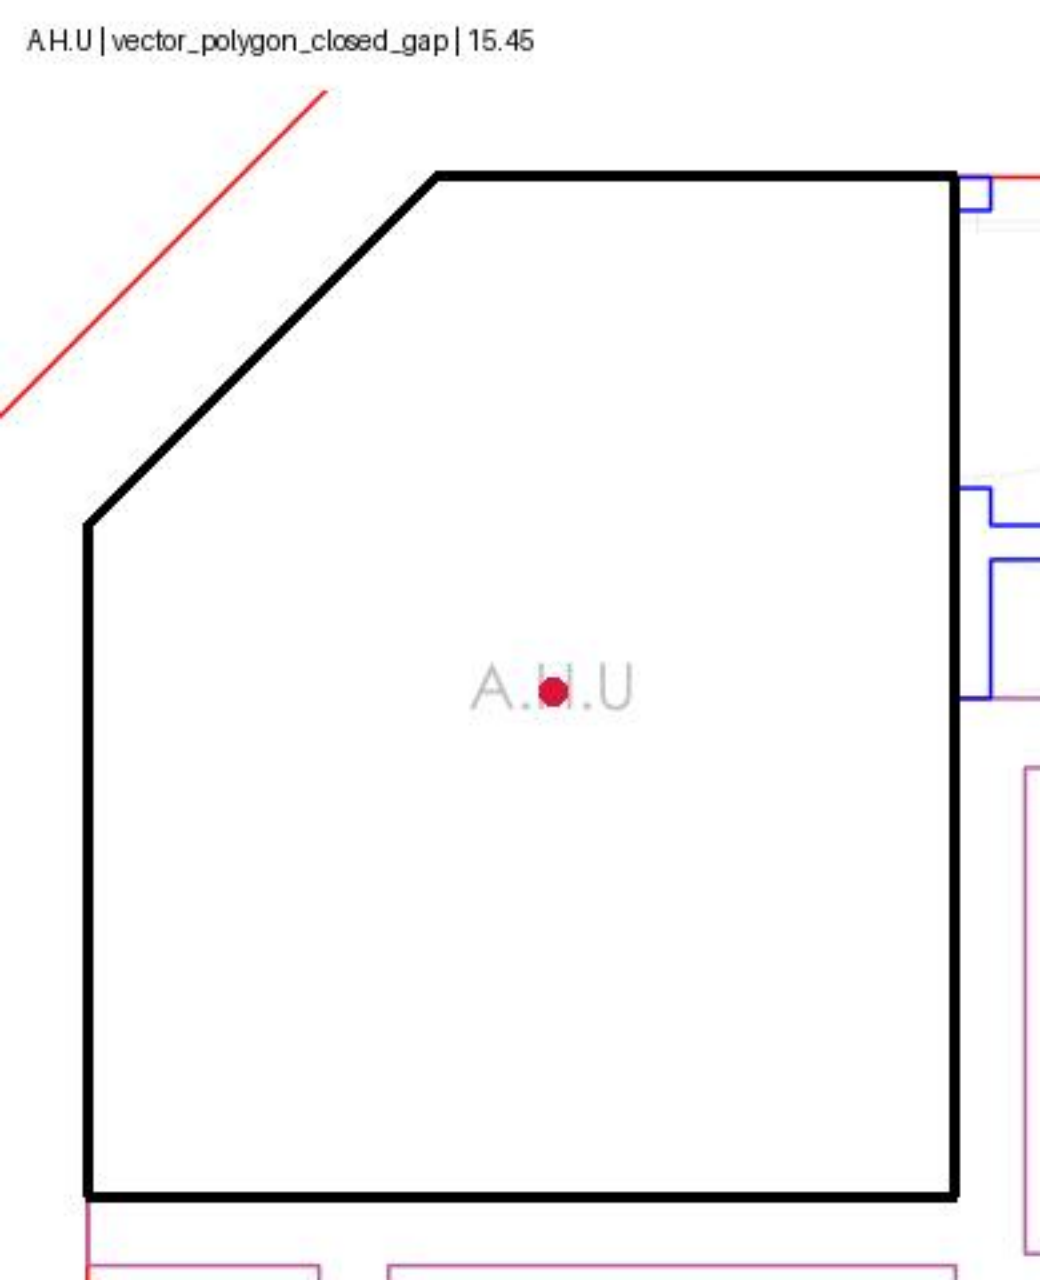
A.H.U | vector_polygon_closed_gap | 15.45
A.H.U

LOBBY-2
PRESSURIZATION
SHAFT

LOBBY. PRESSURIZATION SHAFT | vector_polygon_exact | 1.78

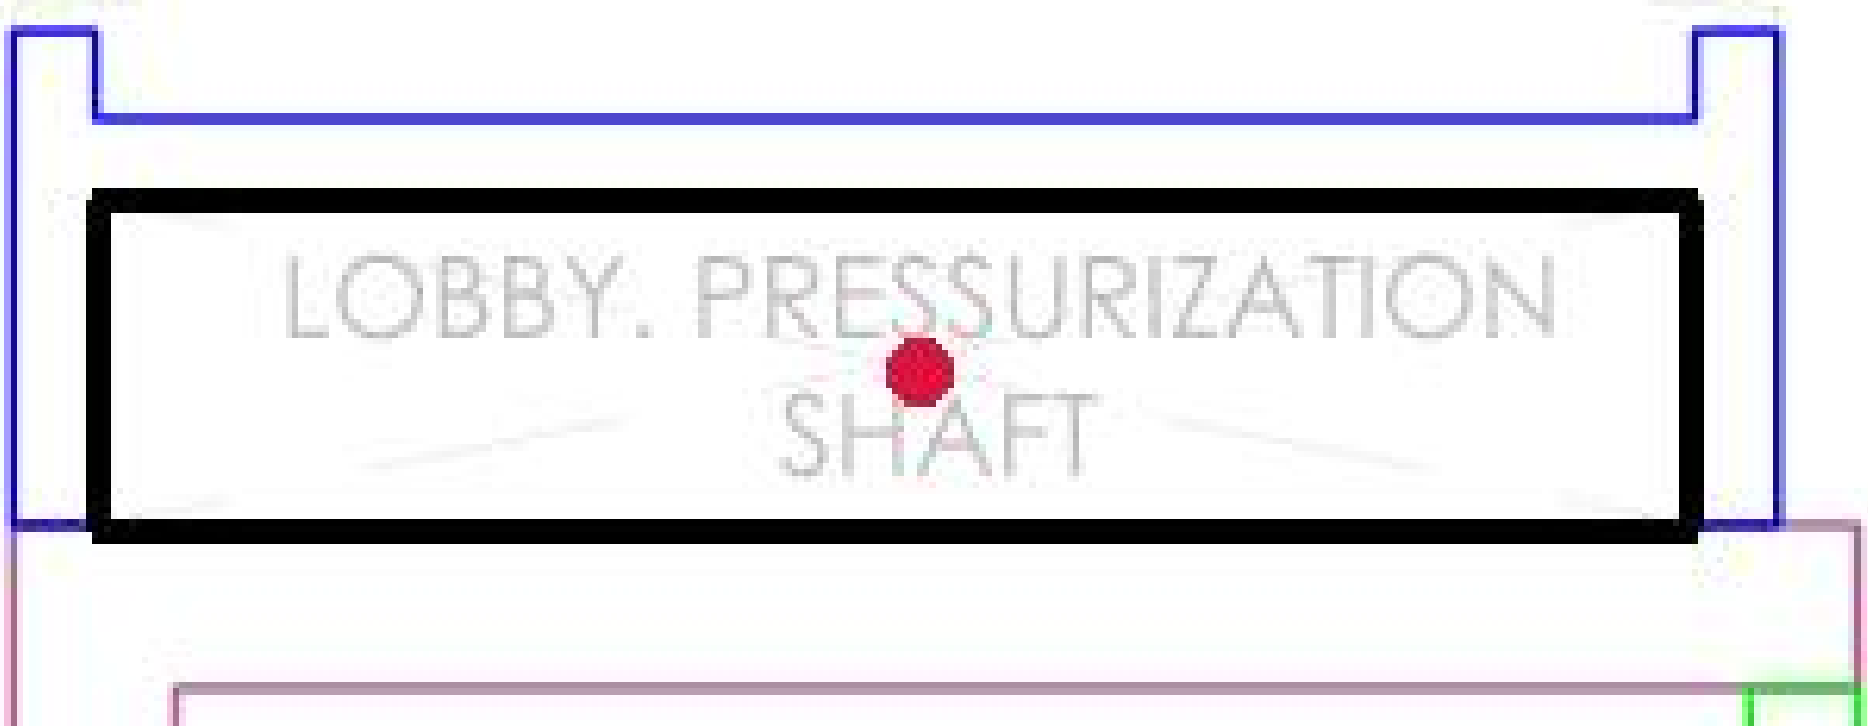

PASSAGE | vector_polygon_closed_gap | 4.45

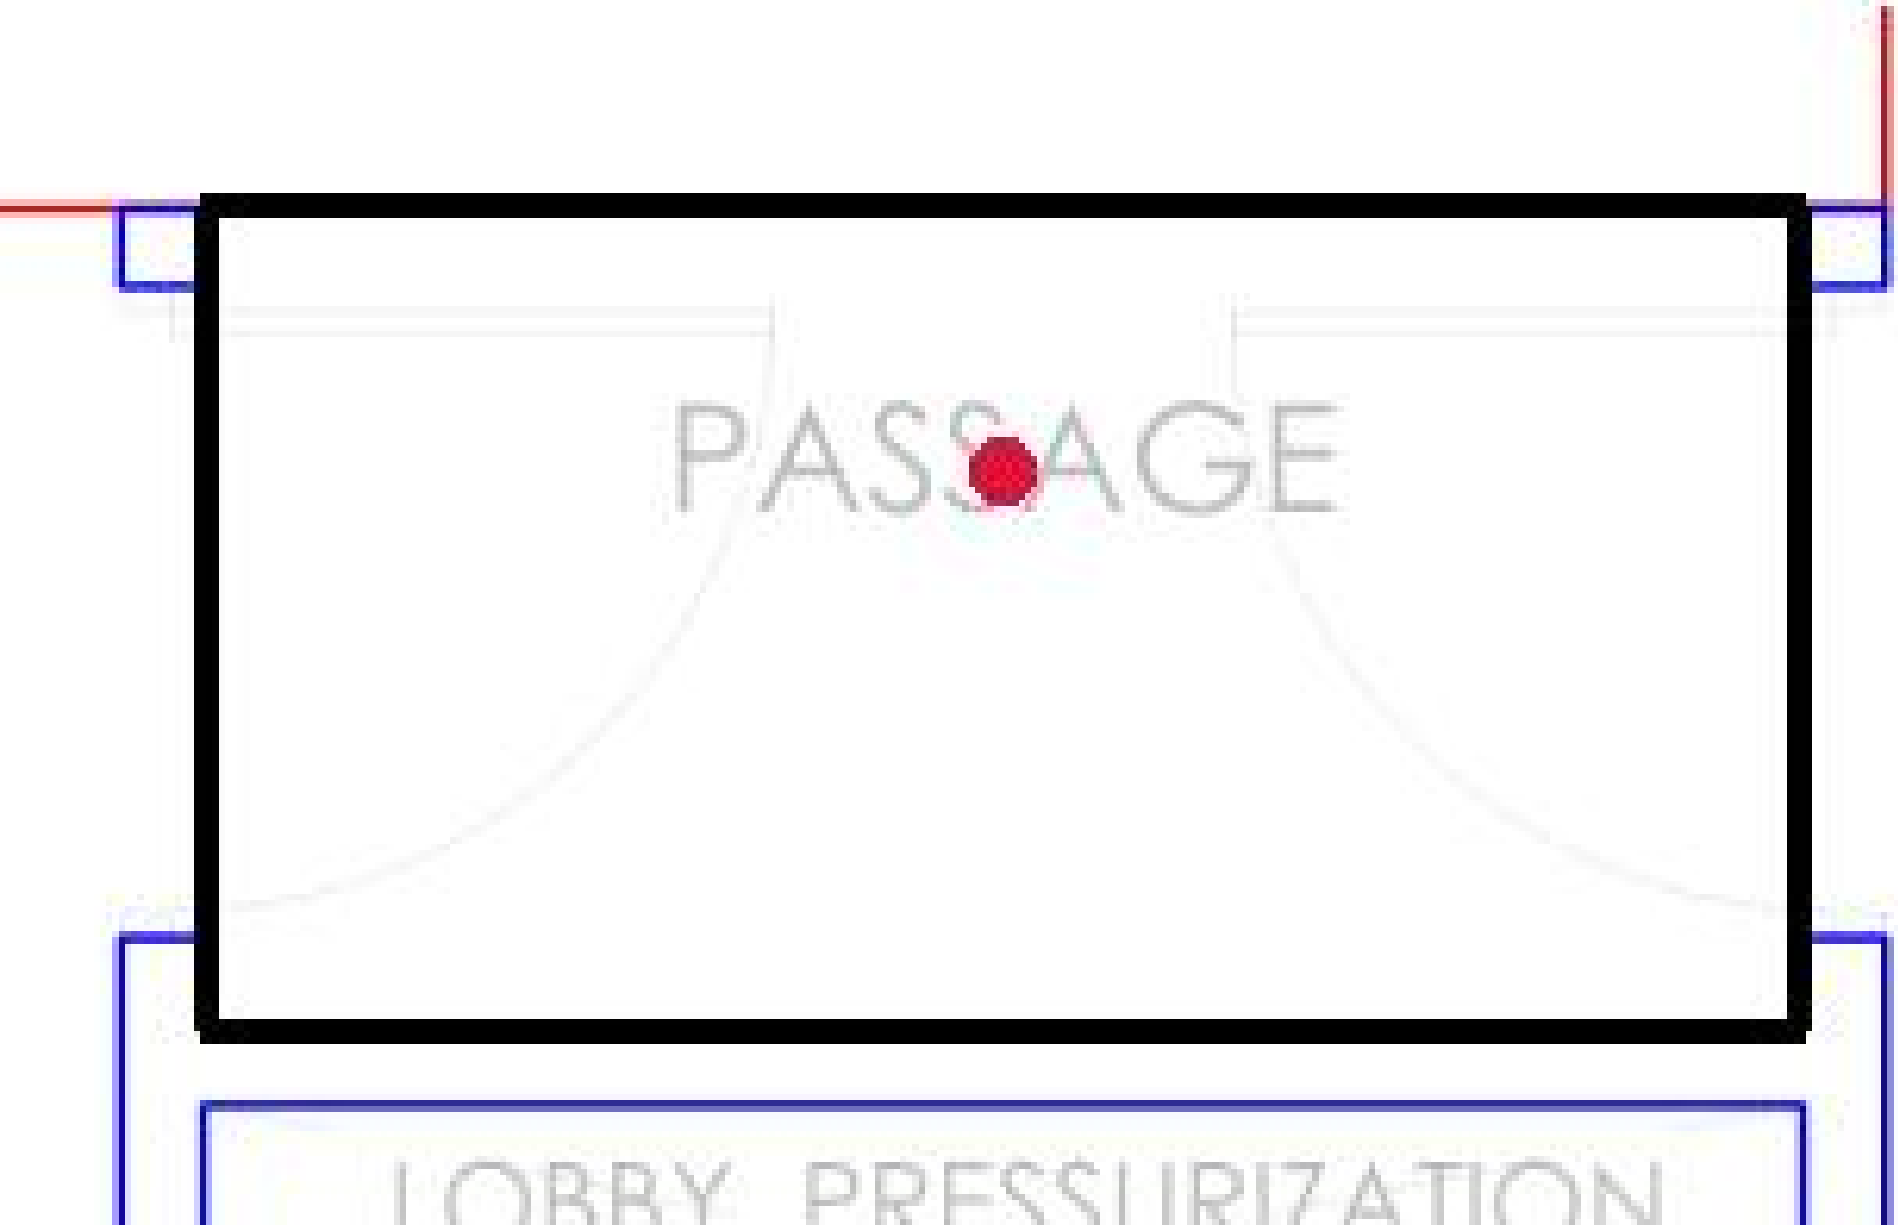

S LIFT - 2 | vector_polygon_exact | 6.12

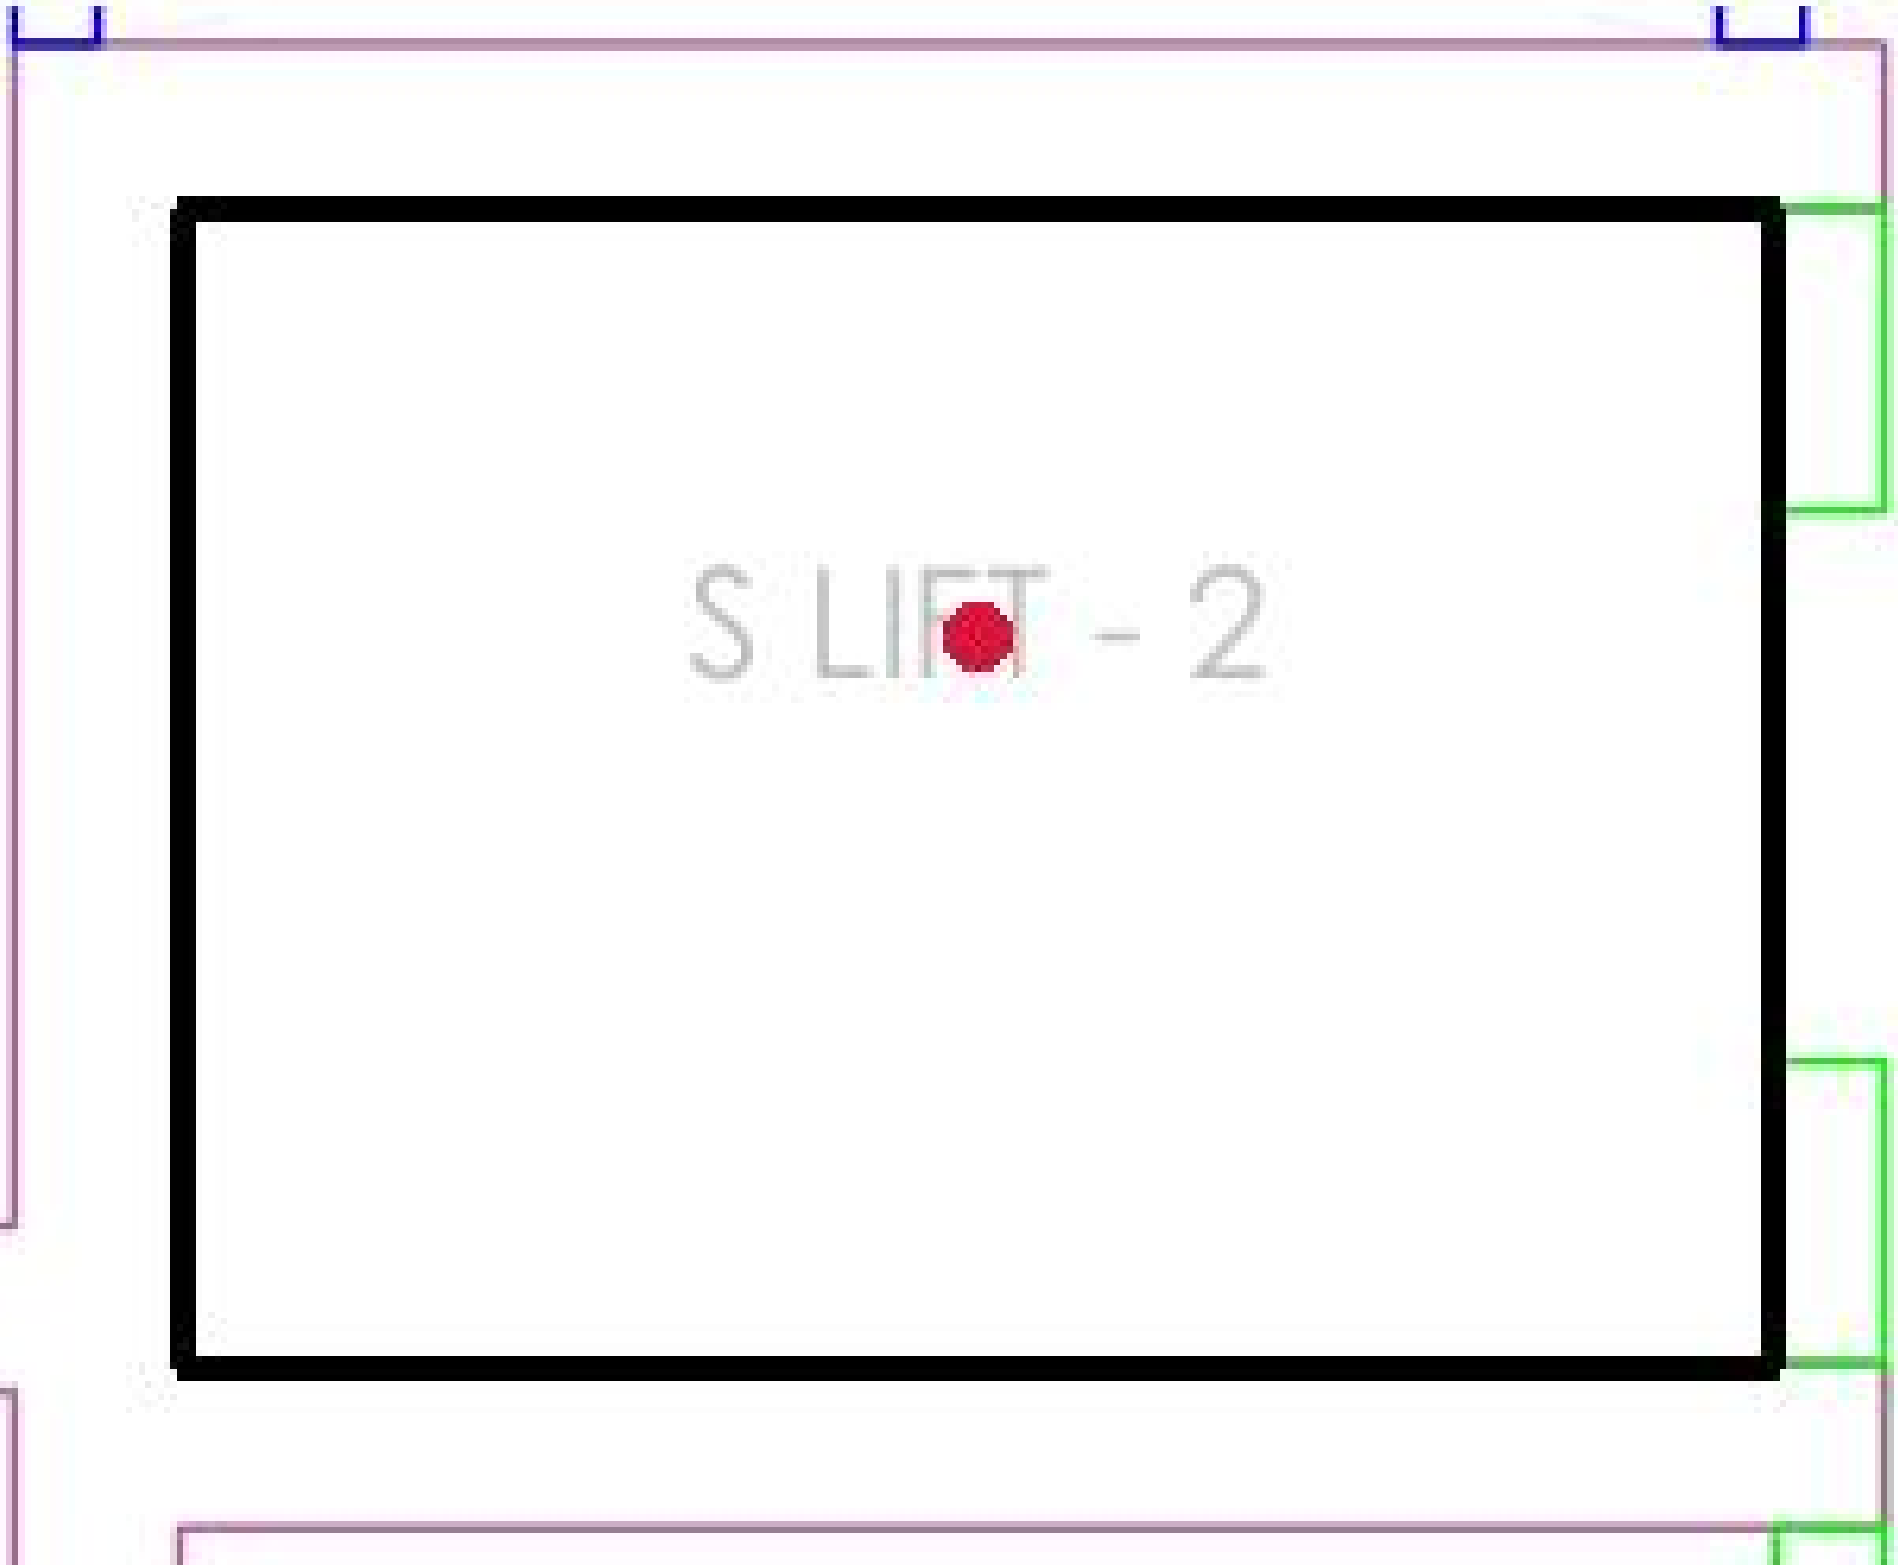

S LIFT - 1 | vector_polygon_exact | 6.13

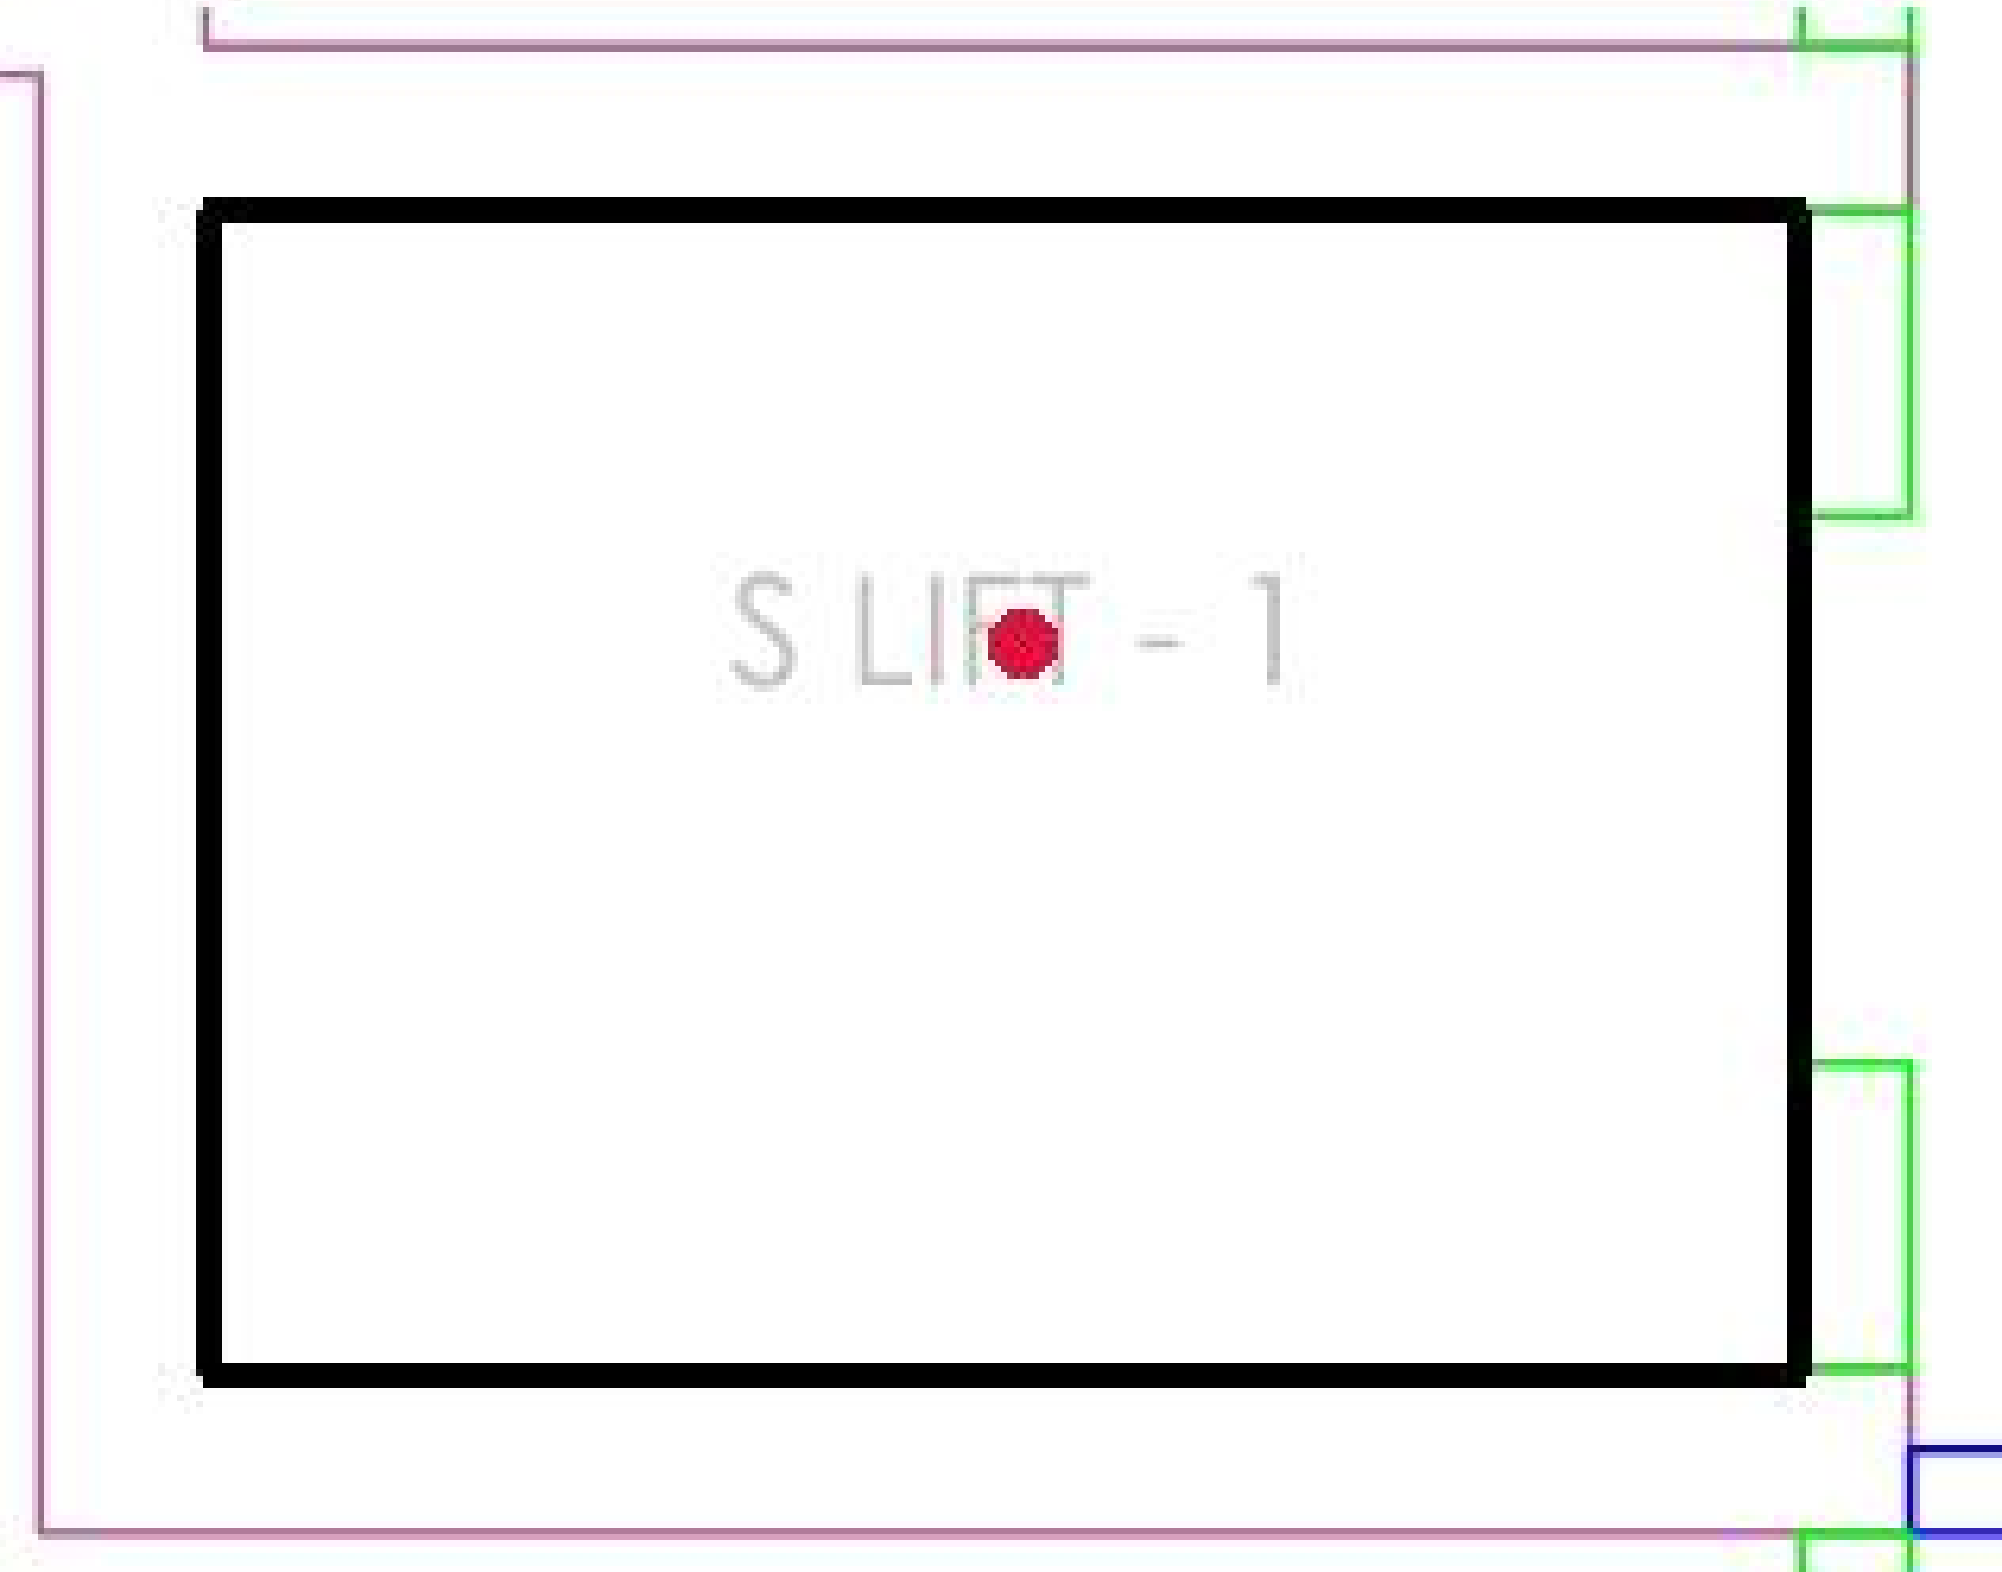

LOBBY-4 | vector_polygon_subtracted_shared_parent

STR PRESSURIZATION

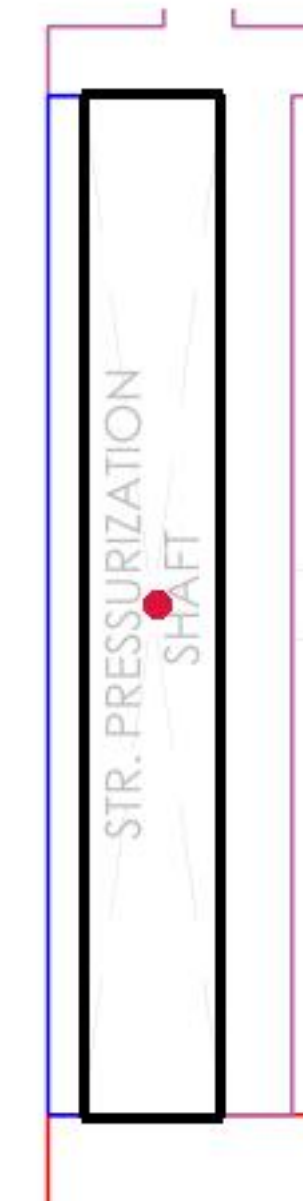

FHC | vector_polygon_e

STAIRCASE-2 | vector_fragment_cluster | 20.93

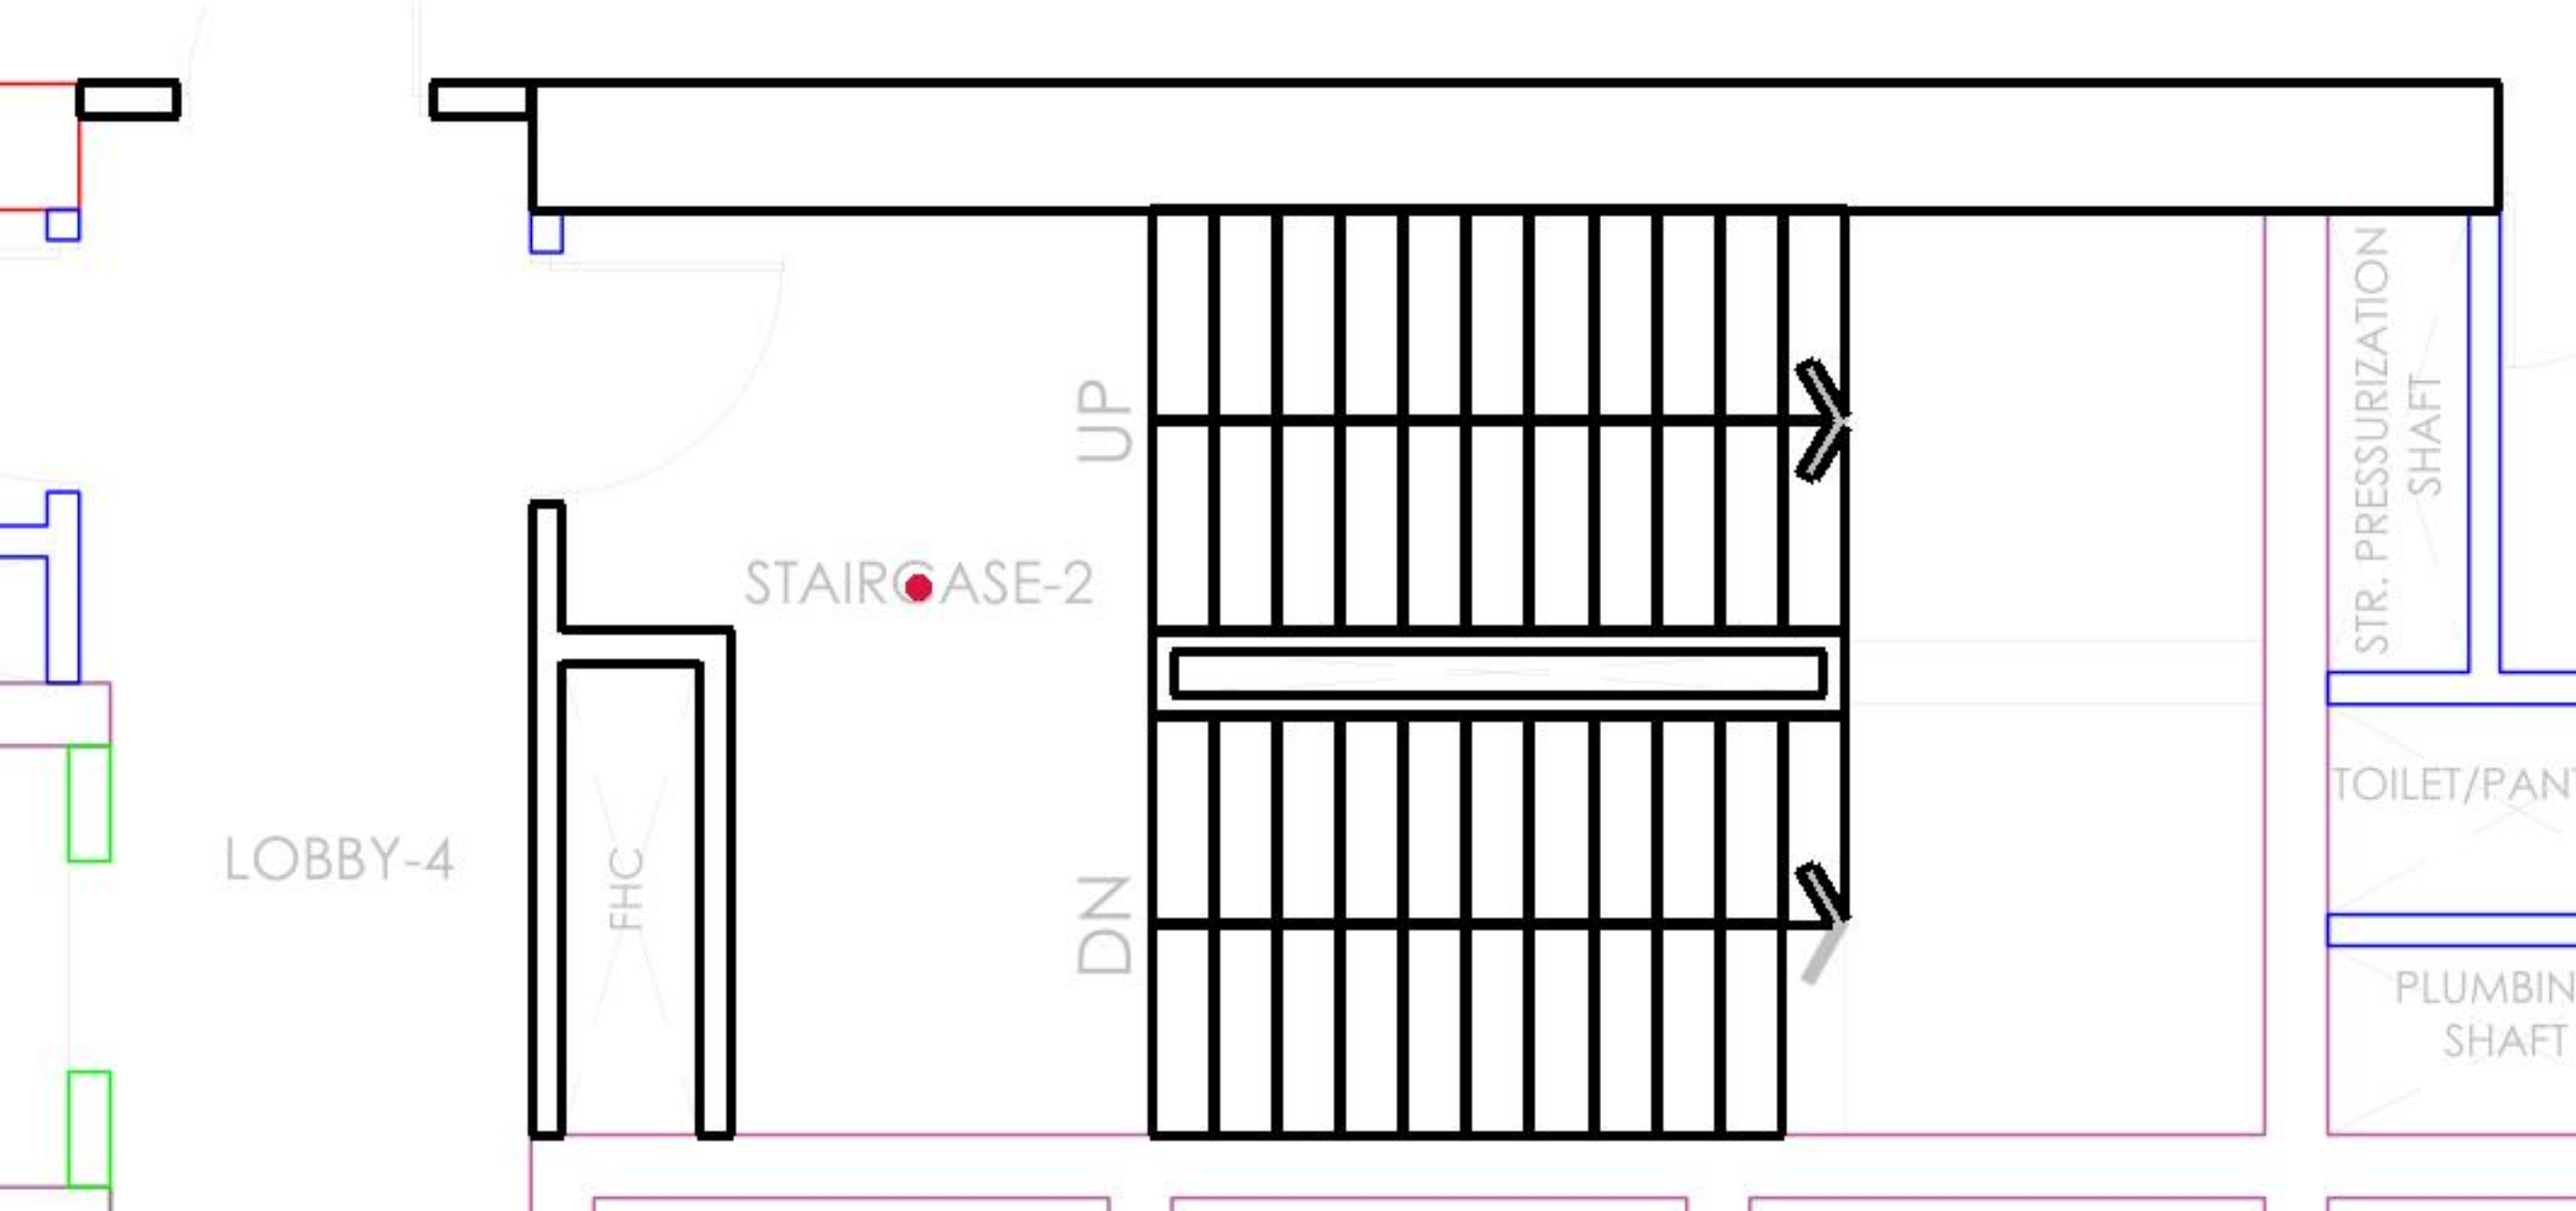

LIFT FOR OBSERVATORY | vector_polygon_exact | 6.03

F LIFT | vector_polygon_exact | 6.14

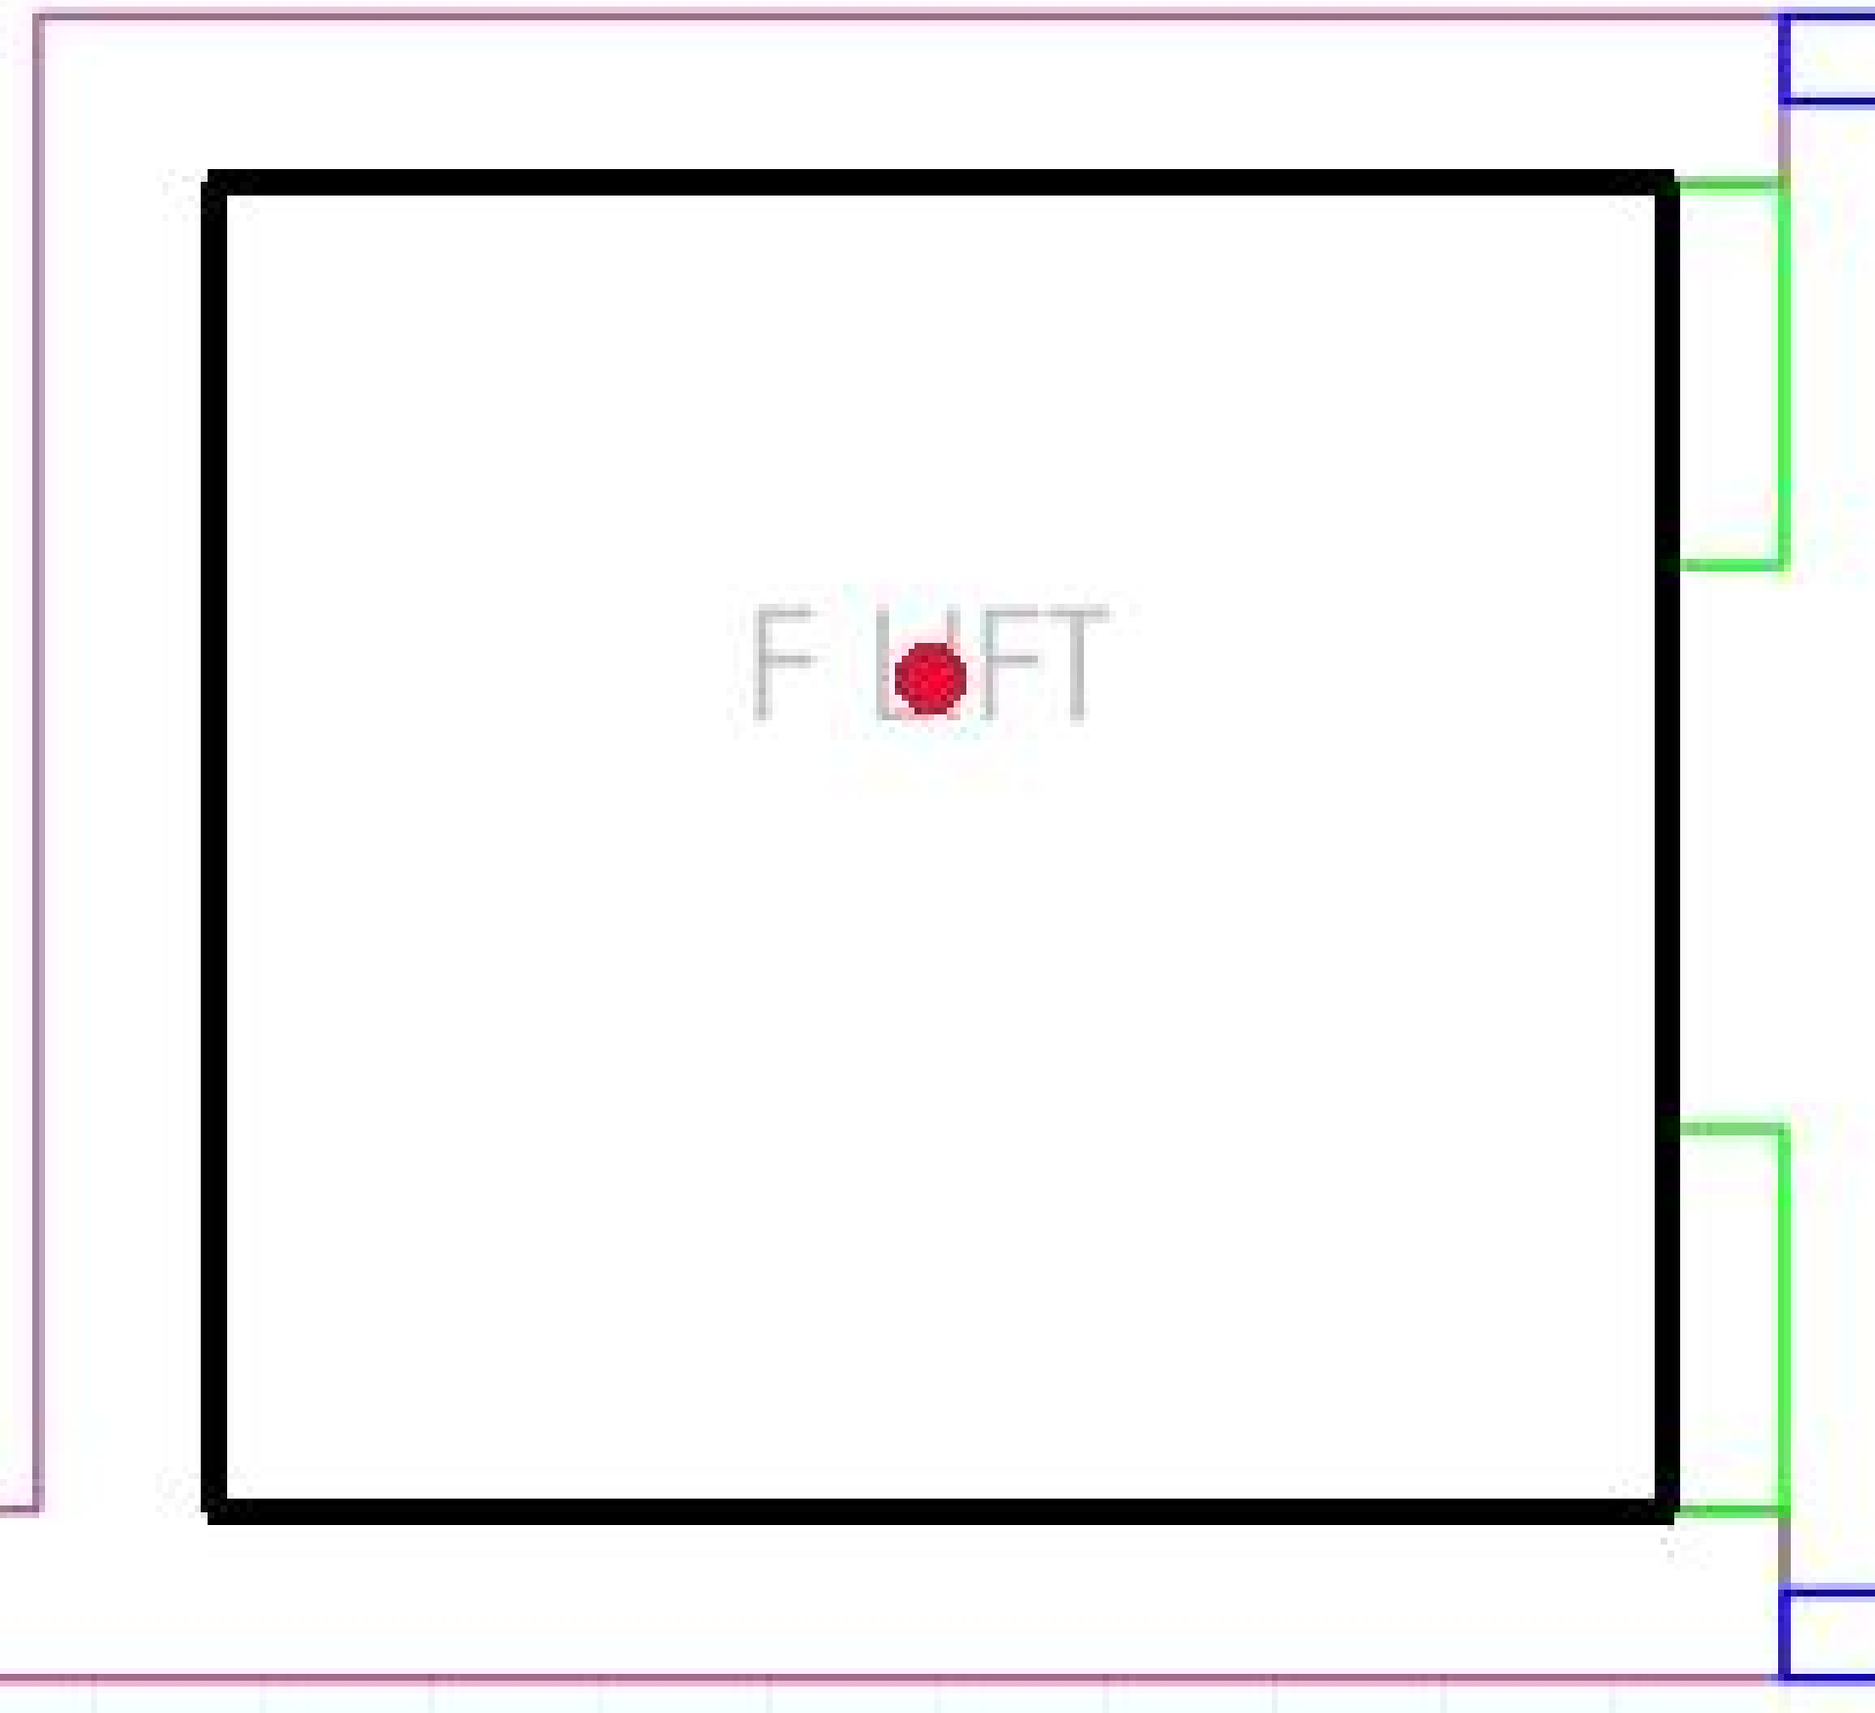

OFFICE | vector_open_residual_partition | 1175.25

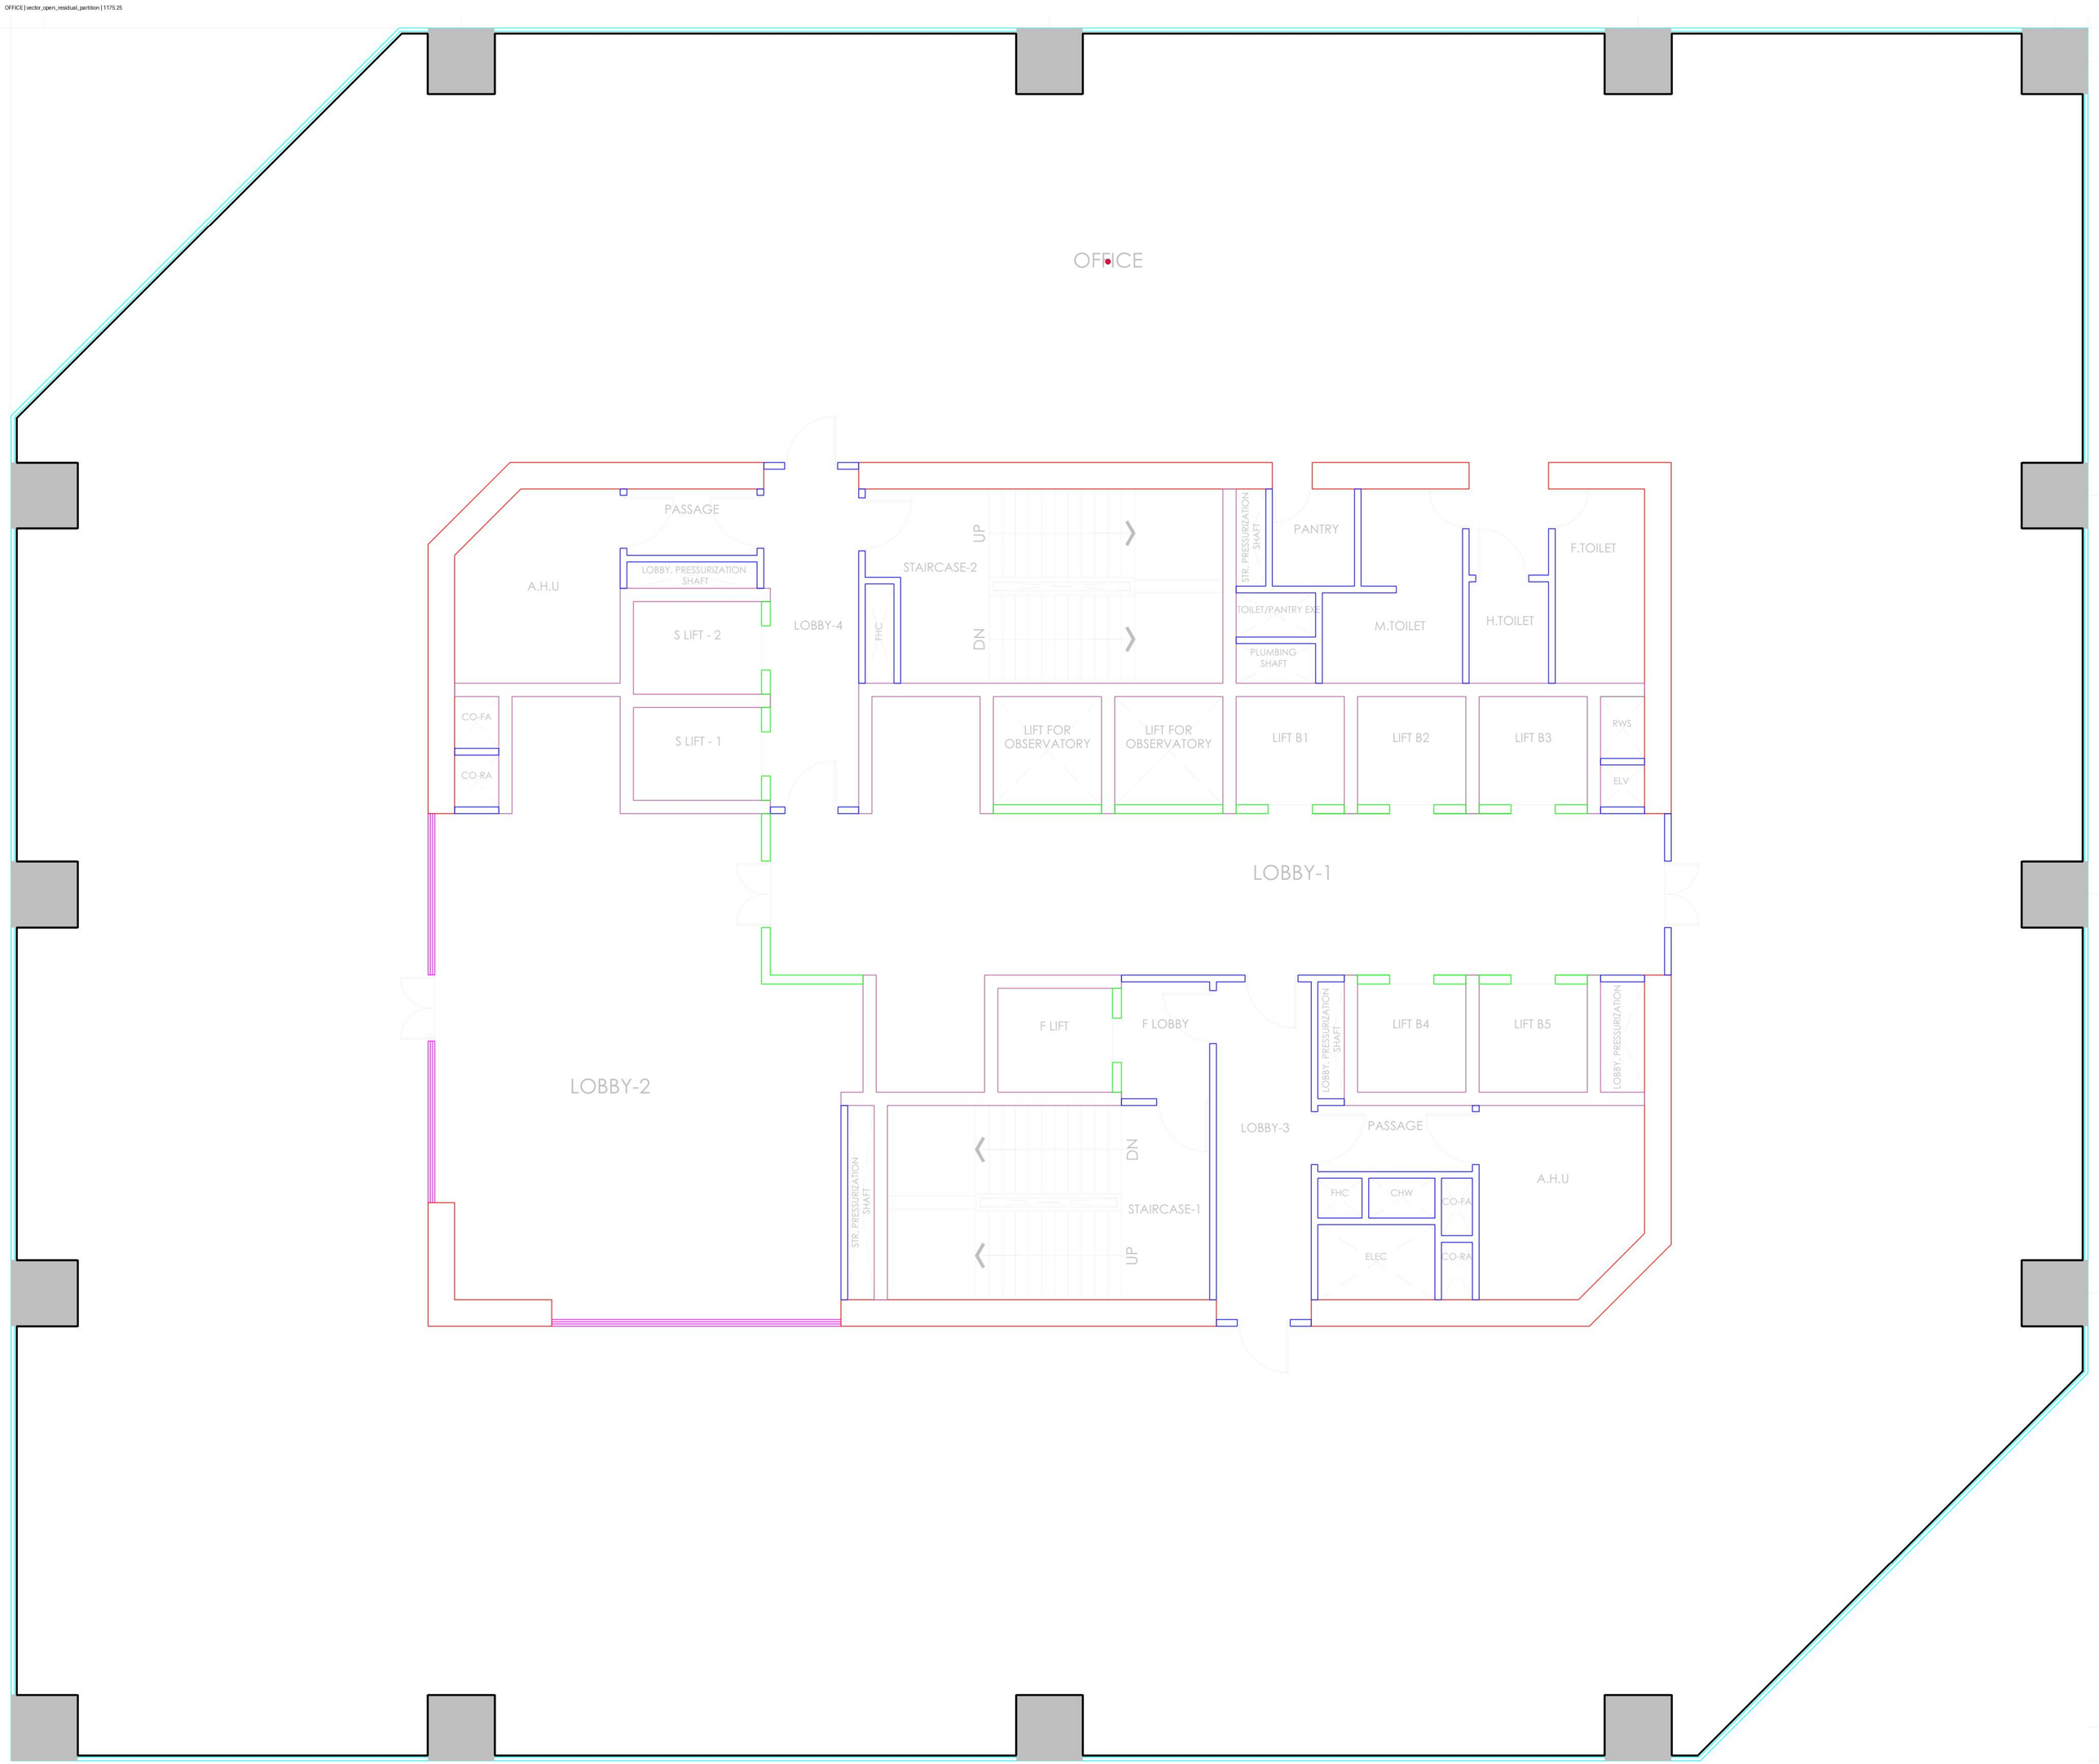

LIFT FOR OBSERVATORY | vector_polygon_exact | 6.03

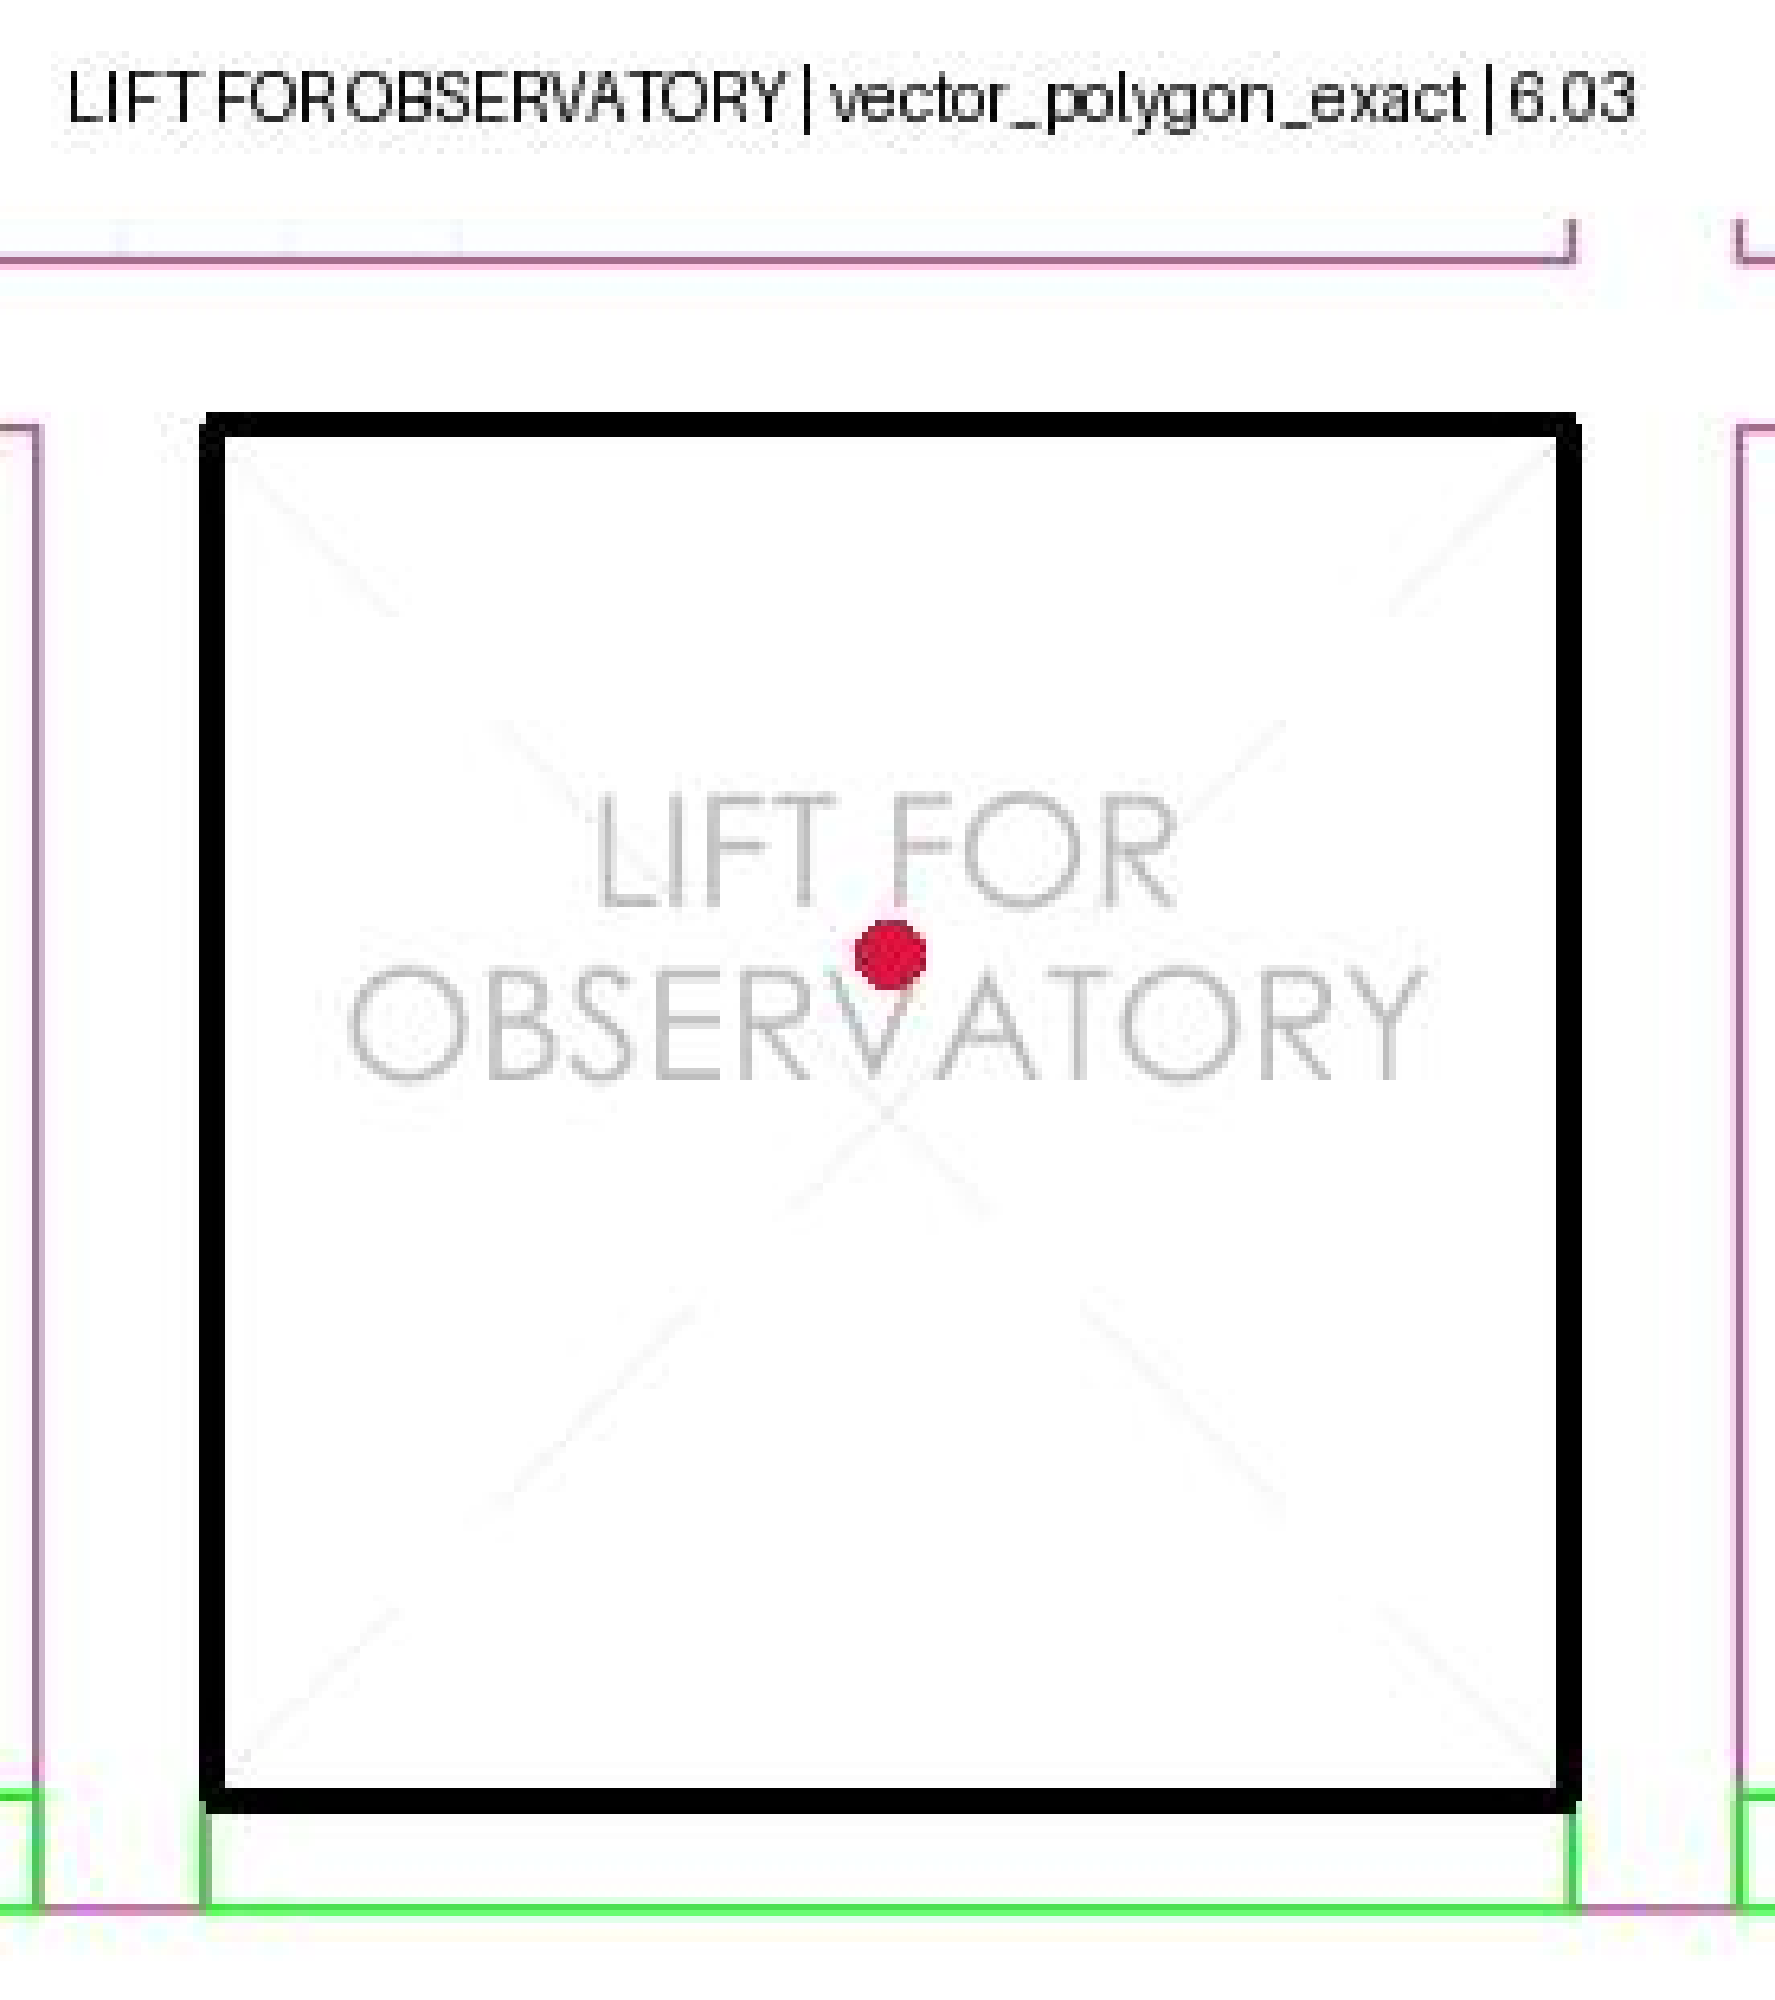

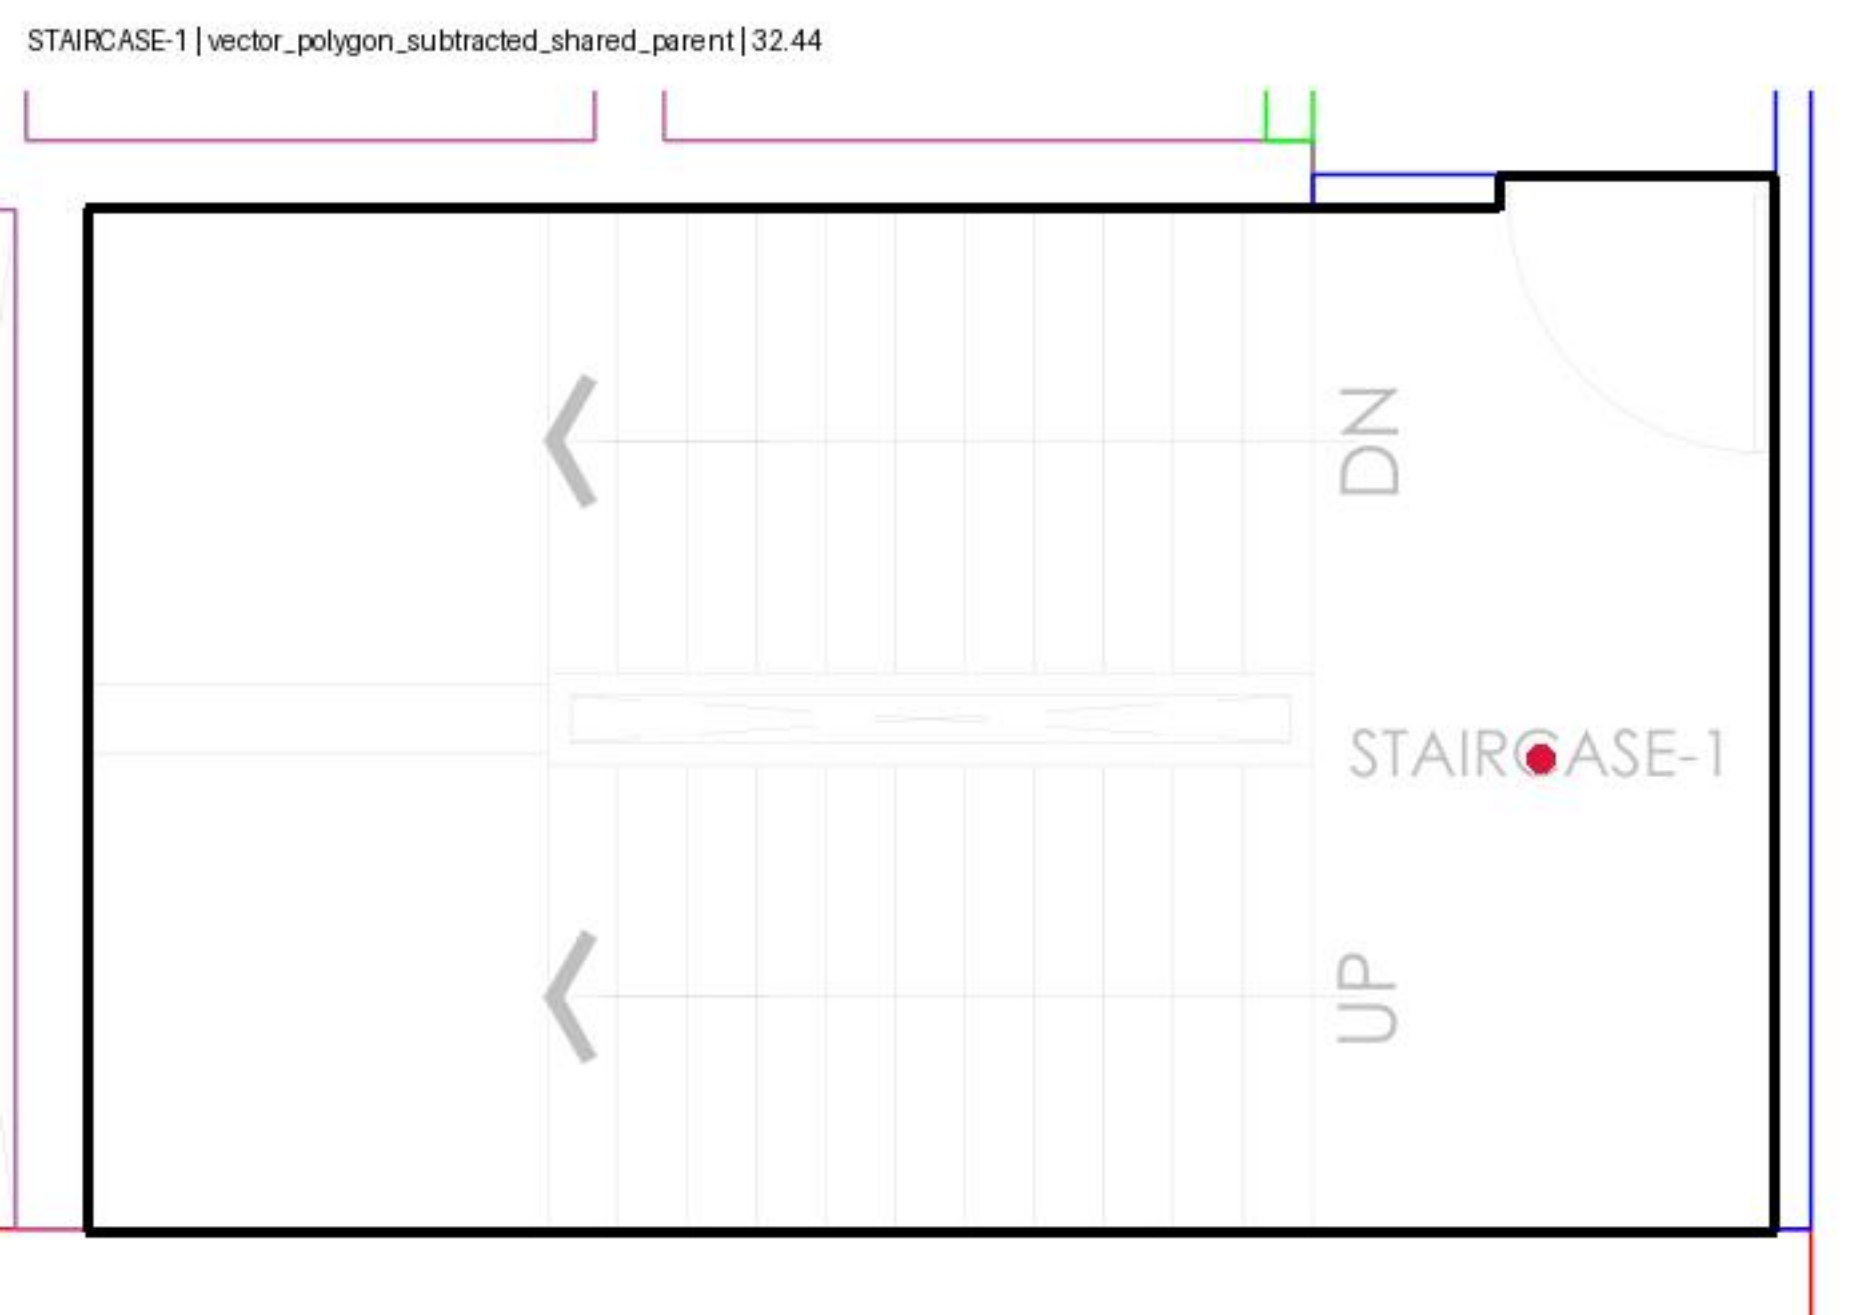
STAIRCASE-1 | vector_polygon_subtracted_shared_parent | 32.44
DN
STAIRCASE-1
UP

F LOBBY | vector_polygon_subtracted_shared_parent

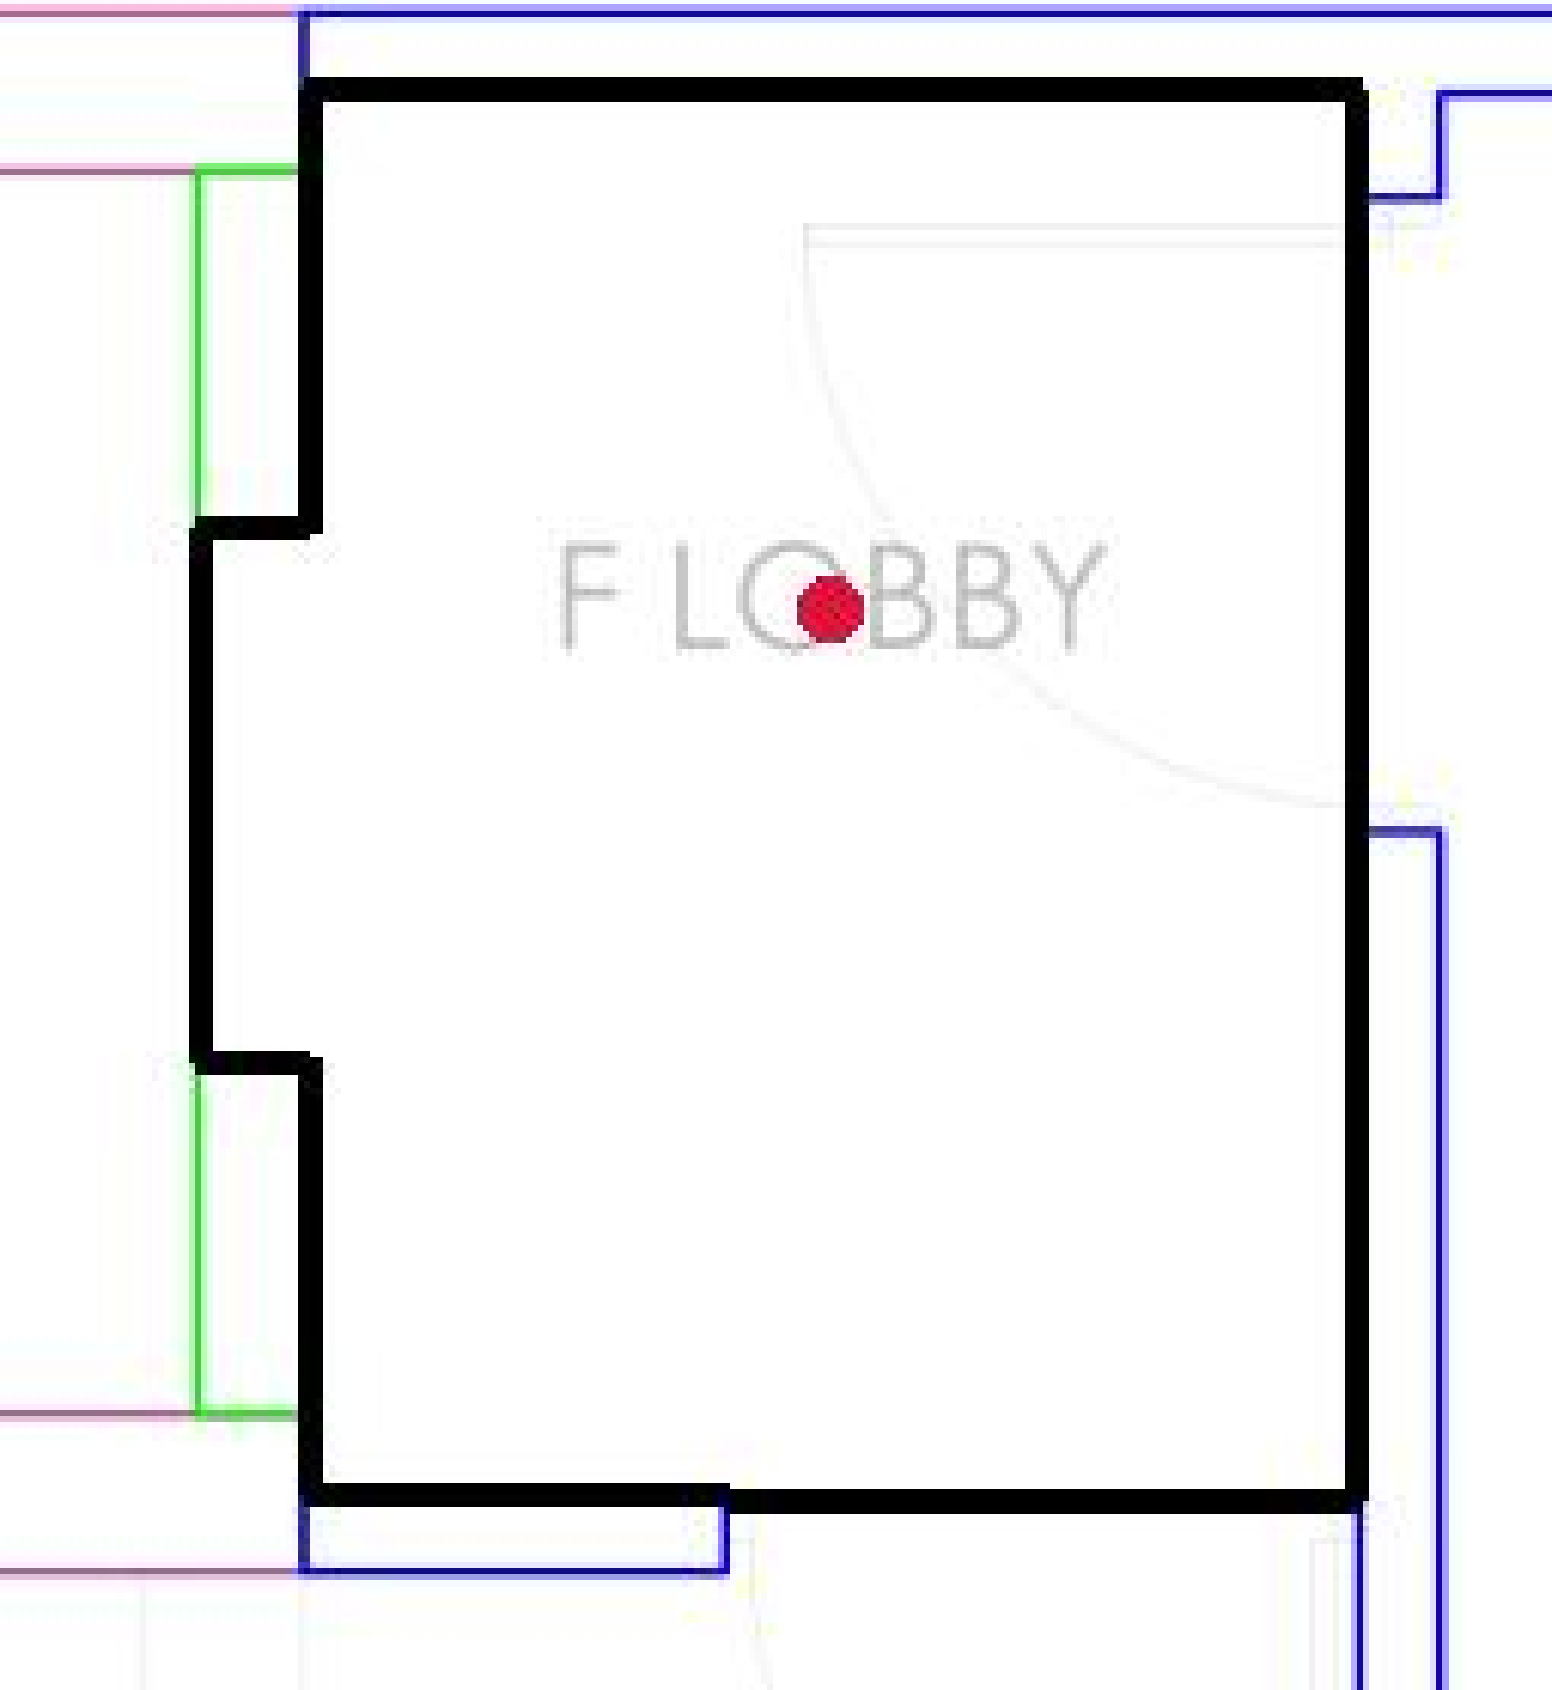

TOILET/PANTRY EXE | vector_polygon_exact | 1.8

LOBBY-3 | vector_polygon_closed_gap | 16.52

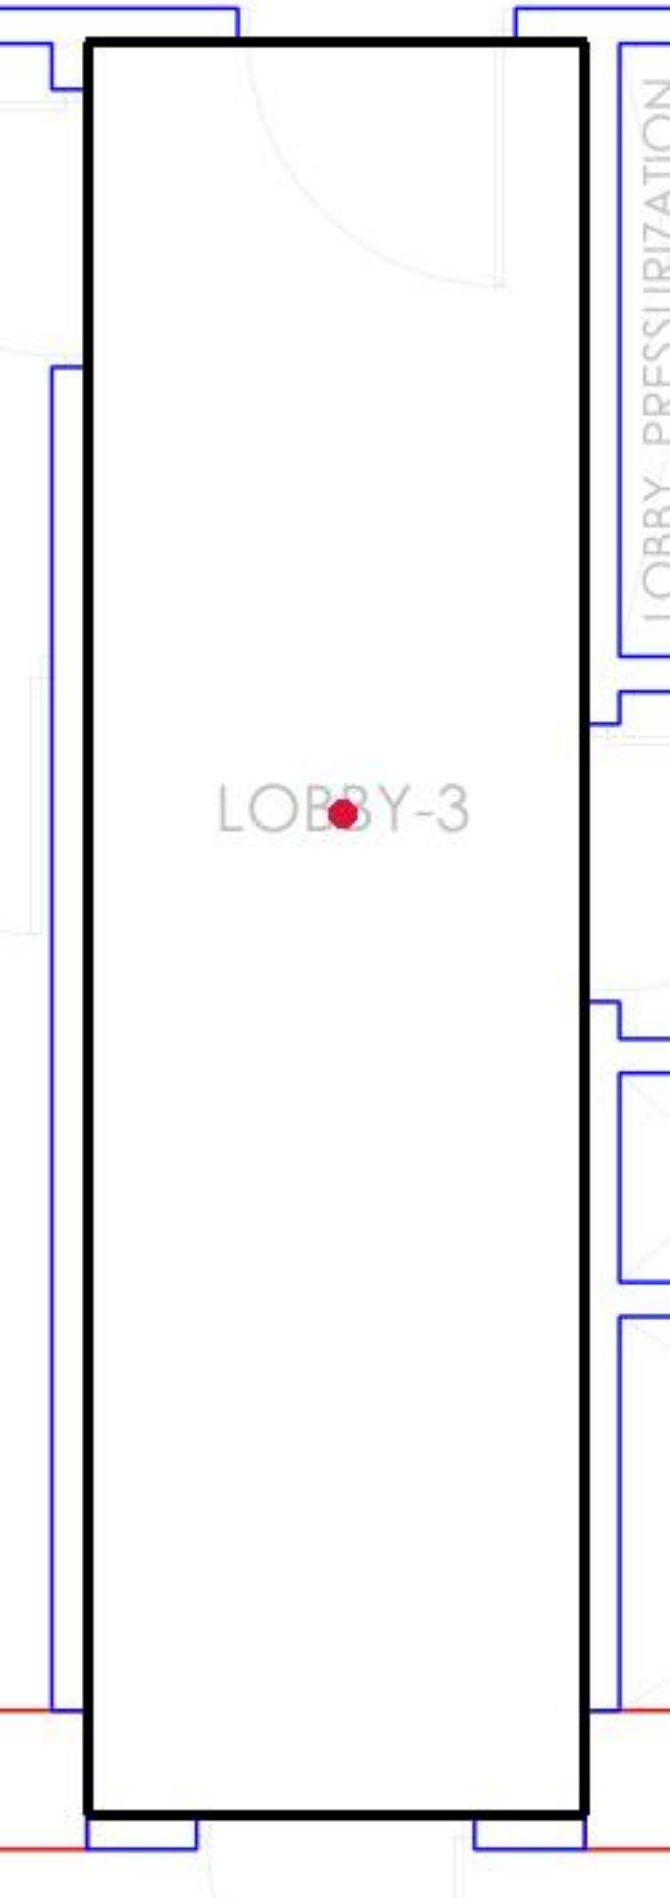

STR PRESSURIZATION S

PLUMBING SHAFT | vector_polygon_exact | 1.6

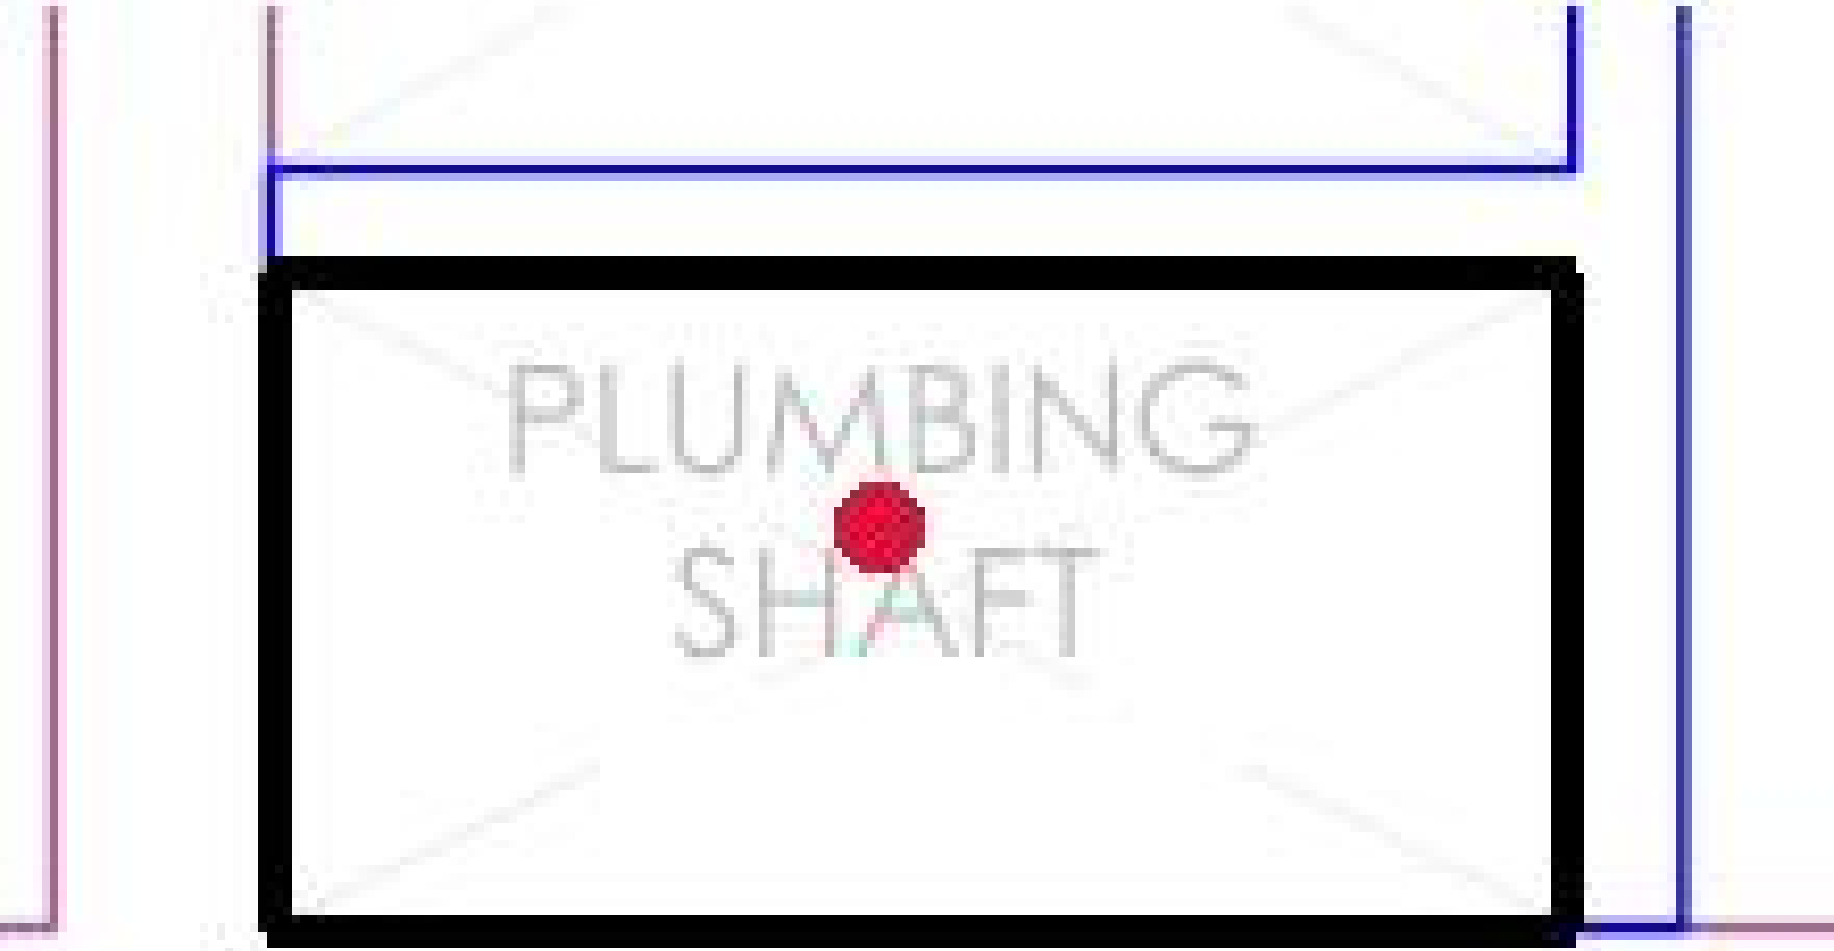

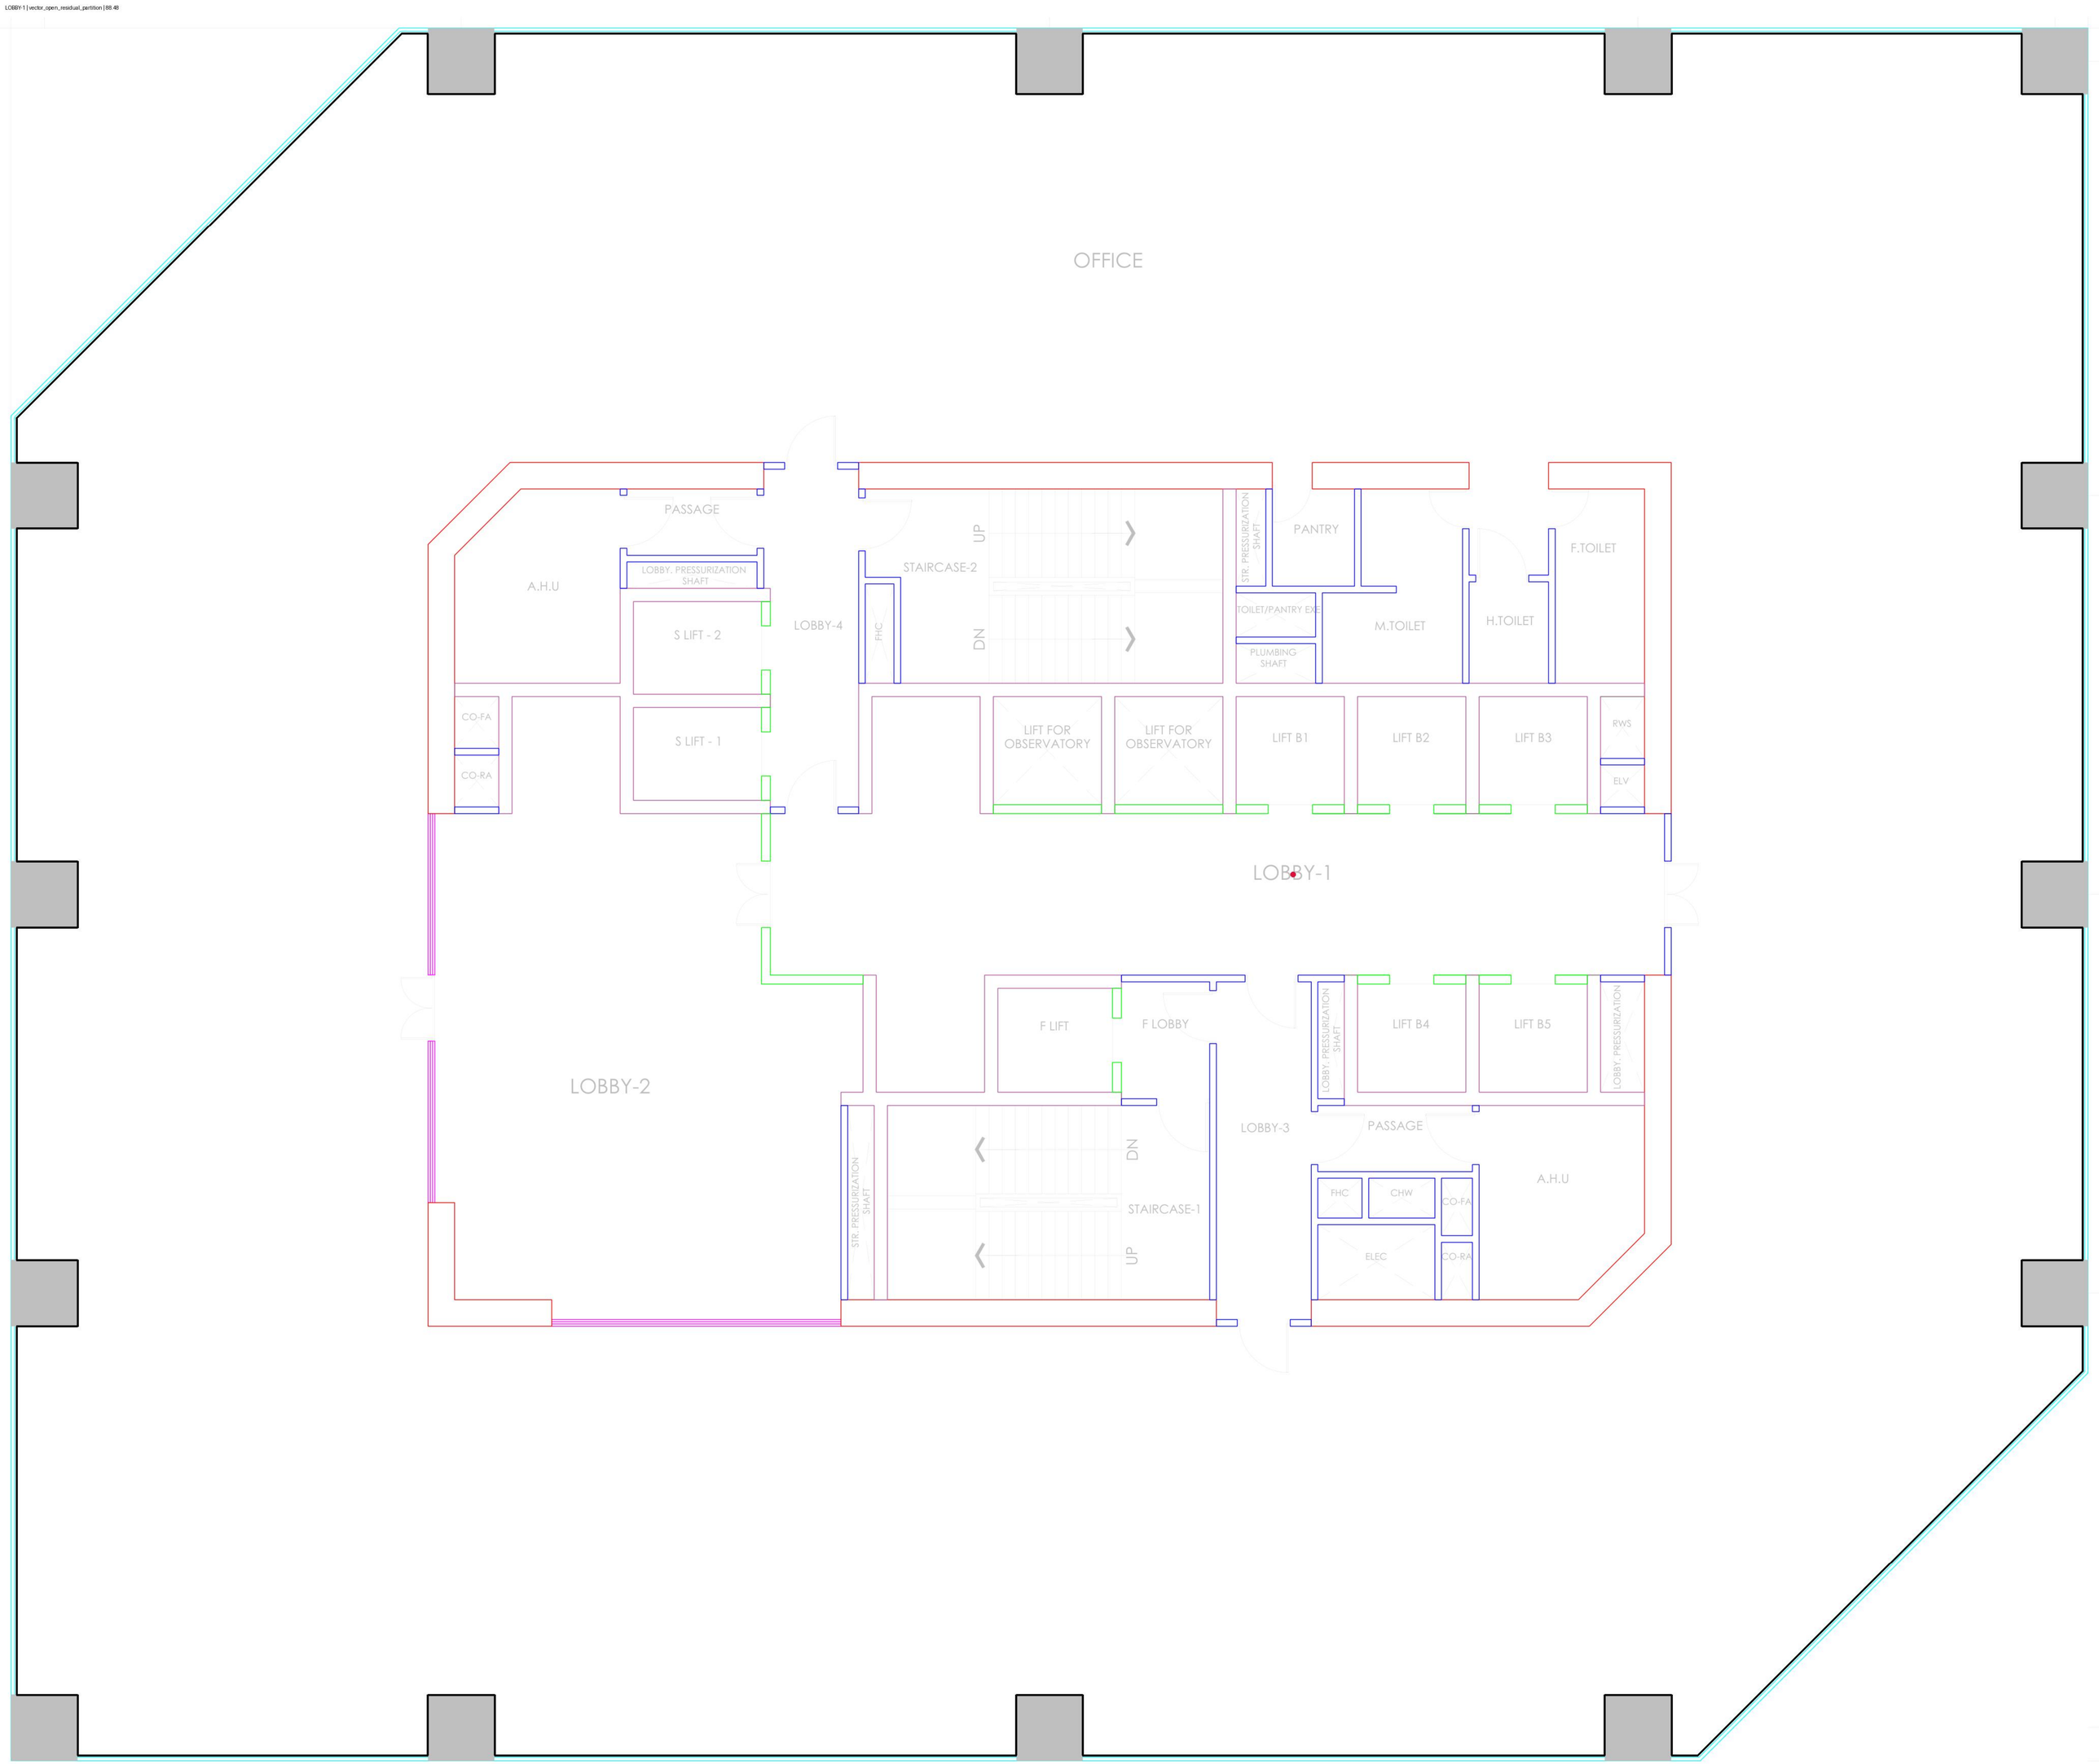
OFFICE
PASSAGE
A.H.U
LOBBY. PRESSURIZATION SHAFT
S LIFT - 2
S LIFT - 1
CO-FA
CO-RA
LOBBY-4
FHC
STAIRCASE-2
UP
DN
STR. PRESSURIZATION SHAFT
PANTRY
TOILET/PANTRY EXE
PLUMBING SHAFT
M.TOILET
H.TOILET
F.TOILET
LIFT FOR OBSERVATORY
LIFT FOR OBSERVATORY
LIFT B1
LIFT B2
LIFT B3
RWS
ELV
LOBBY-1
LOBBY-2
F LIFT
F LOBBY
LOBBY-3
LOBBY. PRESSURIZATION SHAFT
LIFT B4
LIFT B5
LOBBY. PRESSURIZATION
PASSAGE
A.H.U
FHC
CHW
CO-FA
ELEC
CO-RA
STR. PRESSURIZATION SHAFT
DN
STAIRCASE-1
UP

LIFT B1 | vector_polygon_exact | 6.03

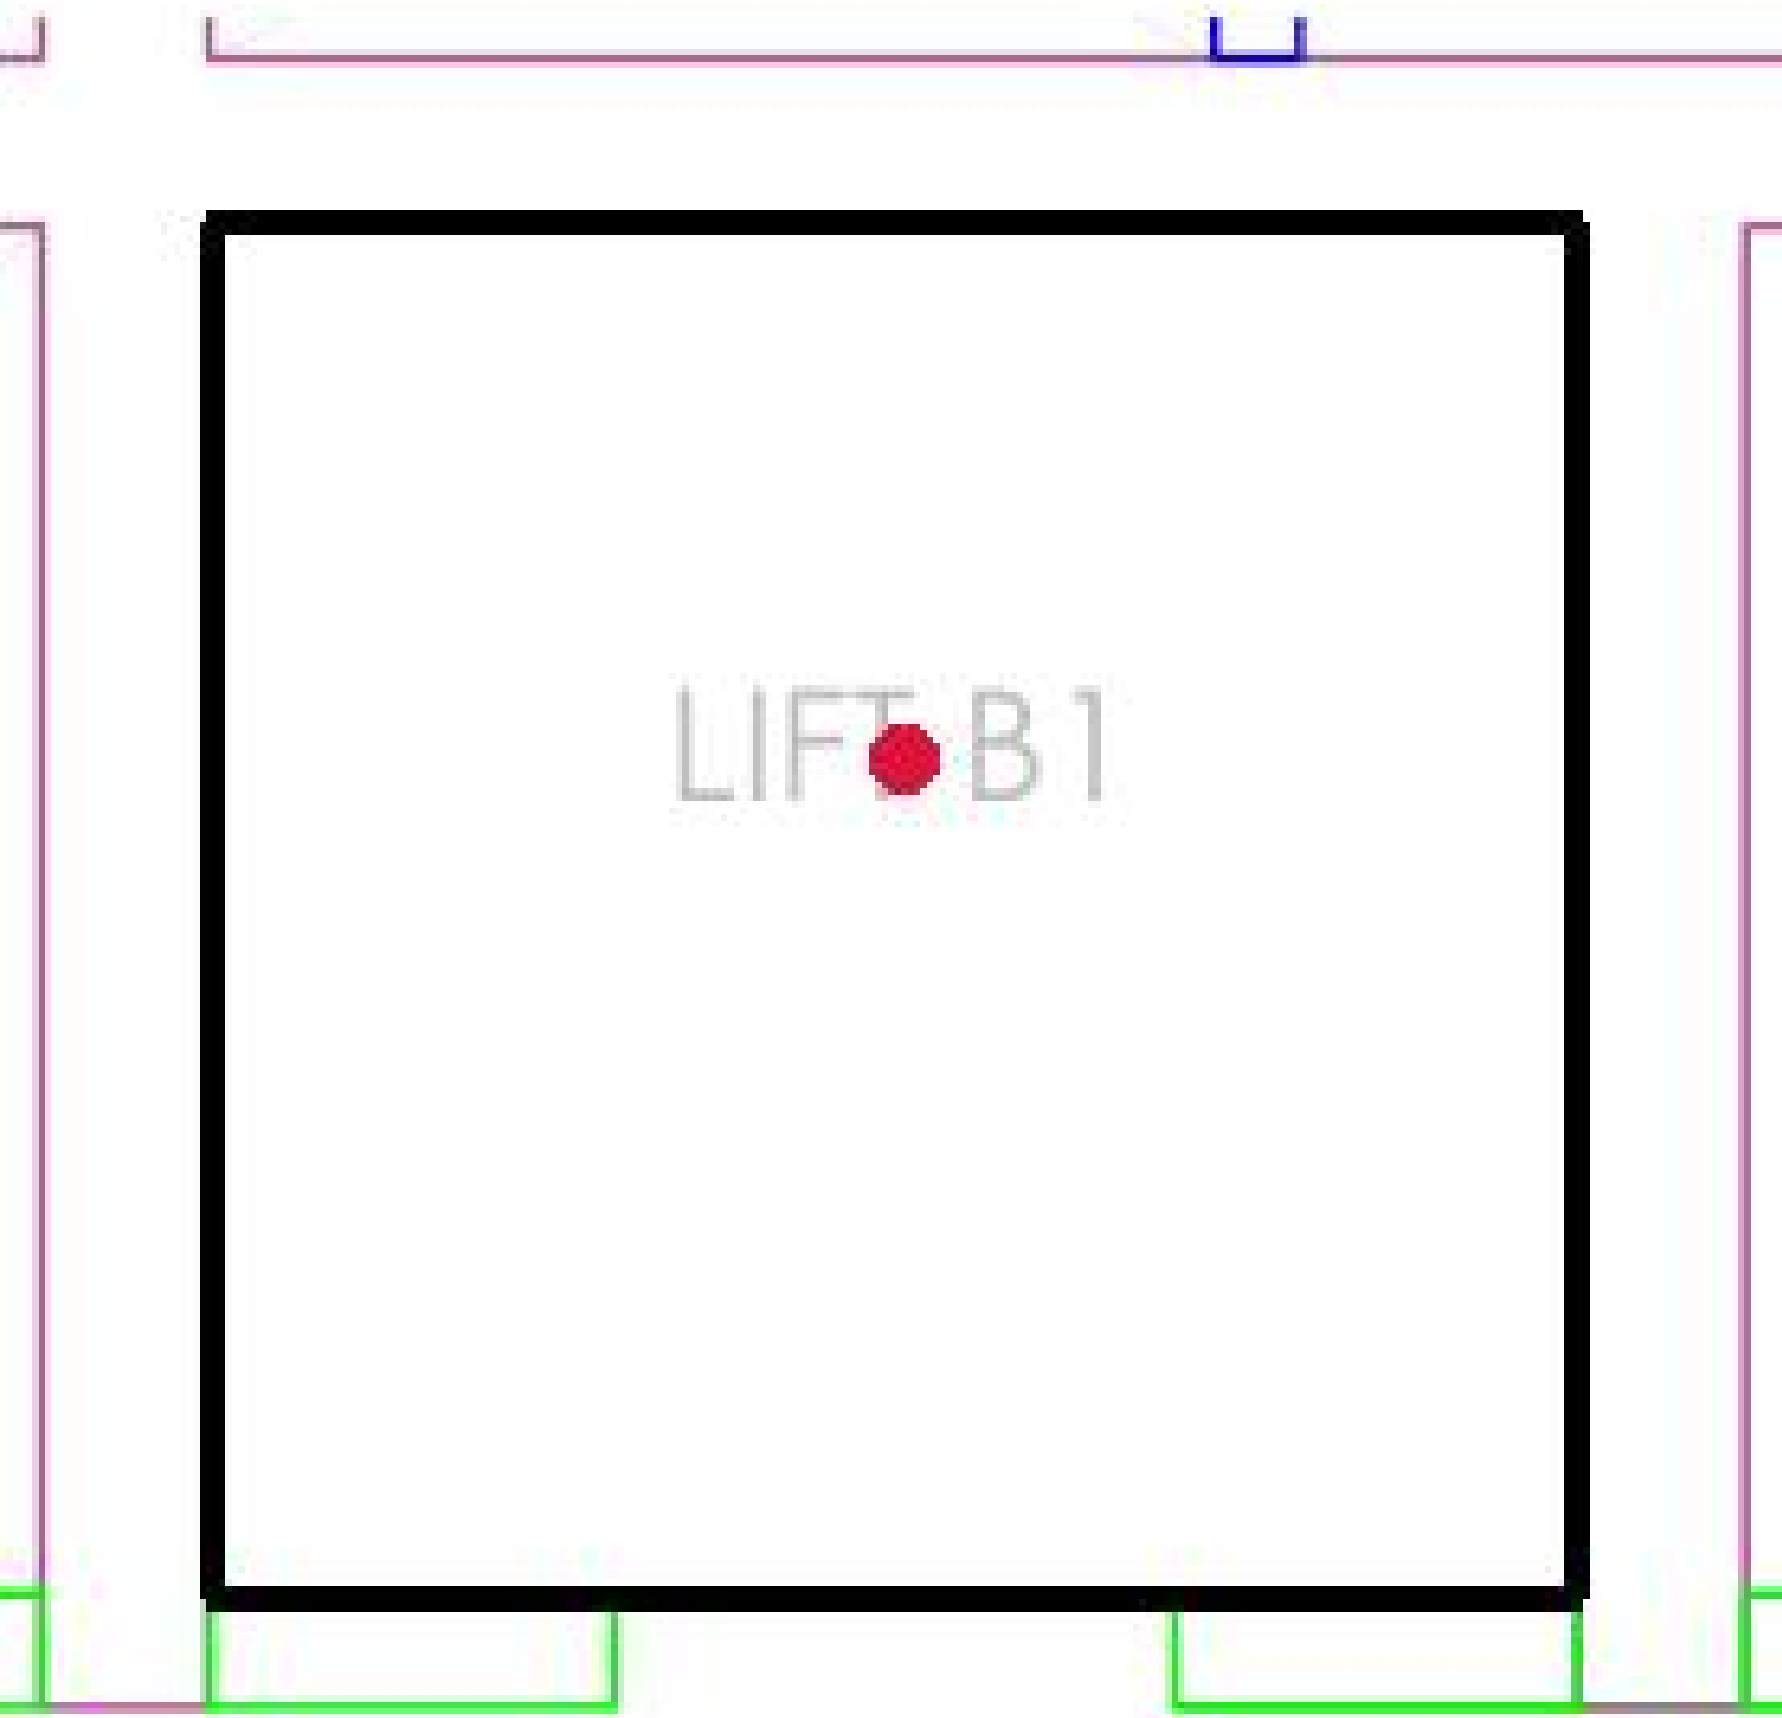

PANTRY | vector_polygon_closed_gap | 4.12

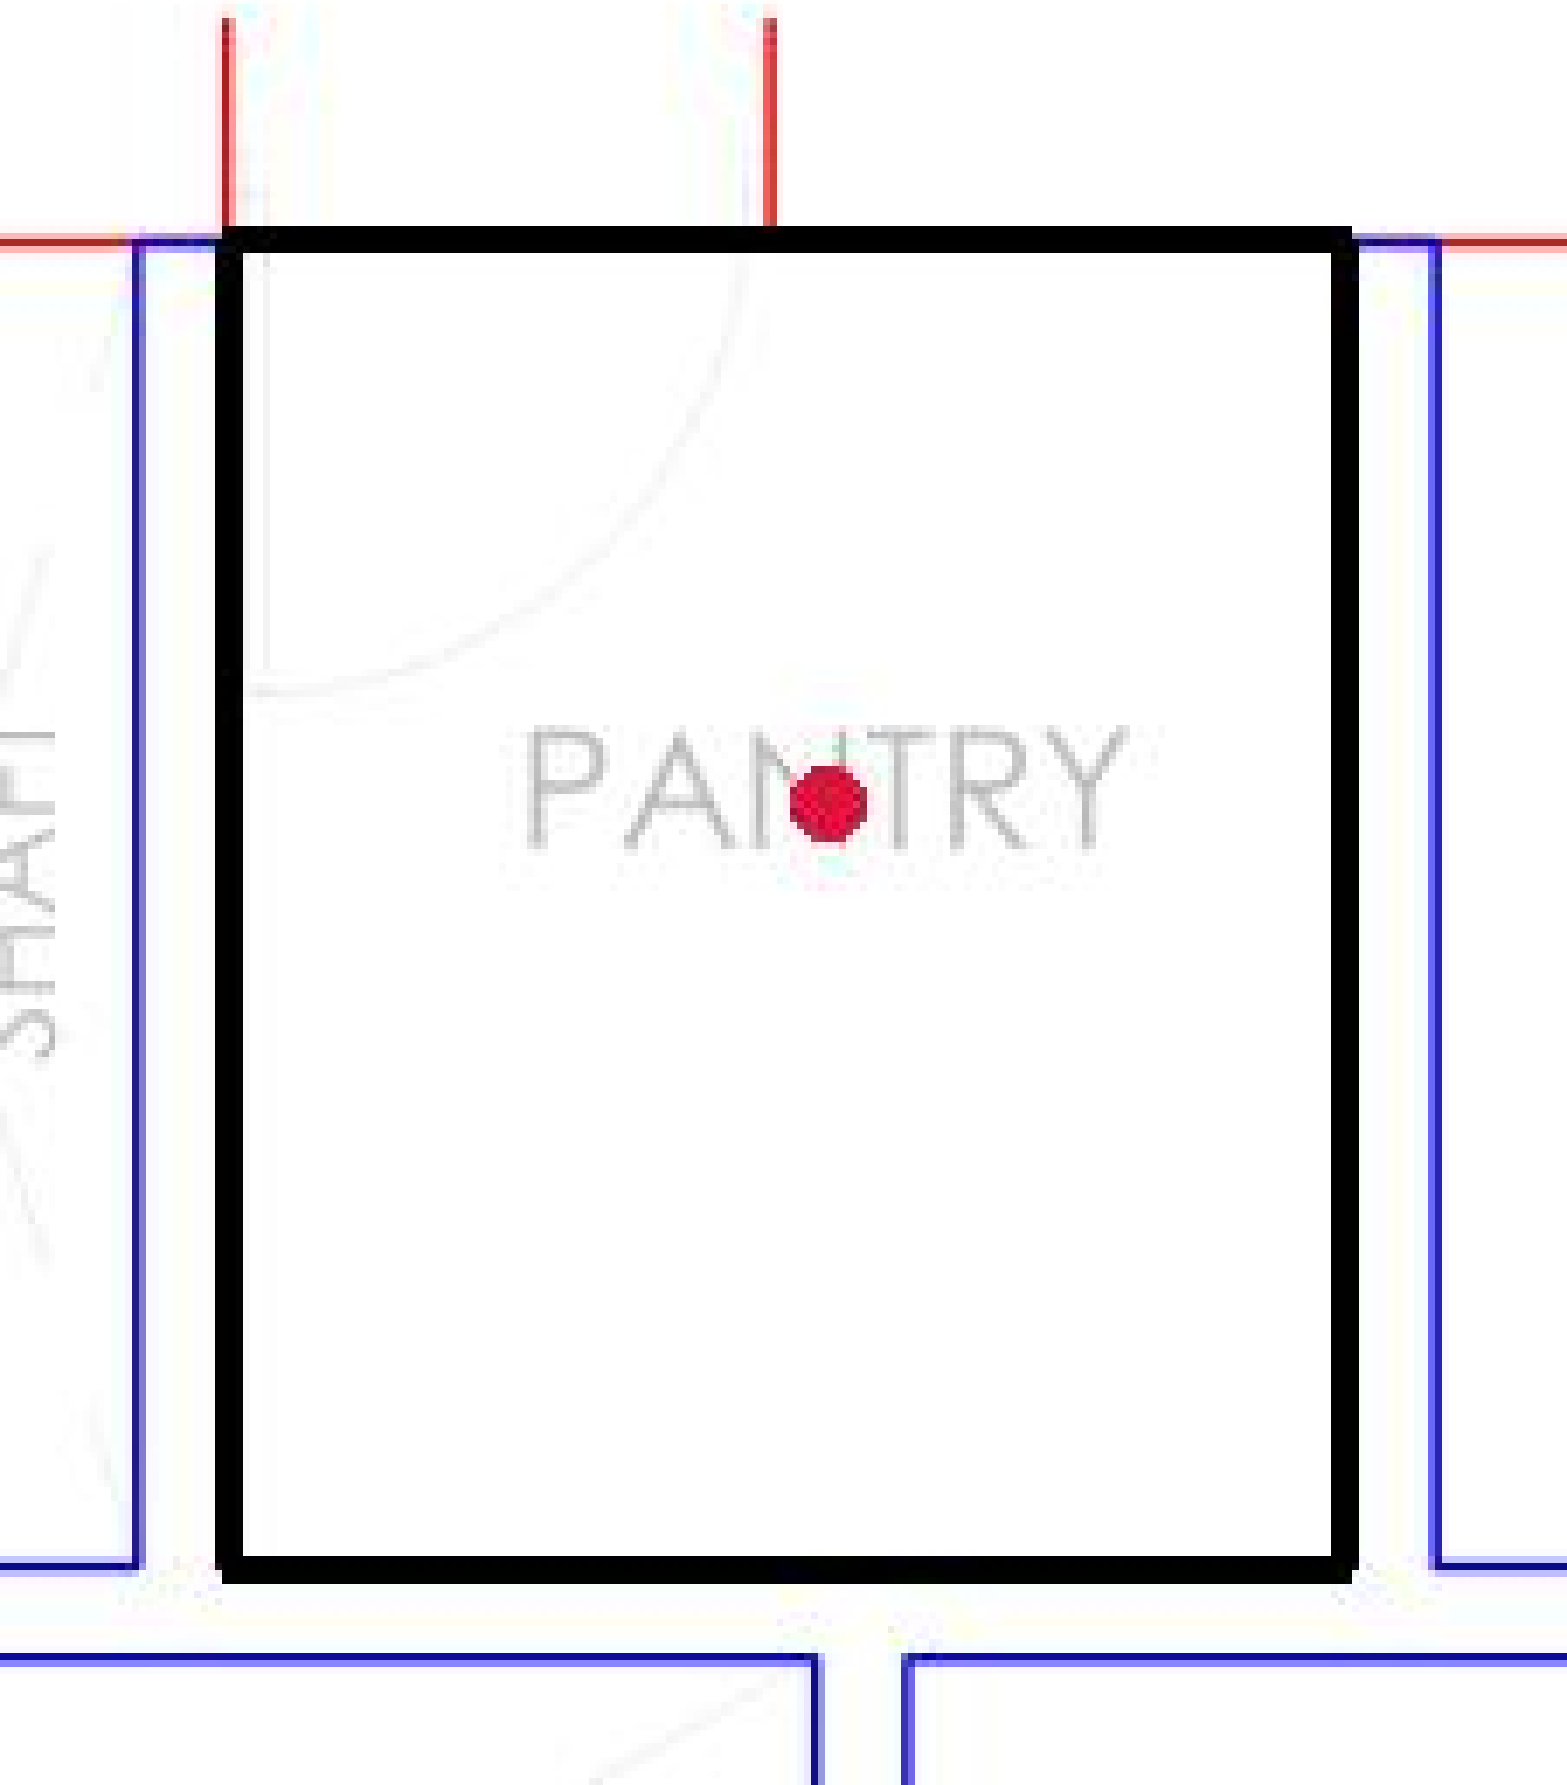

LOBBY. PRESSURIZATIO

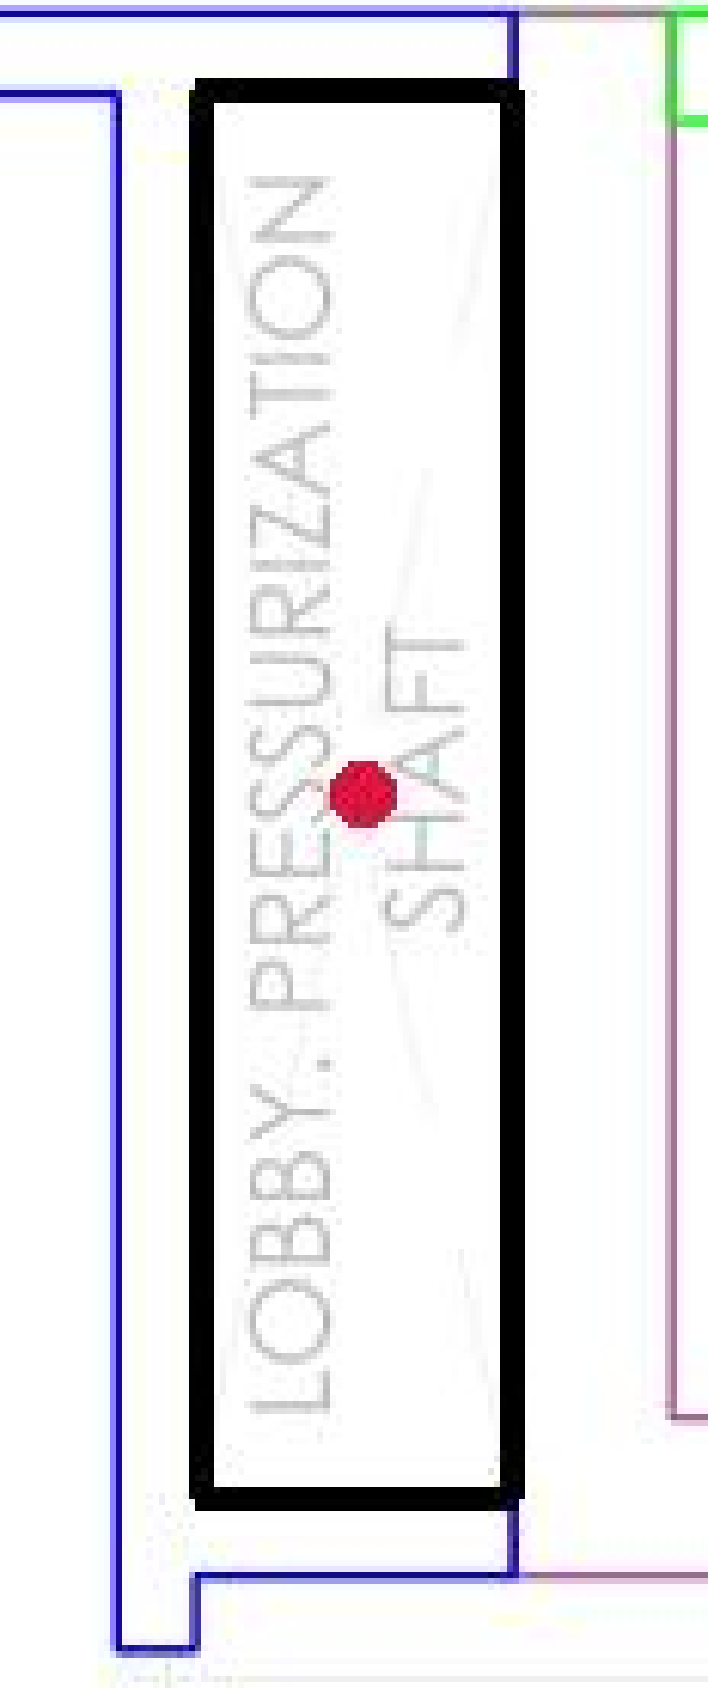

FHC | vector_polygon_exact | 0.

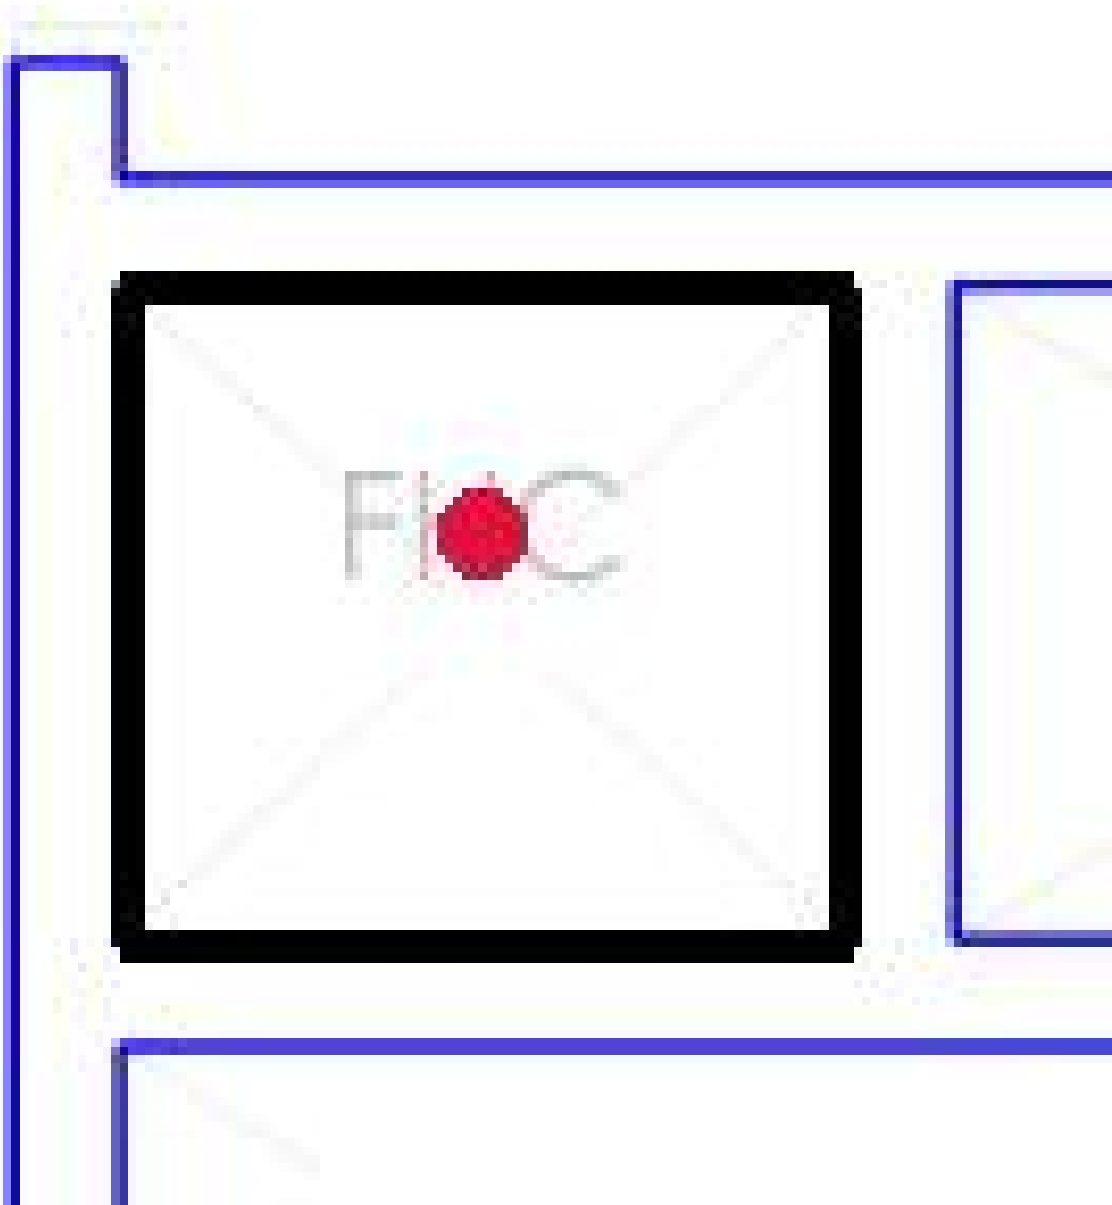

ELEC | vector_polygon_exact | 4.54

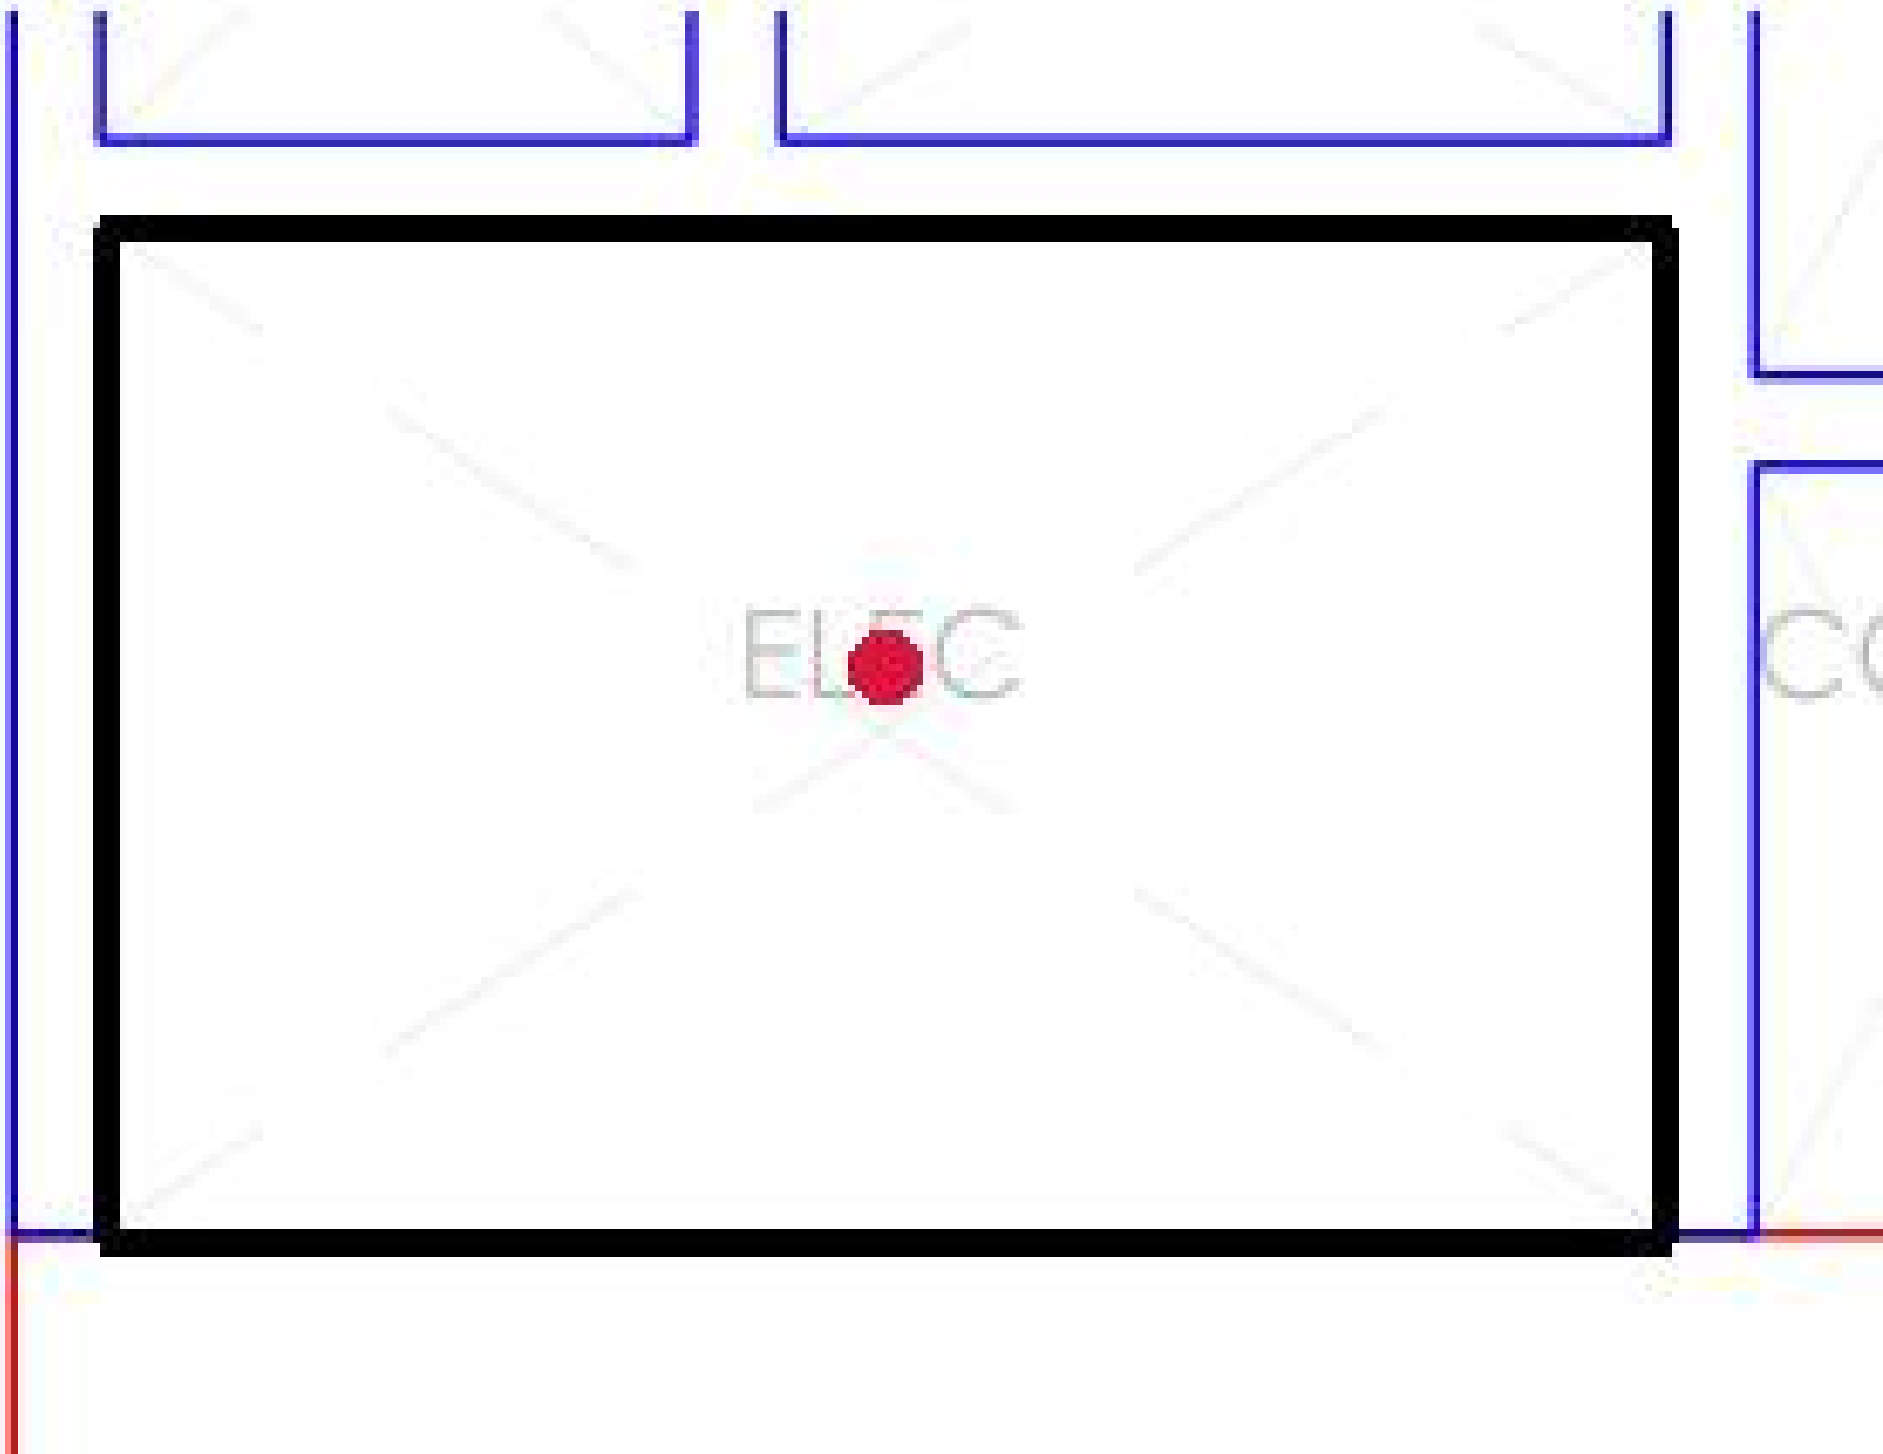

PASSAGE | vector_polygon_closed_gap | 5.27

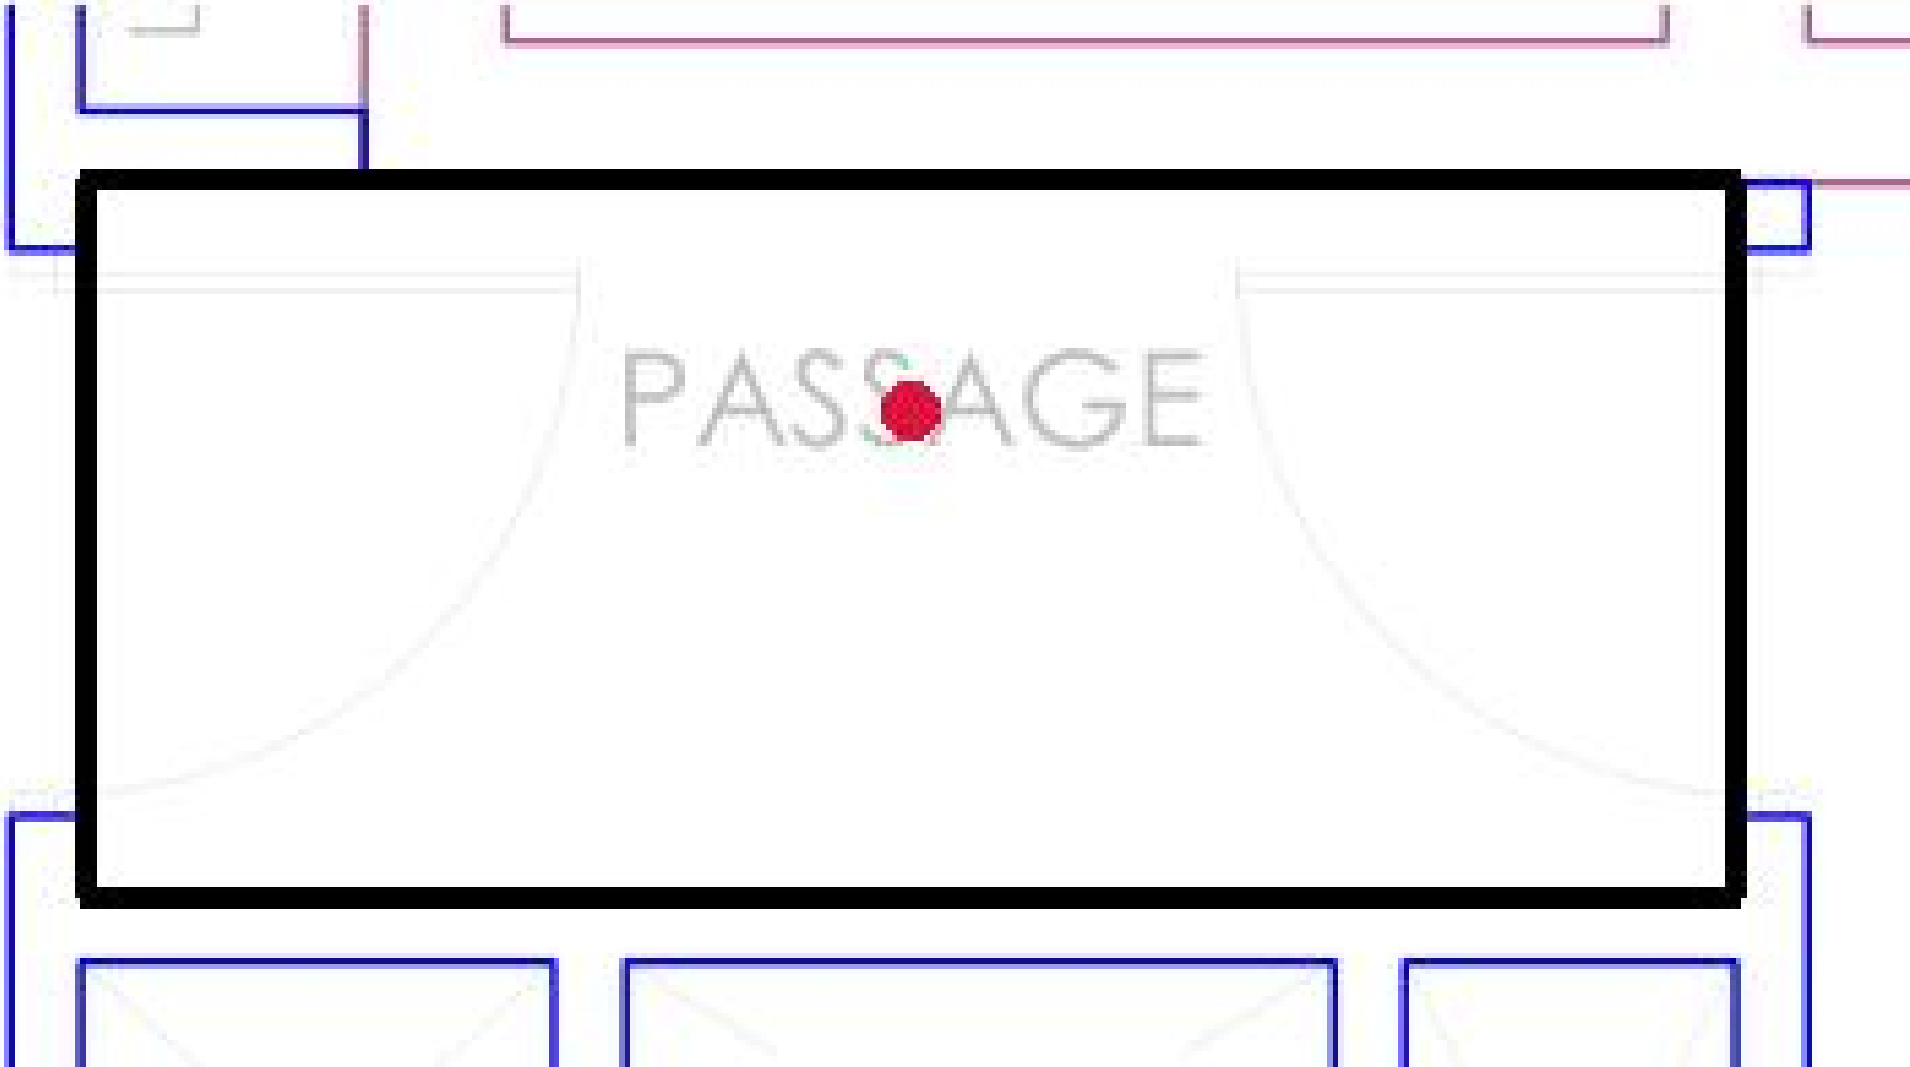

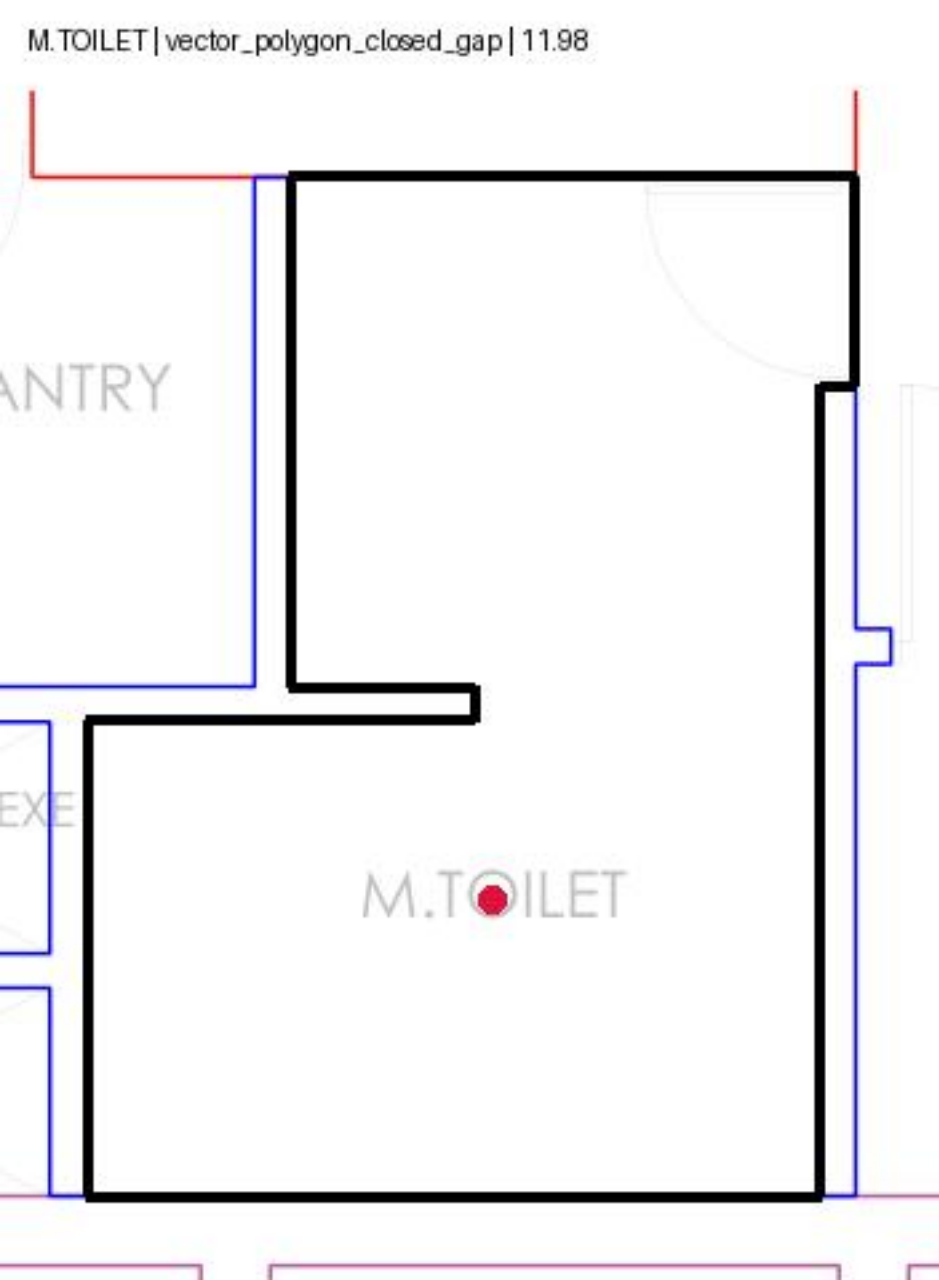
M.TOILET | vector_polygon_closed_gap | 11.98
ANTRY
EXE
M.TOILET

CHW | vector_polygon_exact | 1.36

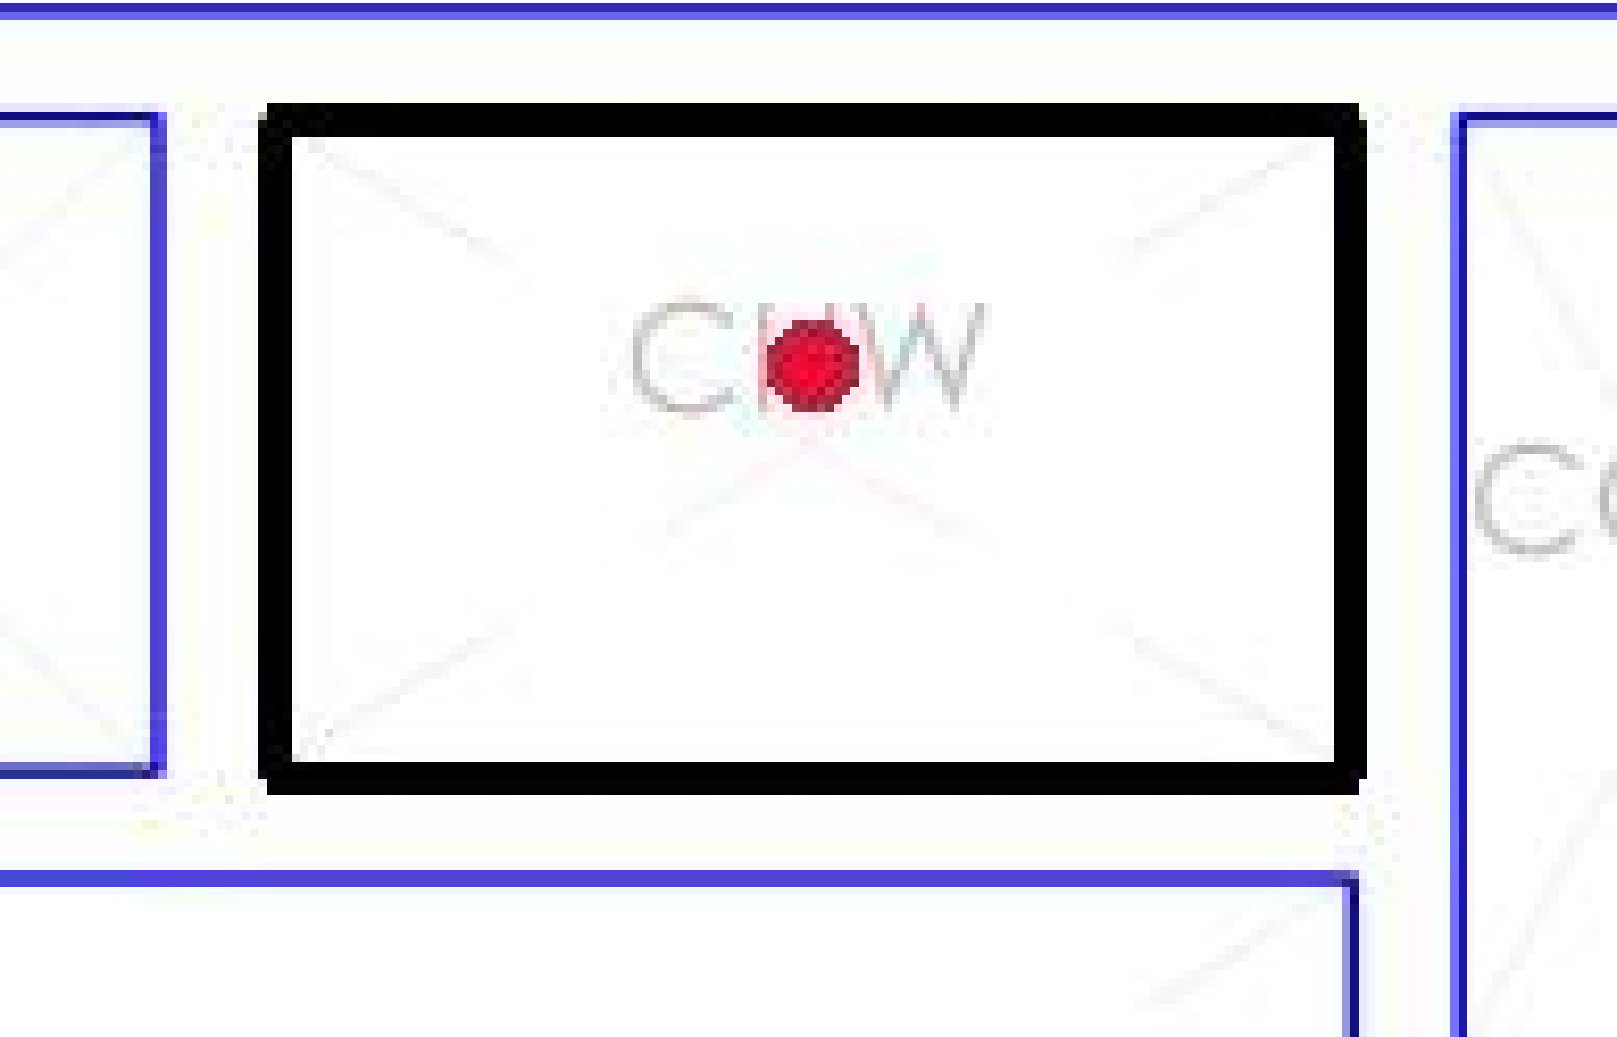

LIFT B4 | vector_polygon_exact | 6.04

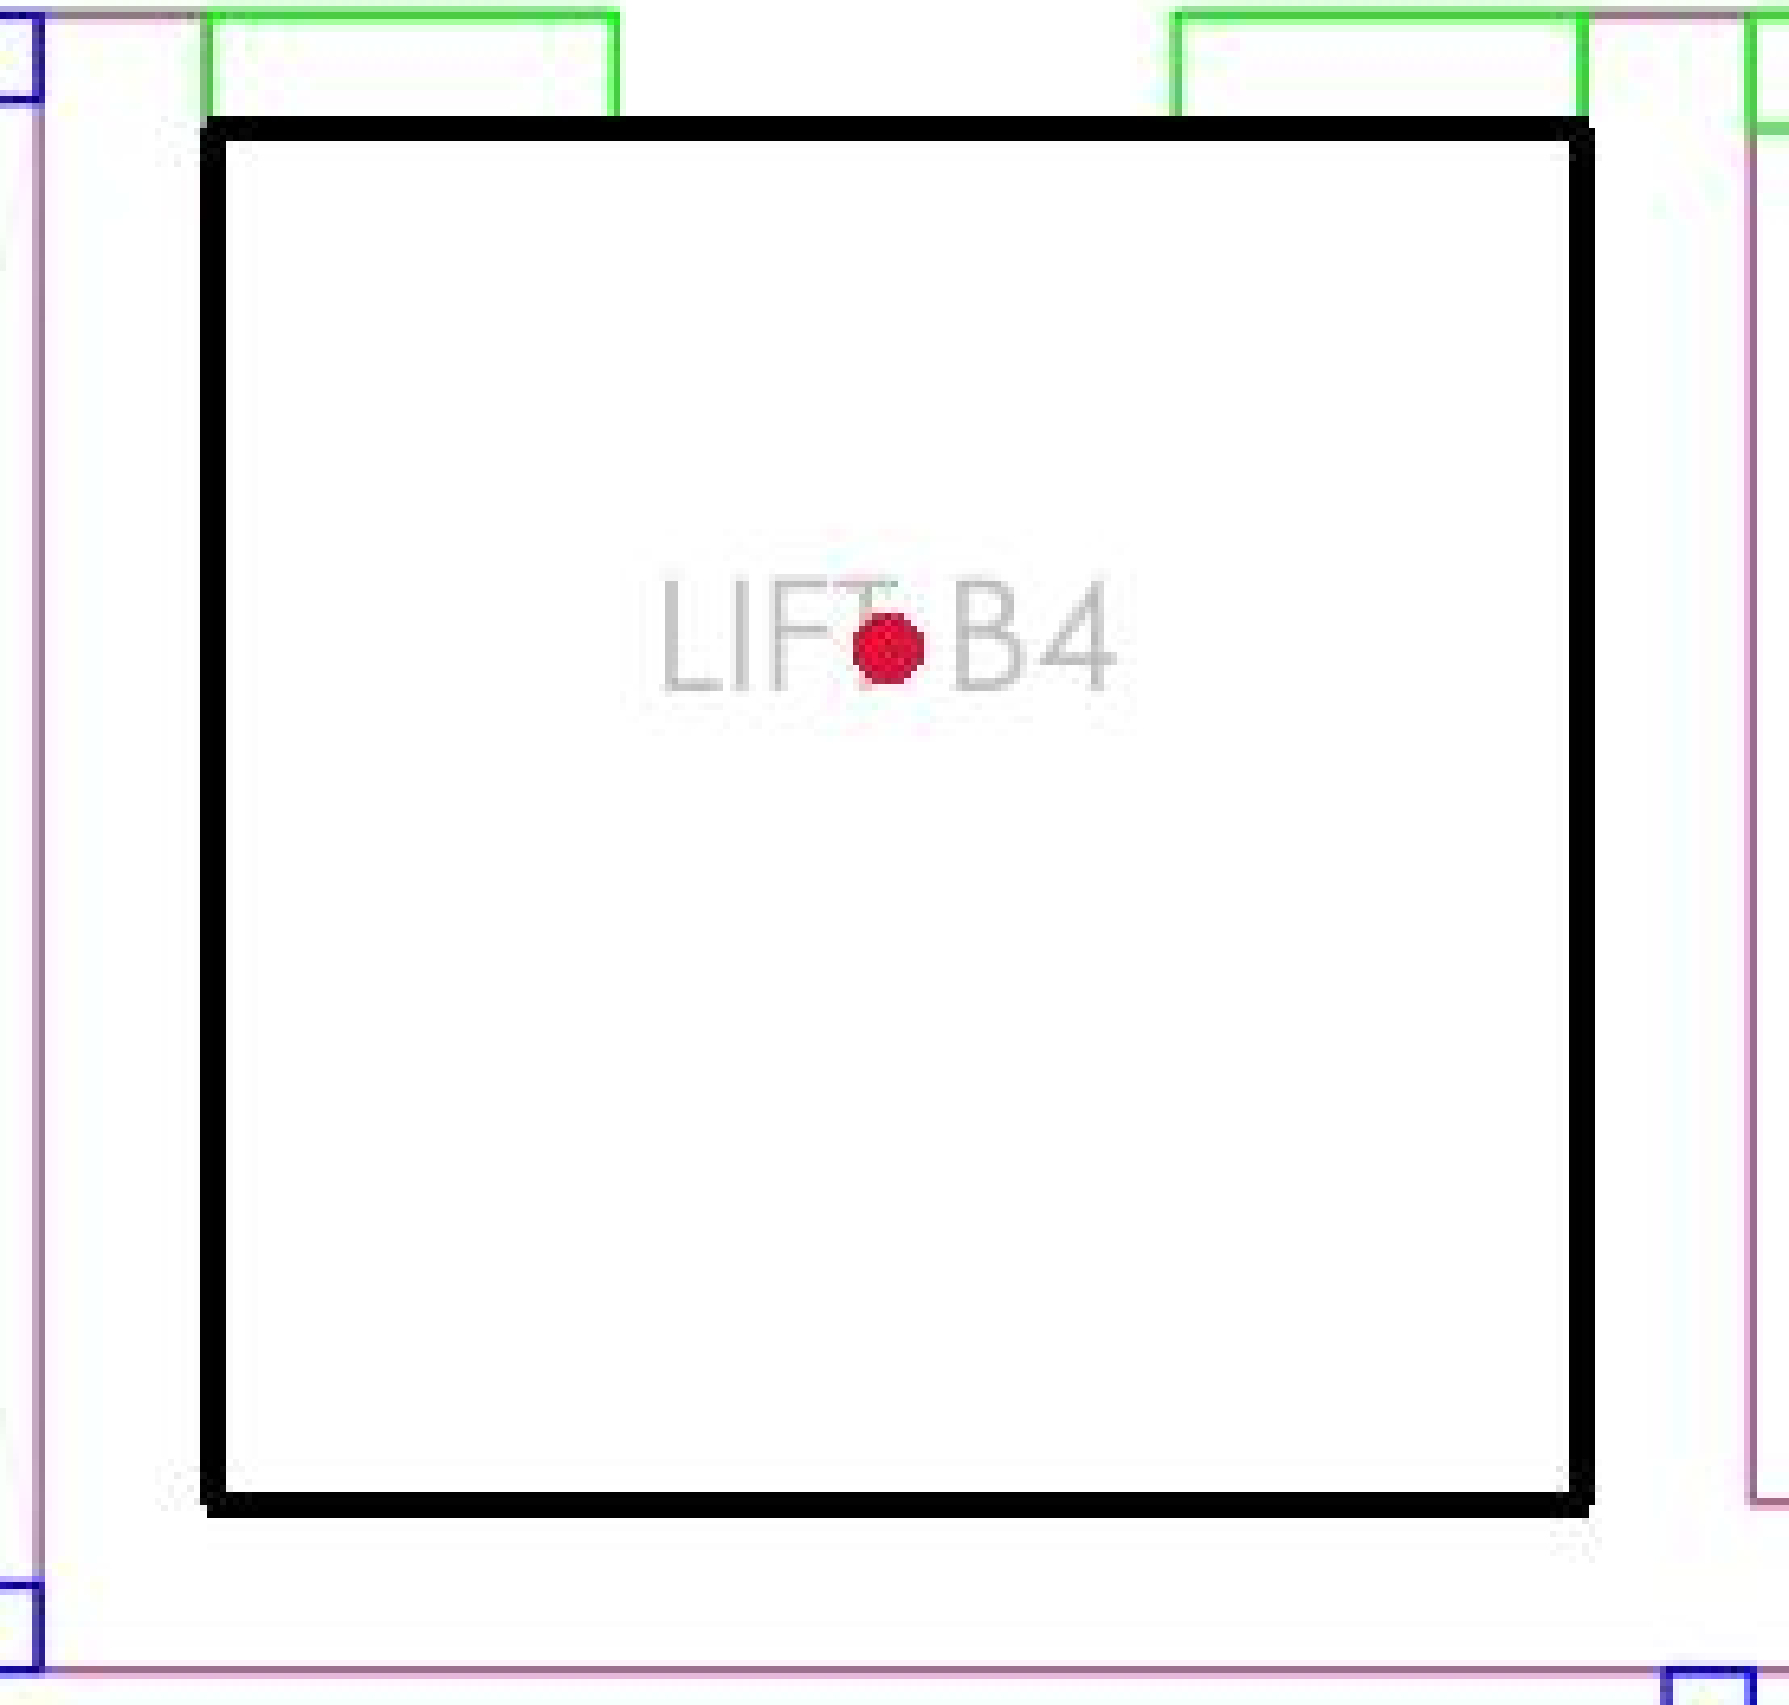

LIFT B2 | vector_polygon_exact | 6.04

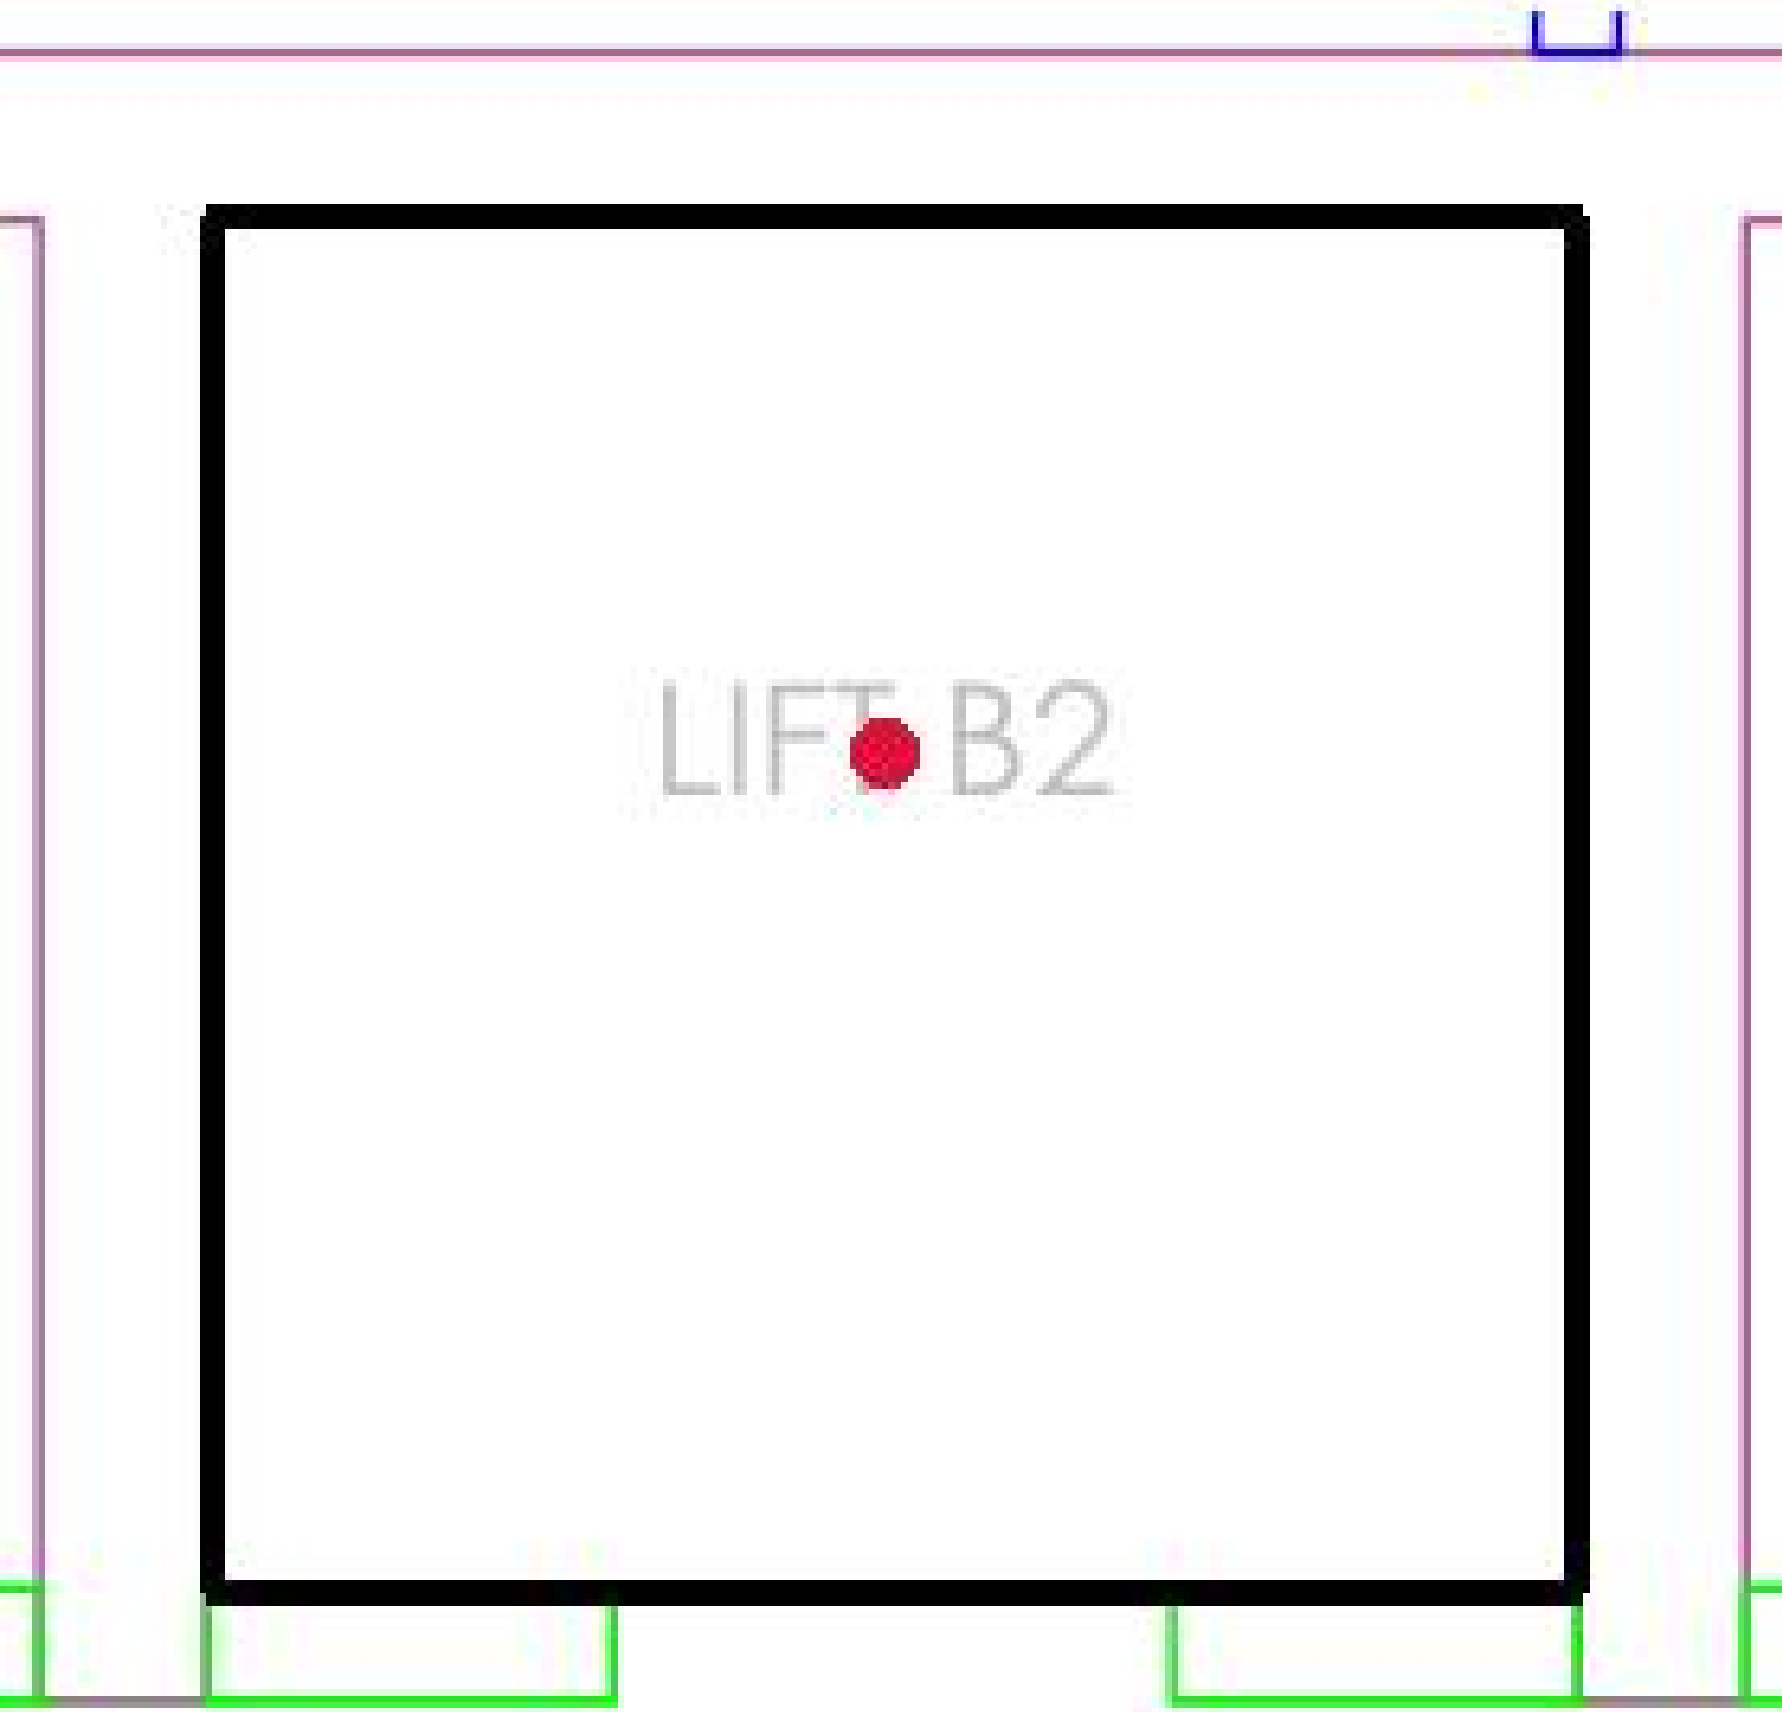

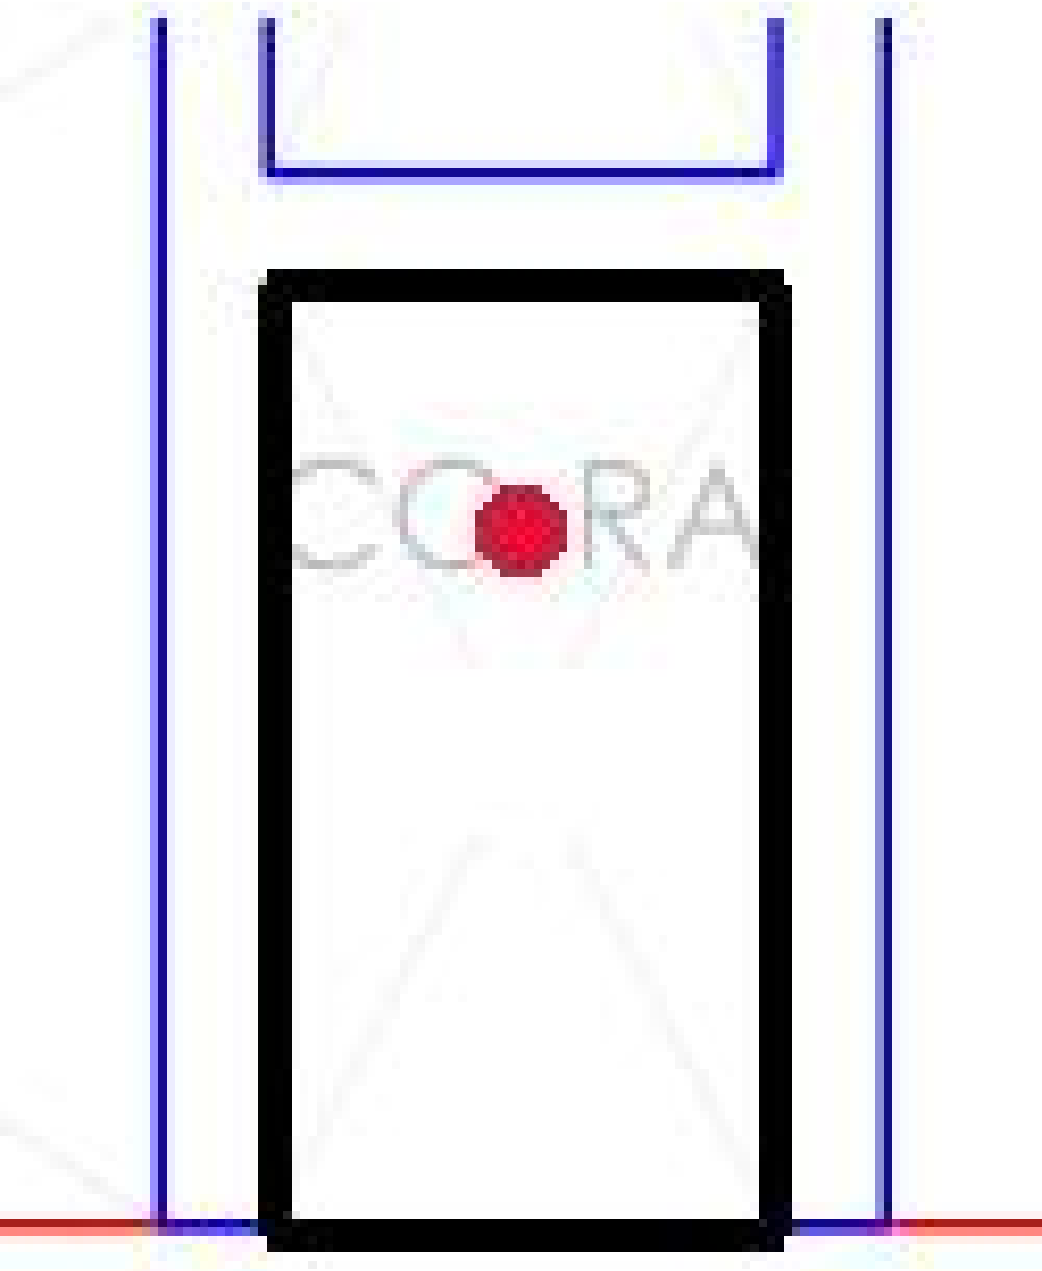

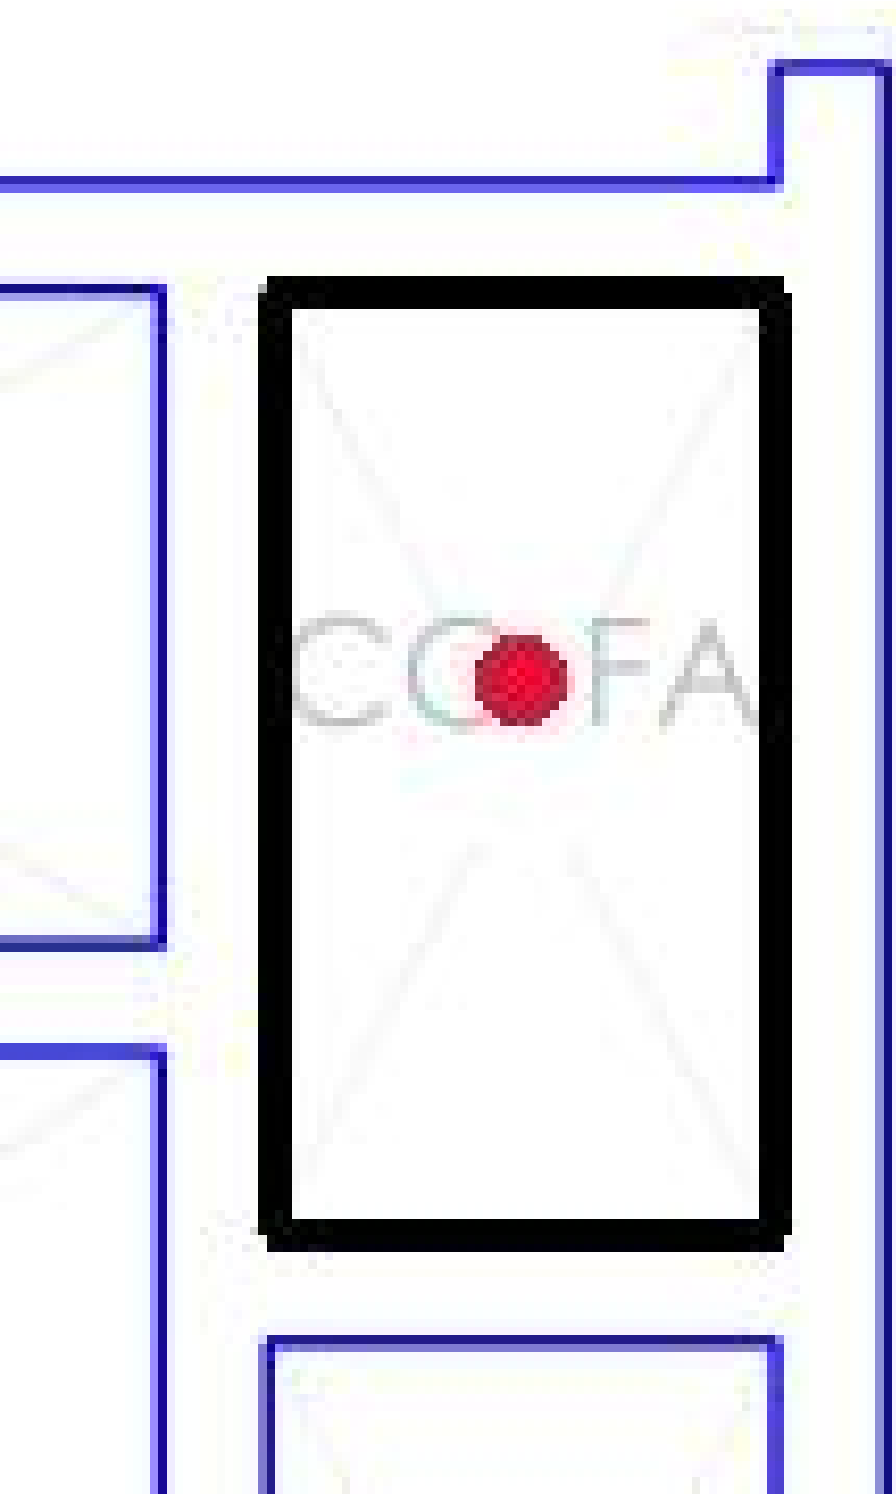
CO FA

H.TOILET | vector_polygon_closed_gap | 4.15

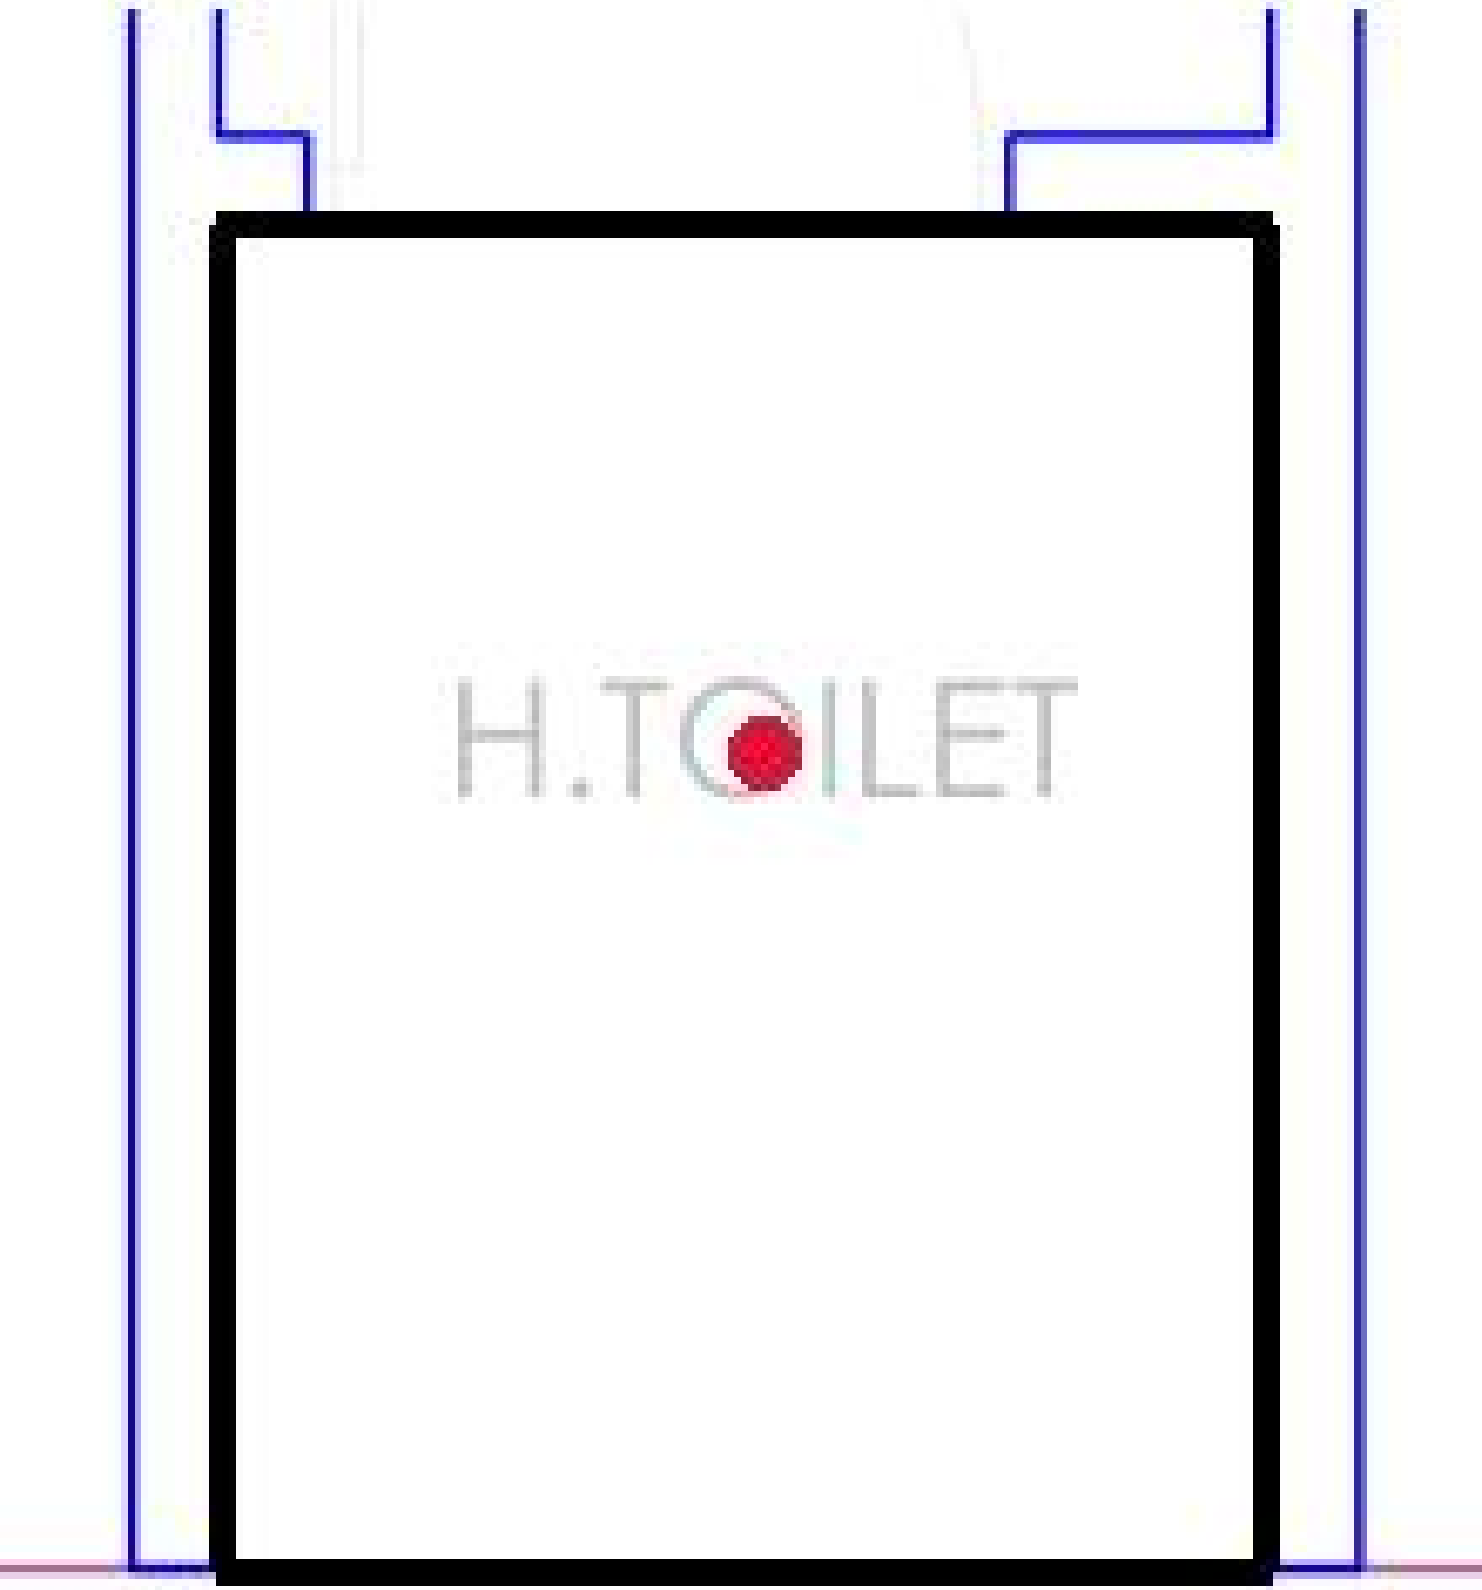

LIFT B5 | vector_polygon_exact | 6.03

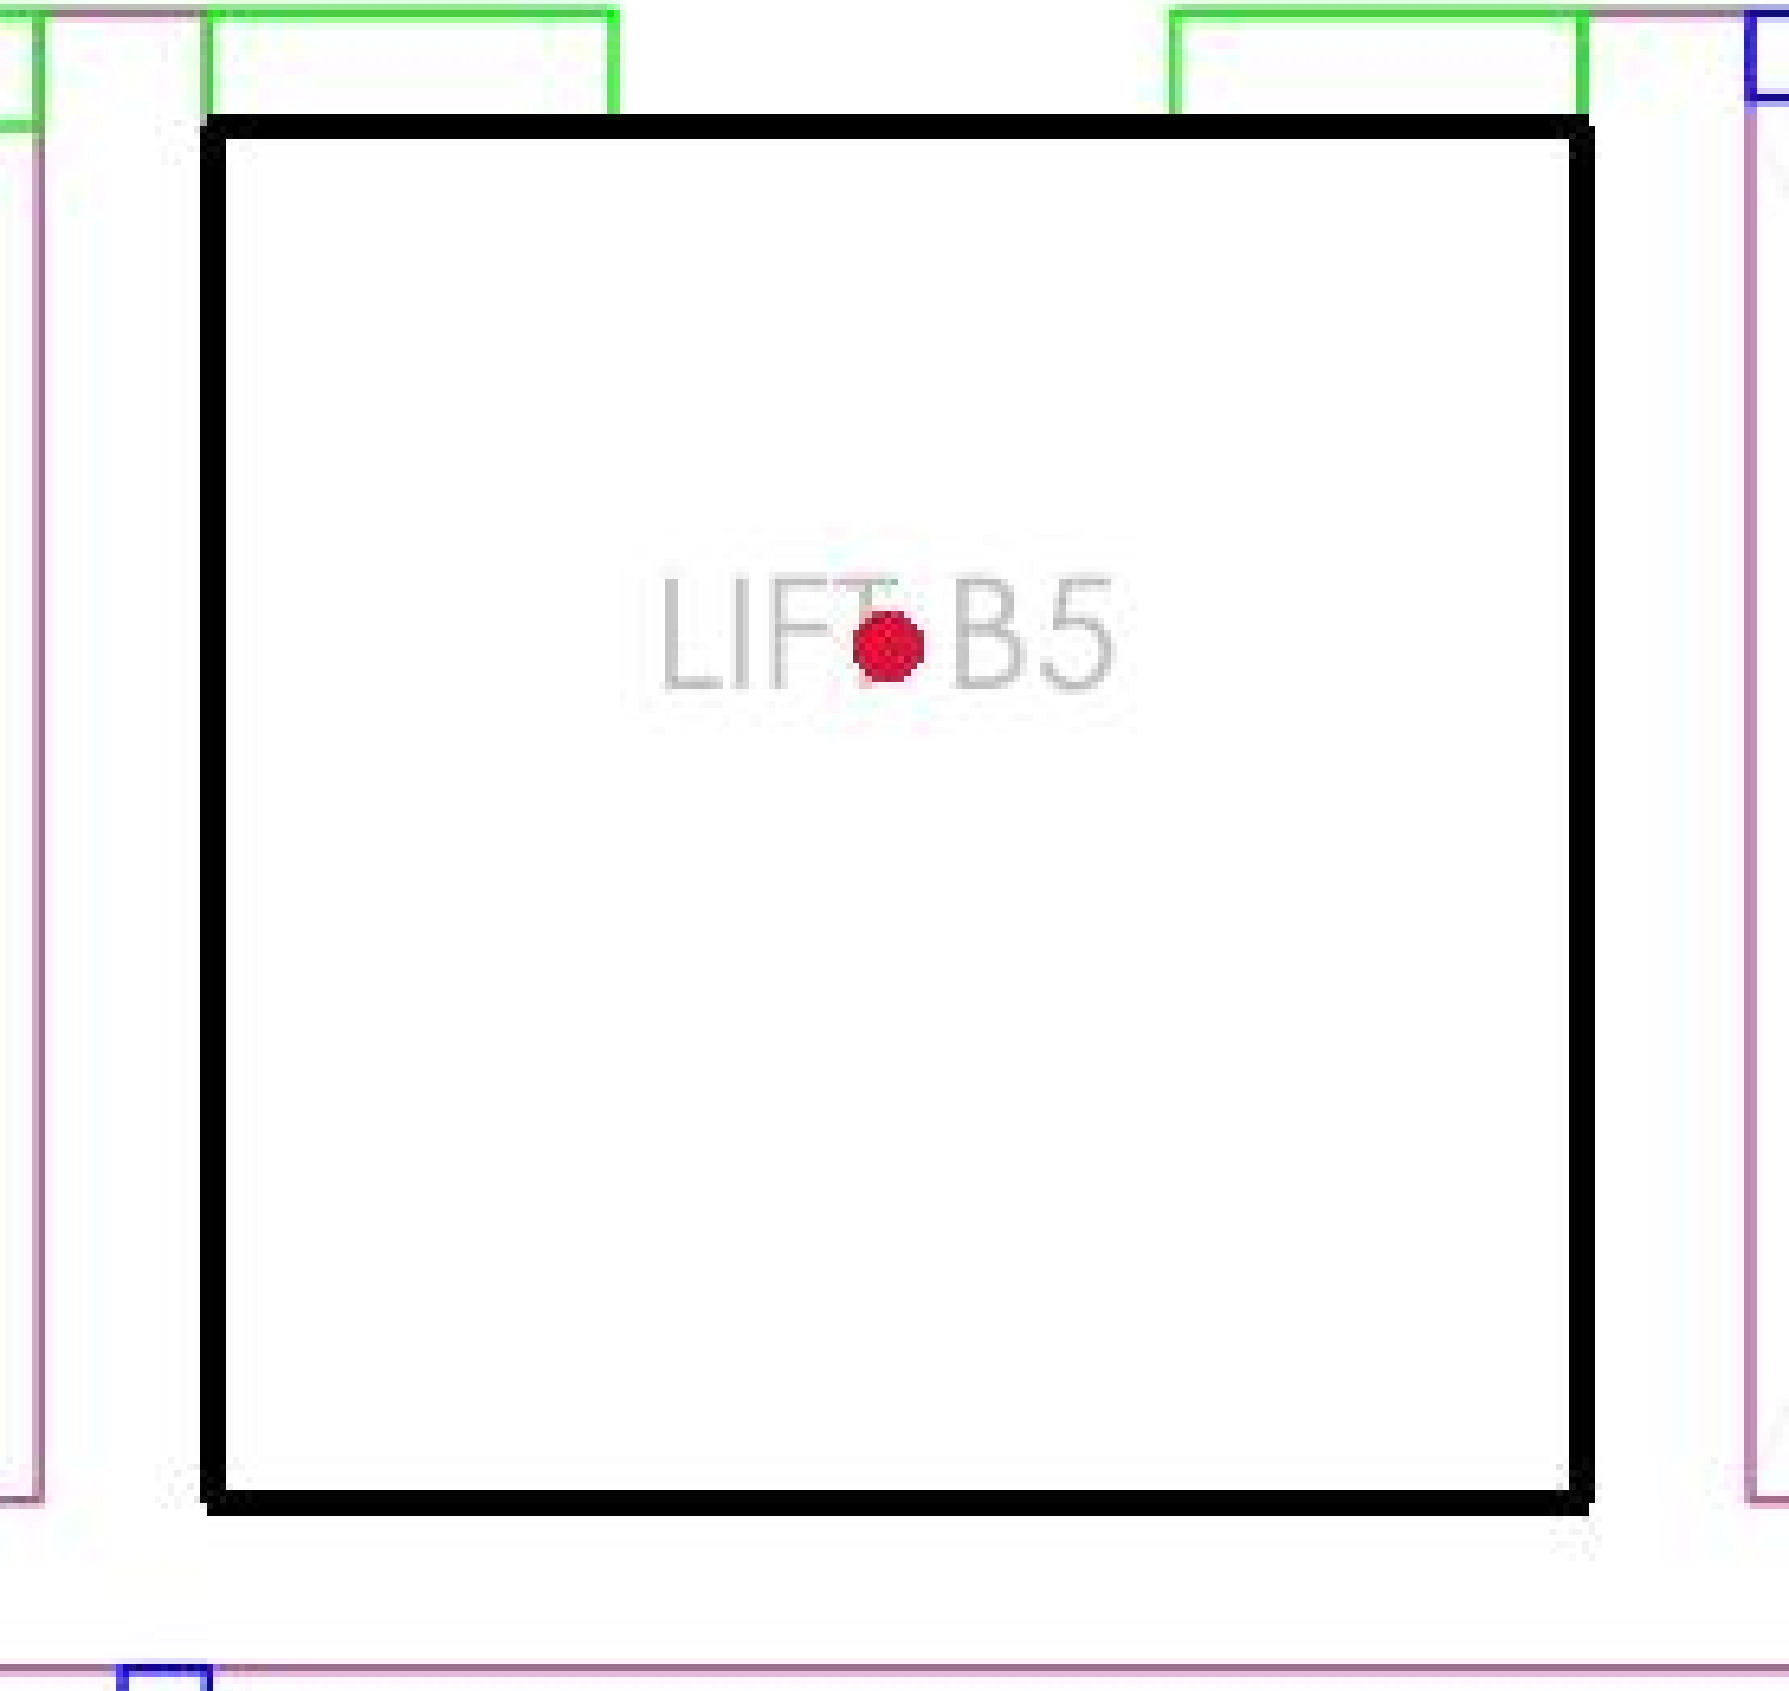

LIFT B3 | vector_polygon_exact | 6.03

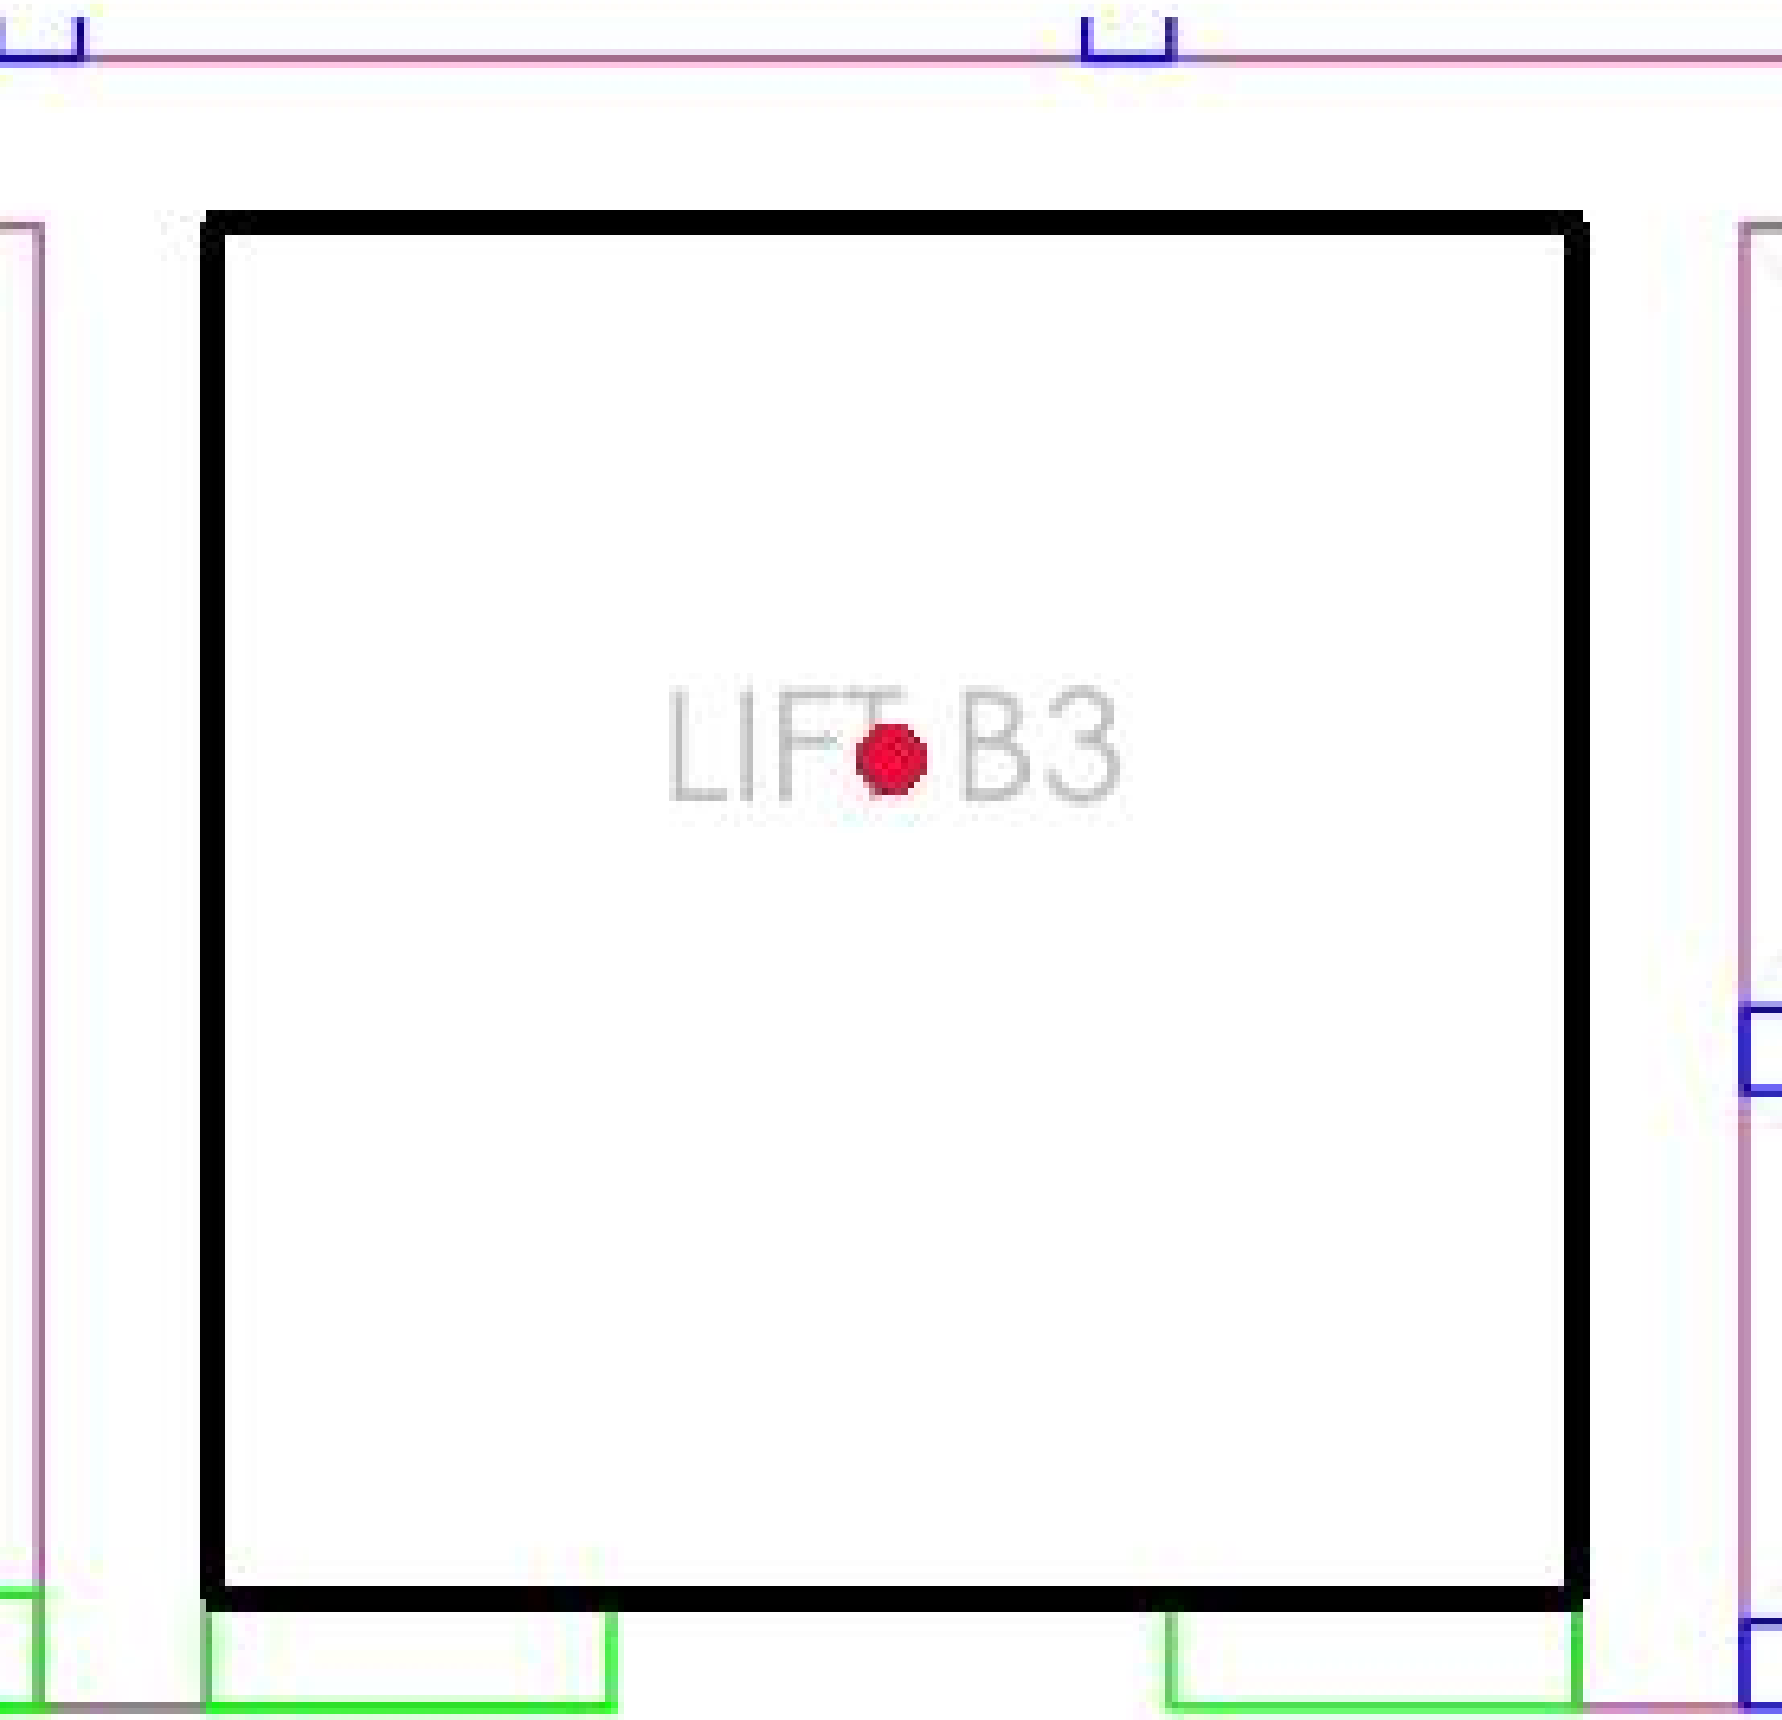

A.H.U | vector_polygon_closed_gap | 15.43

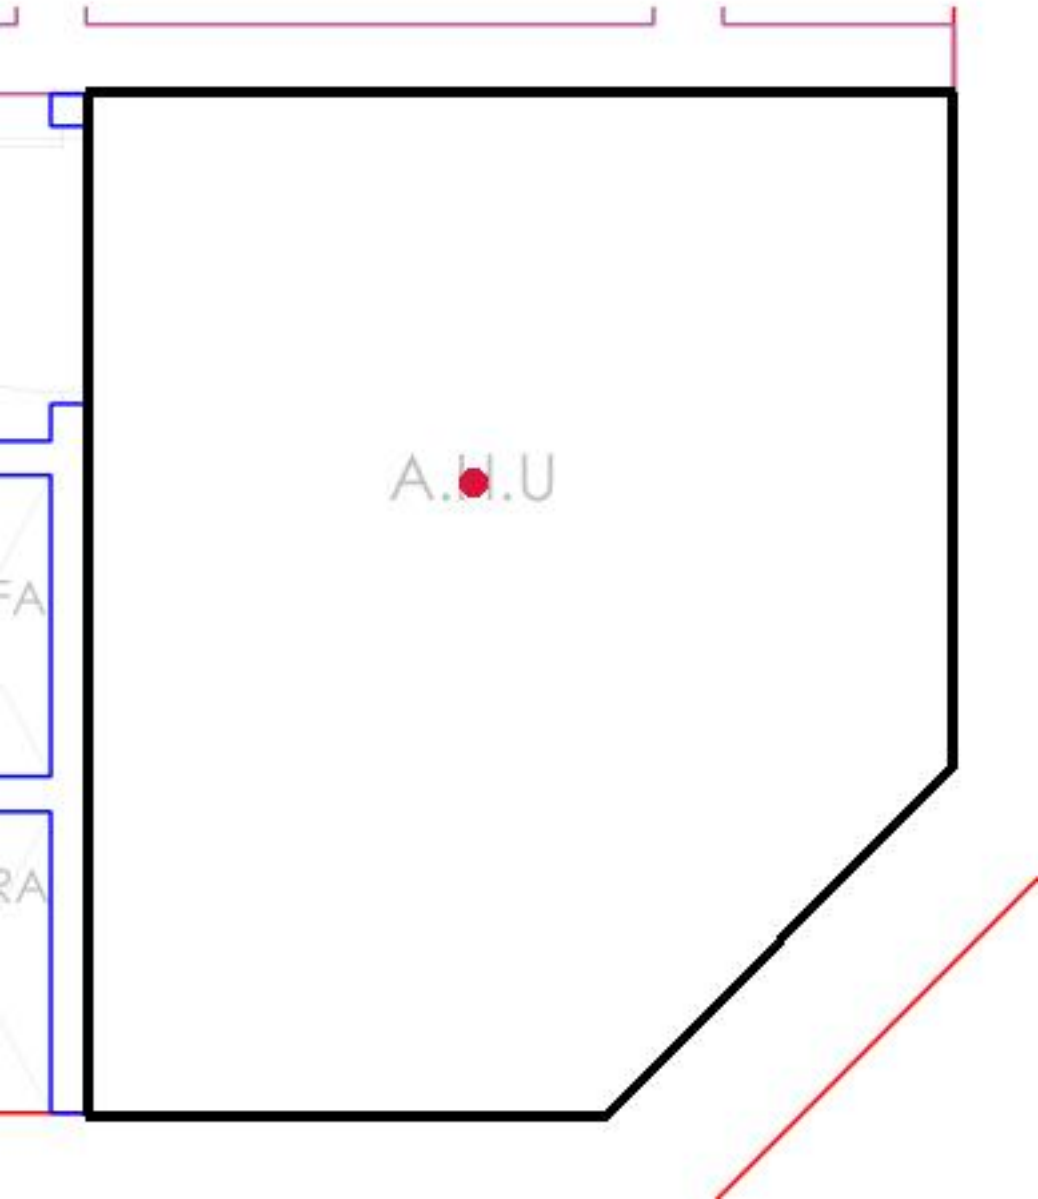

F.TOILET | vector_polygon_closed_gap | 9.08

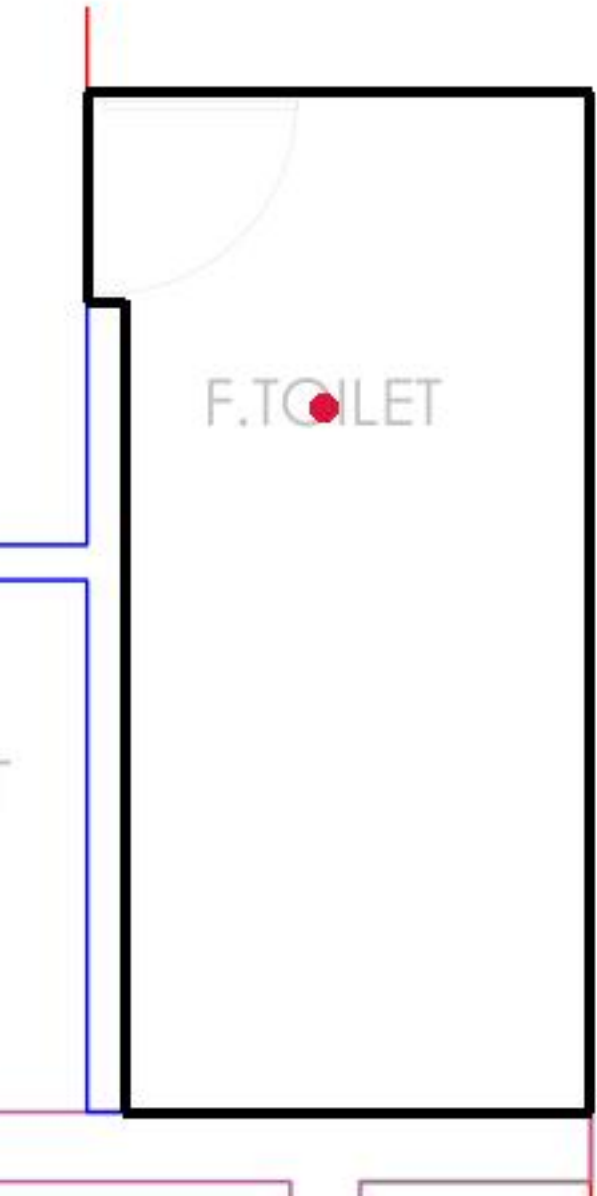

RWS | vector_polygon_exact | 1

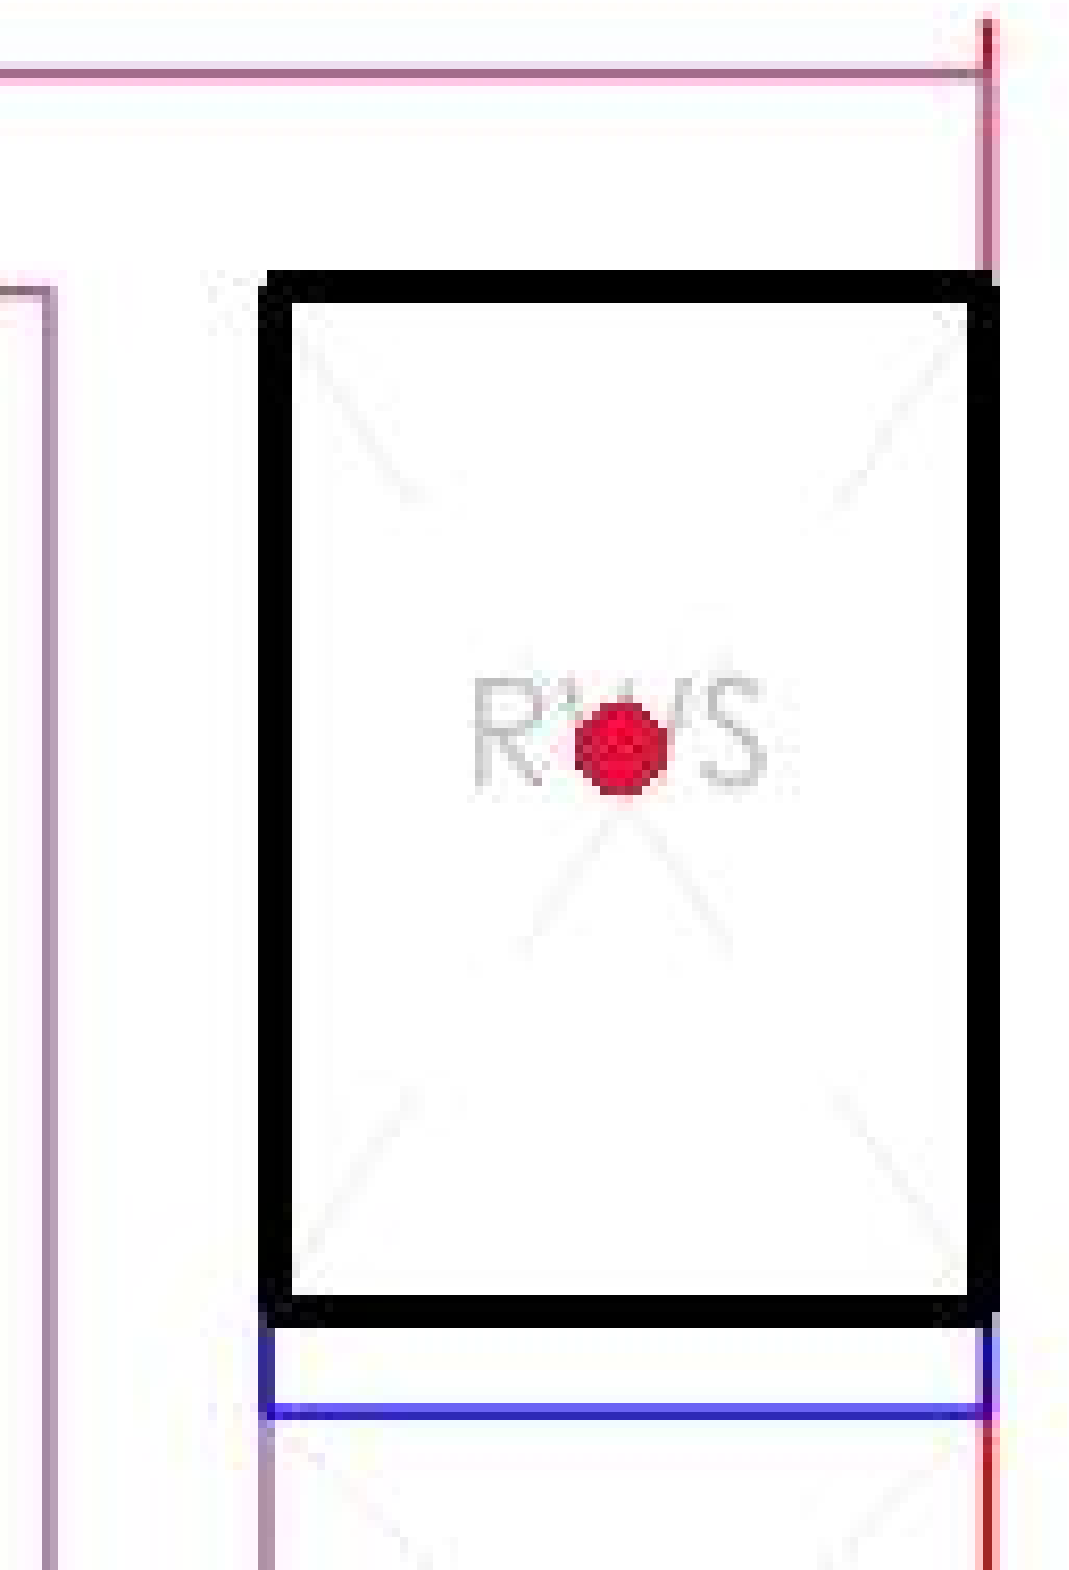

LOBBY. PRESSURIZATION | vec

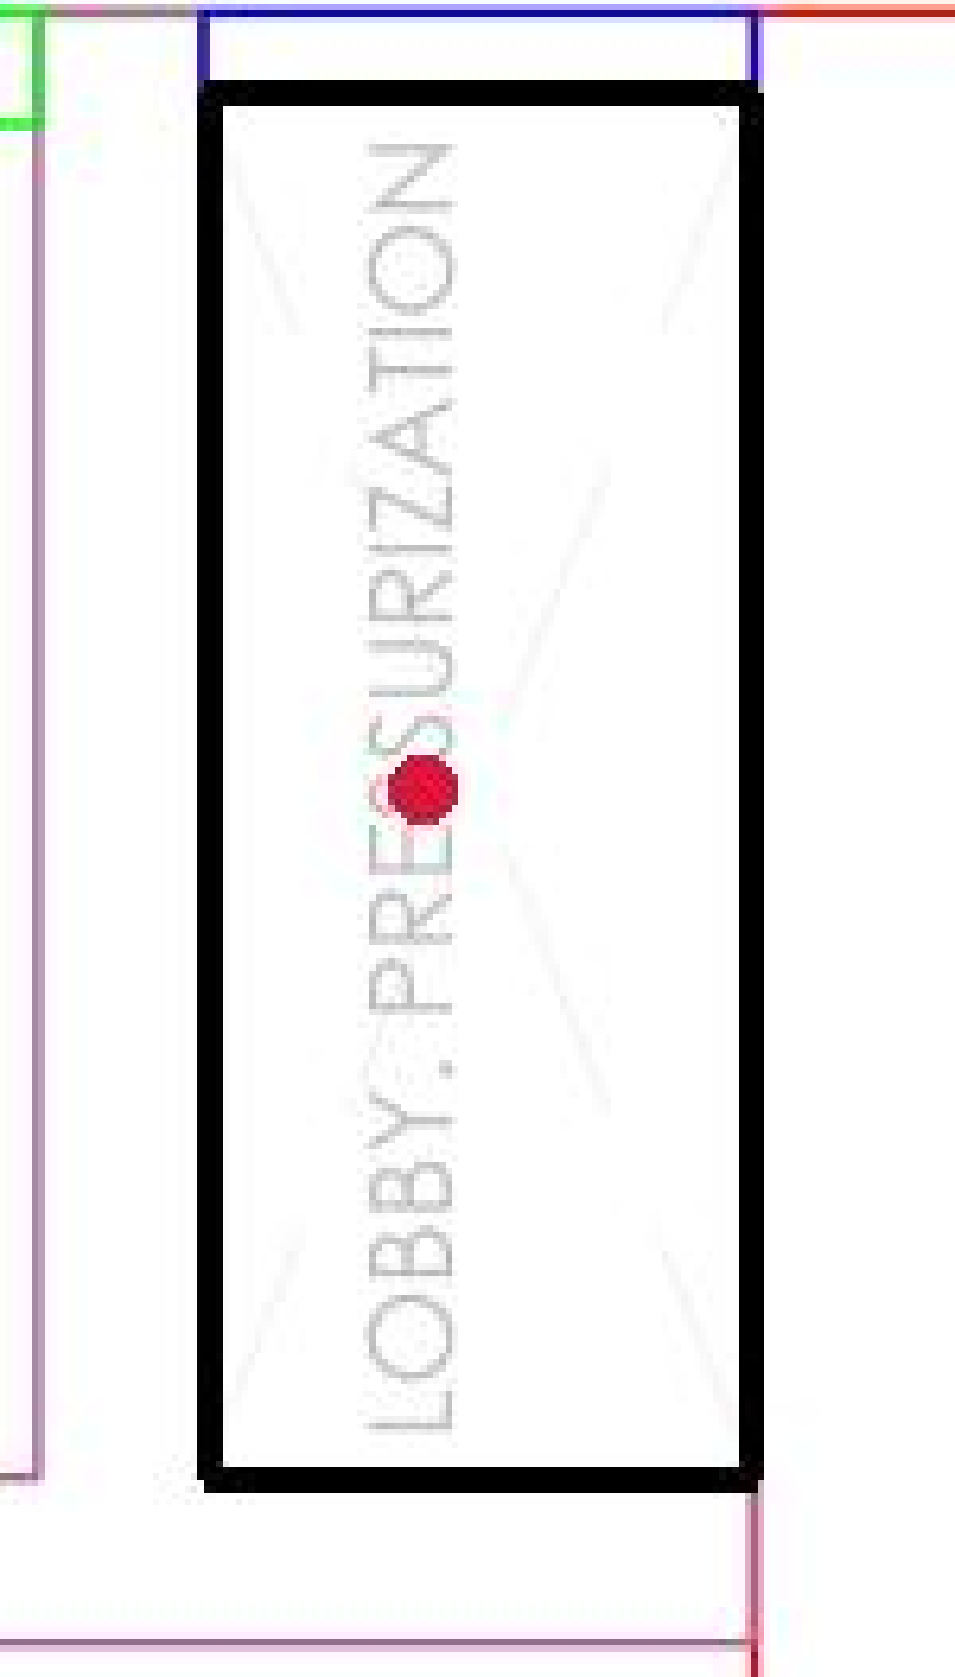
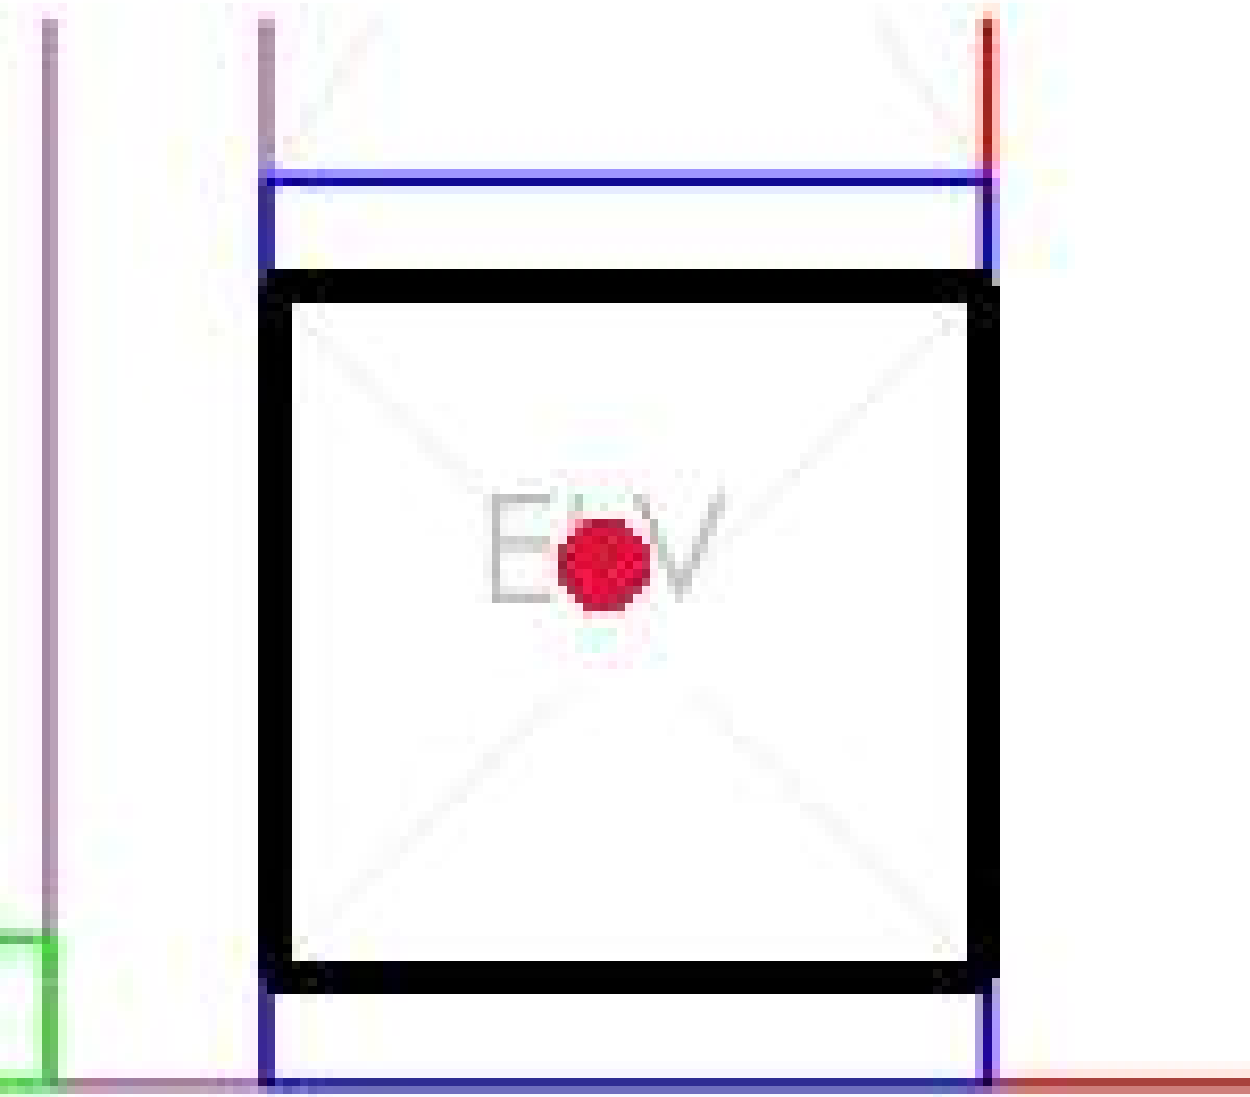
ELV | vector_polygon_exact | 0.5