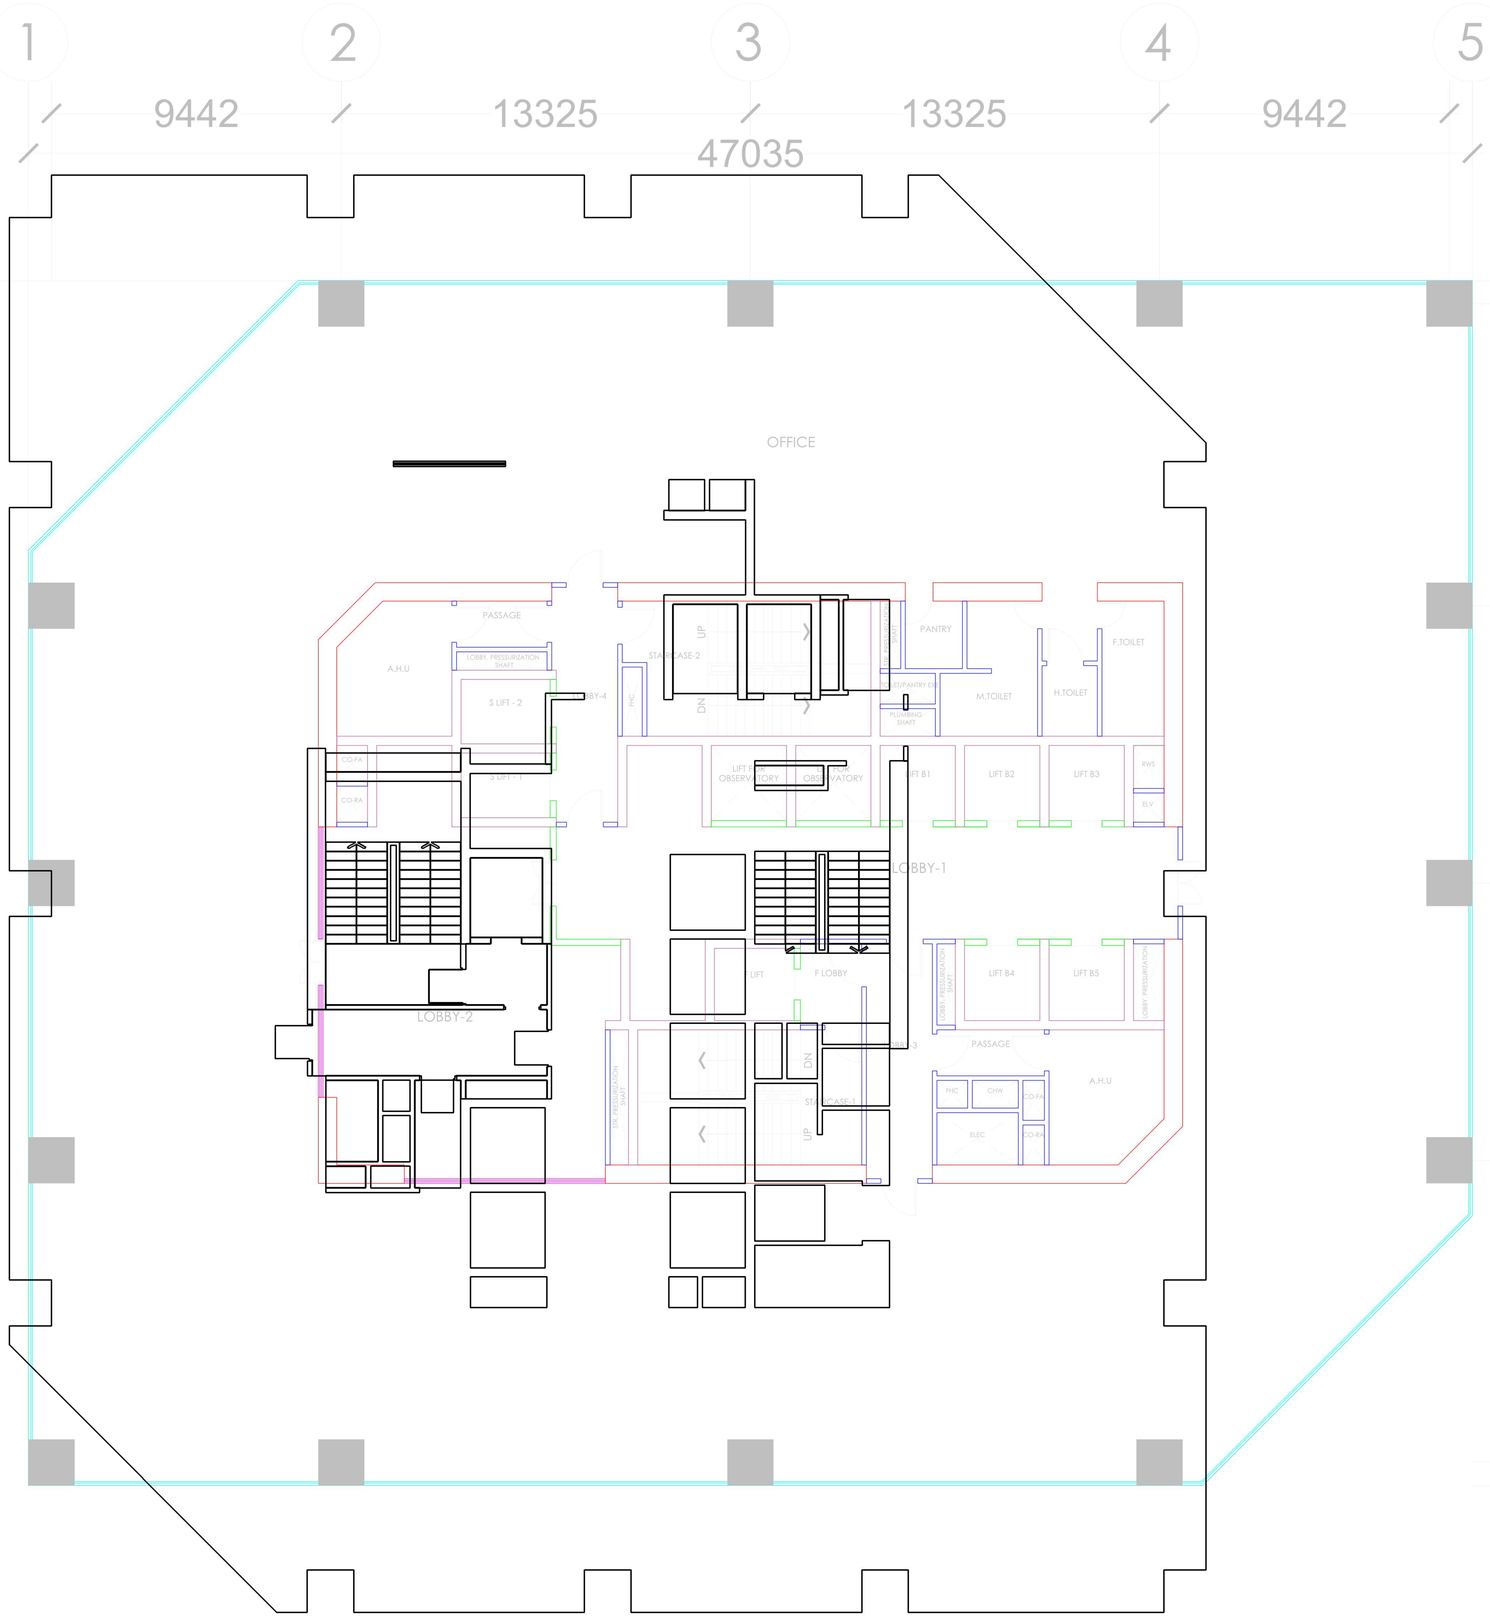

GENERAL NOTES :-

THIS DRAWING IS THE COPYRIGHT OF Architect Hafeez Contractor
29, Bank Street, Mumbai 400 023
Tel. 91-2661920.

IT IS NOT ALLOWED TO COPY OR REPRODUCE ITS CONTENTS IN ANY FORM EXCEPT FOR THE PURPOSE WHICH IT IS INTENDED WITHOUT THE ABOVE CONSULTANT'S AUTHORITY.

DO NOT SCALE THIS DRAWING, ONLY STATED DIMENSIONS ARE TO BE CONSIDERED.

CONTRACTOR TO VERIFY THE DETAIL / INFORMATION GIVEN IN THIS DRAWING, ANY DISCREPANCIES SHALL BE BROUGHT TO ENGINEERS ATTENTION PRIOR TO COMMENCEMENT OF WORK, FAILURE TO COMPLY WITH THE ABOVE WILL BE CONTRACTORS LIABILITY.

ARCH-RCC WALL-1

ARCH-RCC WALL-2

ARCH-BRICK WALL-1

ARCH-BRICK WALL-2

ARCH-COLUMN

INTERNAL GLASS WINDOW

EXTERNAL GLASS WINDOW

KEY PLAN

NOTE :-

Rev.	Date	Description.

PURPOSE OF ISSUE

PROJECT NAME

CONSTRUCTION OF JNPA OFFICE COMPLEX AT MALLET BUNDER, MUMBAI

CLIENT

JAWAHARLAL NEHRU PORT AUTHORITY

PROJECT MANAGEMENT CONSULTANT

ENGINEERS INDIA LIMITED

R&D COMPLEX, NATIONAL HIGHWAY 8 CHANDER NAGAR, SECTOR 16, GURUGRAM, HARYANA 122001

ARCHITECTURAL CONSULTANT

PLANOSCAPES
ARCHITECTS&PLANNERSPVT.LTD.
811, 6th Floor, The Gateway Commercial Building at Atmosphere, Goregeon Mulund Link Road,Near Runwal Greens, Mulund West, Mumbai - 400080.
sarvesh@planoscapes.com

STRUCTURAL CONSULTANT

MAHIMTURA CONSULTANTS PVT. LTD
ADDRESS - 3RD FLOOR, UNIQUE HOUSE, 25, SYED ABDULLAH BRELVI MARG, KALA GHODA FORT, MUMBAI - 400001
EMAIL - BELAPUR@MAHIMTURA.NET, DHRUVA22MAHIMTURA@GMAIL.COM

SERVICES CONSULTANT

TECHFOUR ENGINEERING SOLUTIONS PVT. LTD -MEPF
ADDRESS - A-16, 1ST FLOOR, MOHAN COOPERATIVE, INDUSTRIAL ESTATES, NEW DELHI - 110044
EMAIL - PUNEIT@TECHFOURSOLUTIONS.COM, BPSAMRAT@TECHFOURSOLUTIONS.COM

LANDSCAPE CONSULTANT

INTEGRAL DESIGNS INTERNATIONAL STUDIO PVT LTD - LANDSCAPE
ADDRESS - E-90, ANAND NIKETAN, NEW DELHI - 110021
EMAIL - DESIGNSINTEGRAL@GMAIL.COM, ACCOUNTS@INTEGRALDESIGNS.IN

DRAWING TITLE

36th FLOOR - DG SHIPPING ARCH LAYOUT

DATE	SHT. SIZE	SCALE
11.02.2026	A1	1:100

DRAWN	APPROVED
Vijay Patil	Sarvesh Nandgirikar

NORTH	DOCUMENT NUMBER	REVISION
	JNPA-EIL-CDG-ARCH-0041	R0

CO-RA | vector_polygon_exact | 1.1

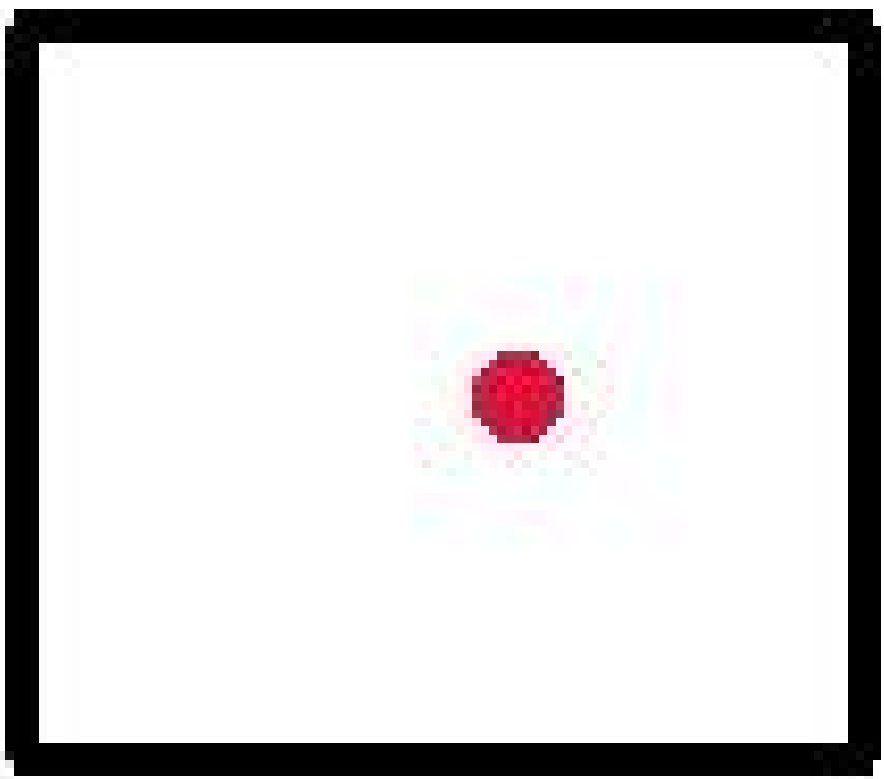

CO-FA | vector_polygon_exact | 1.1

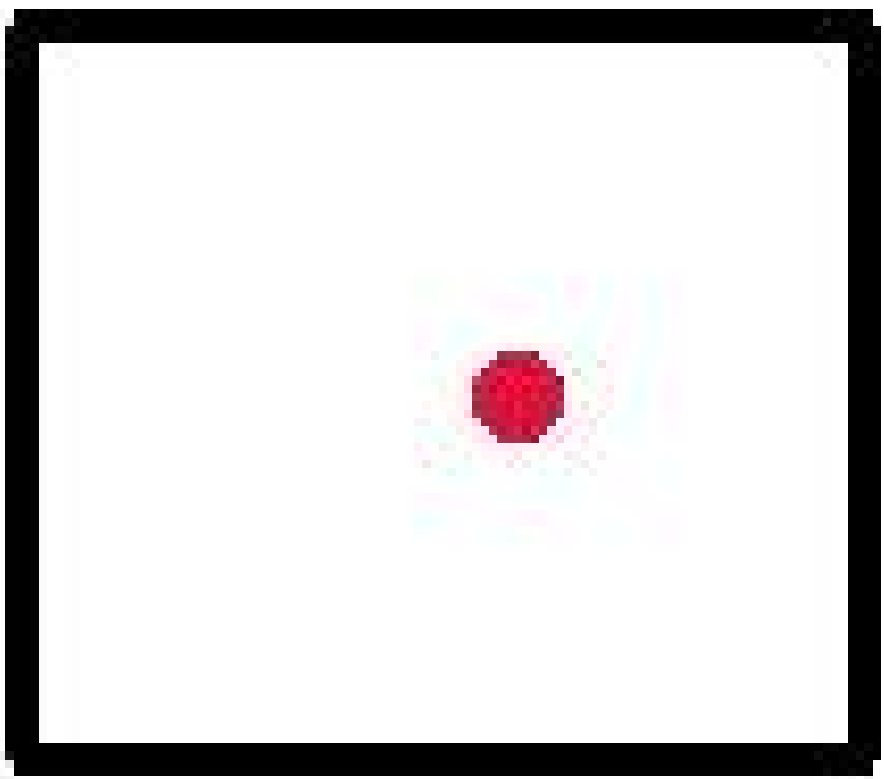

OFFICE

PASSAGE

A.H.U

LOBBY. PRESSURIZATION SHAFT

S LIFT - 2

S LIFT - 1

LOBBY-4

FHC

STAIRCASE-2

UP

DN

STR. PRESSURIZATION SHAFT

PANTRY

TOILET/PANTRY EXE

PLUMBING SHAFT

M.TOILET

H.TOILET

F.TOILET

CO-FA

CO-RA

LIFT FOR OBSERVATORY

LIFT FOR OBSERVATORY

LIFT B1

LIFT B2

LIFT B3

RWS

ELV

LOBBY-1

LOBBY-2

F LIFT

F LOBBY

STR. PRESSURIZATION SHAFT

STAIRCASE-1

DN

UP

LOBBY-3

LOBBY. PRESSURIZATION SHAFT

LIFT B4

LIFT B5

LOBBY. PRESSURIZATION

PASSAGE

A.H.U

FHC

CHW

CO-FA

ELEC

CO-RA

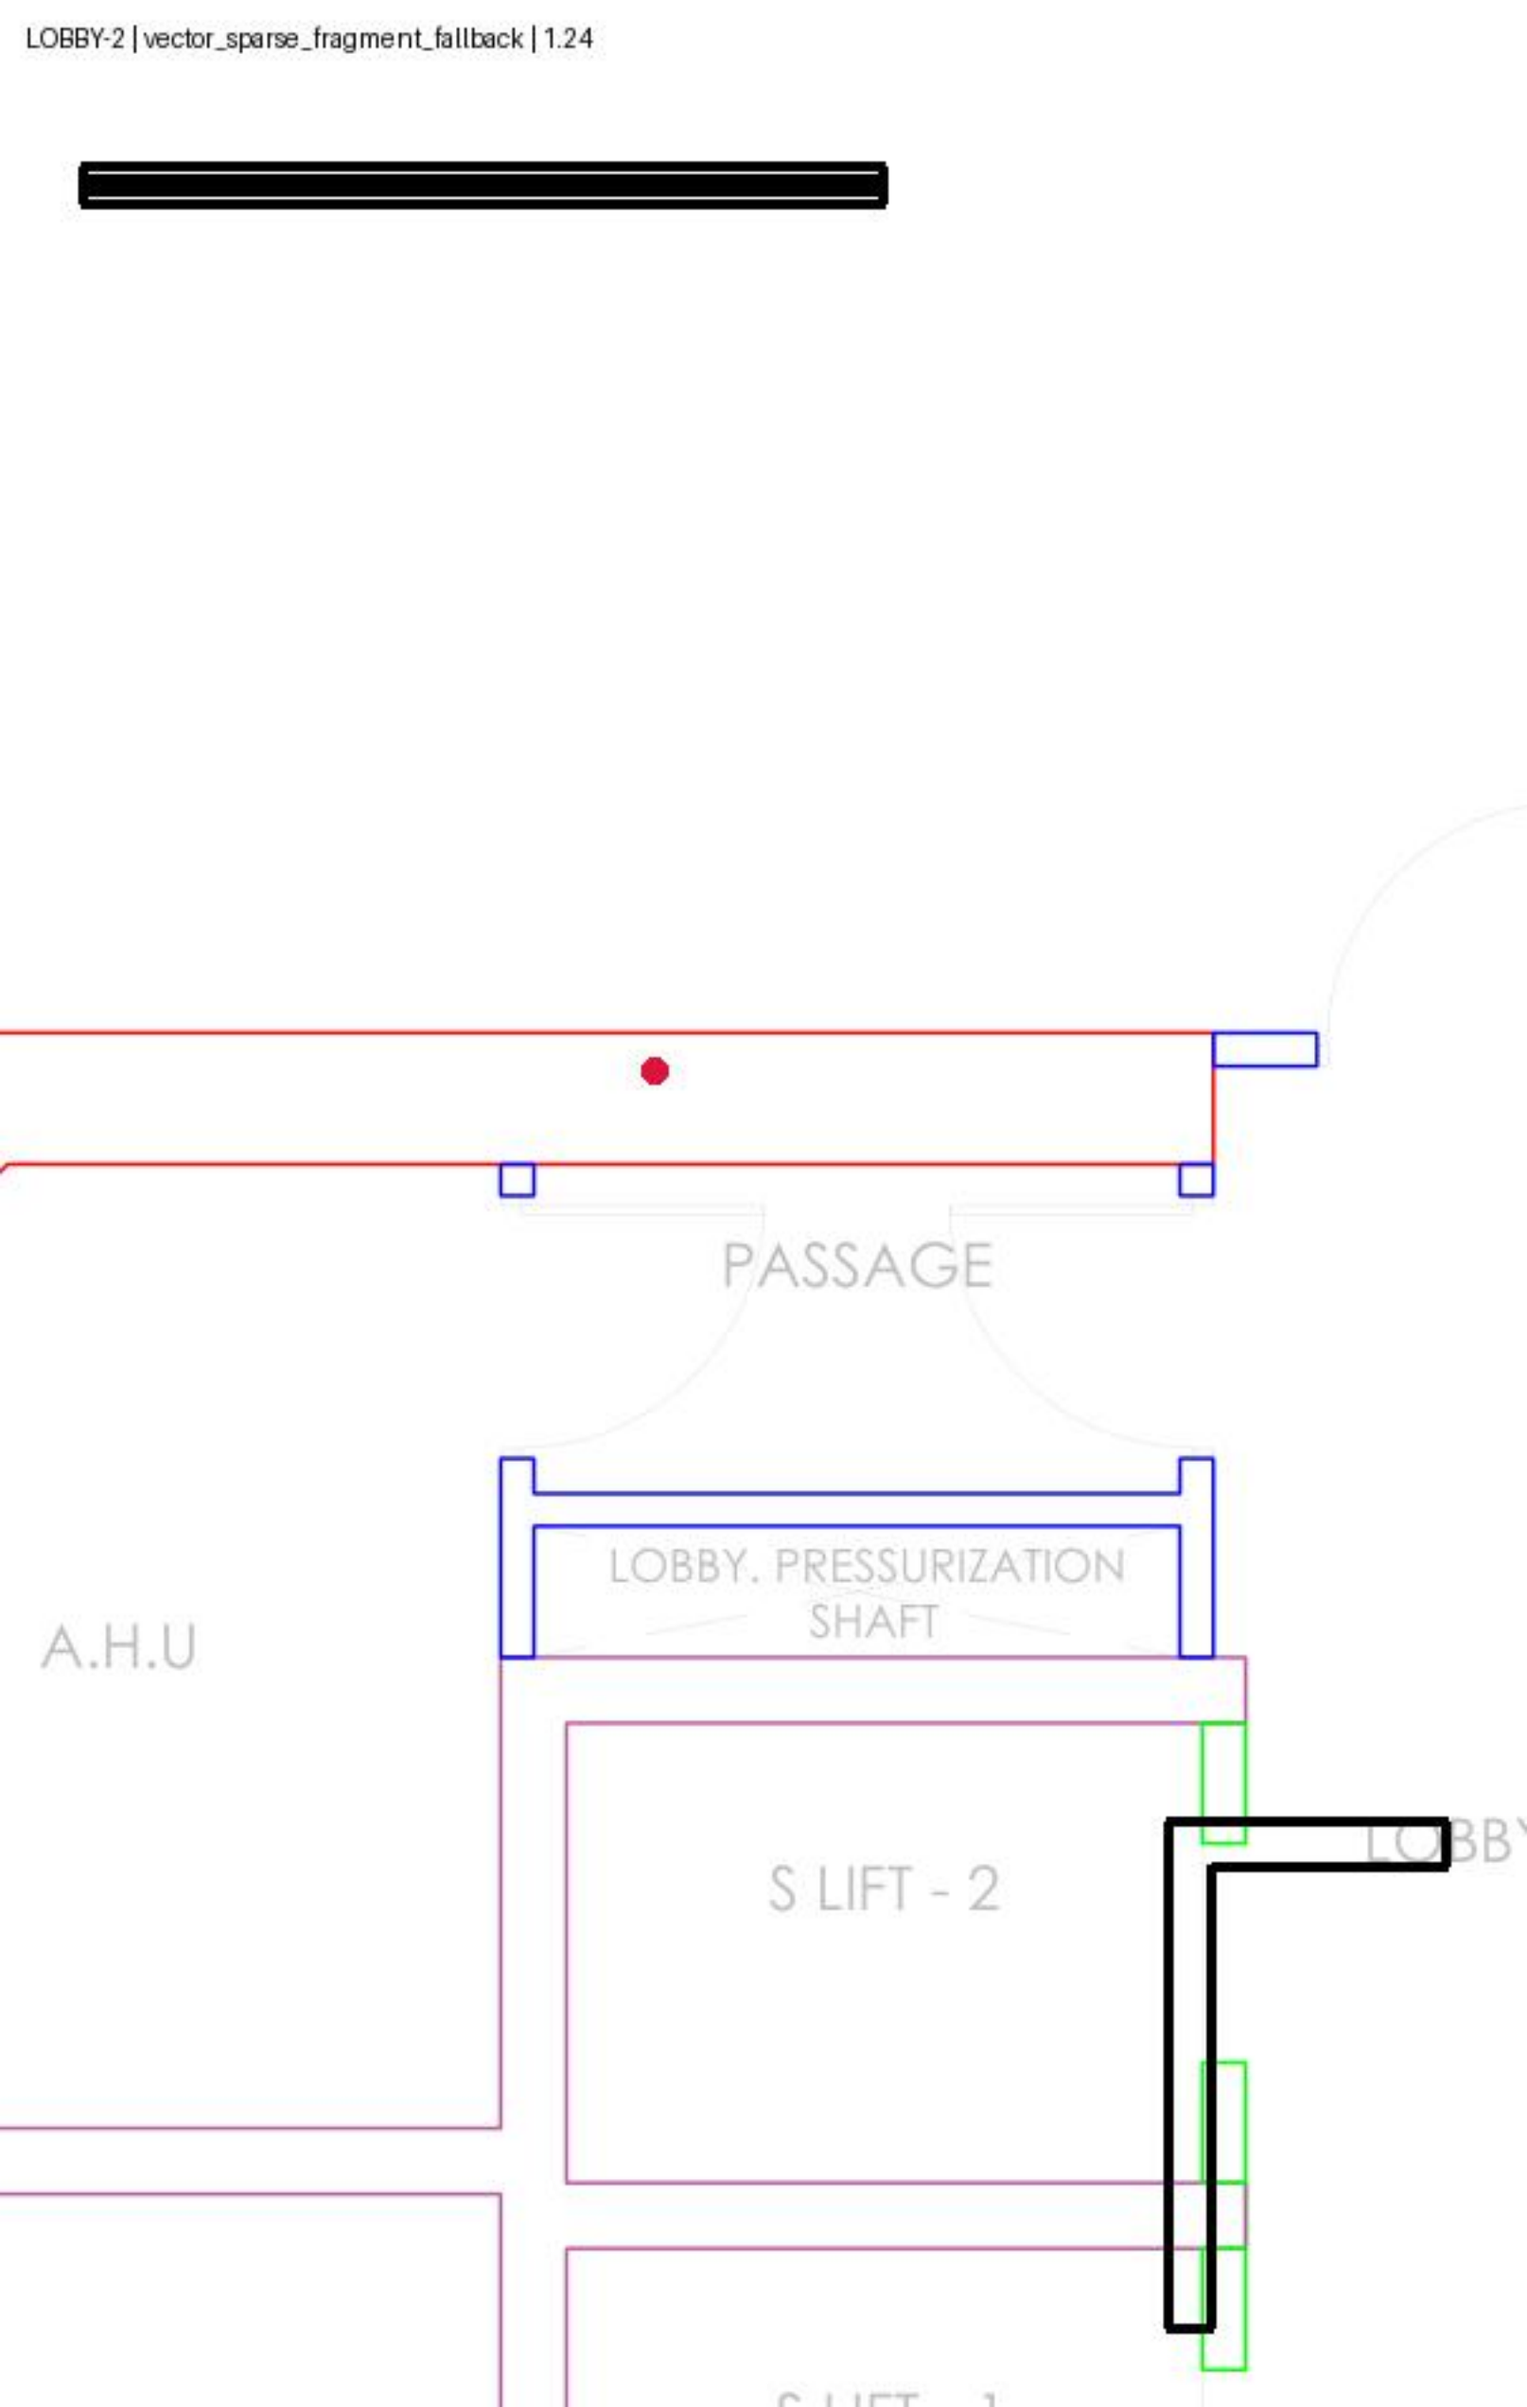
PASSAGE
LOBBY. PRESSURIZATION SHAFT
A.H.U
S LIFT - 2

LOBBY. PRESSURIZATIO

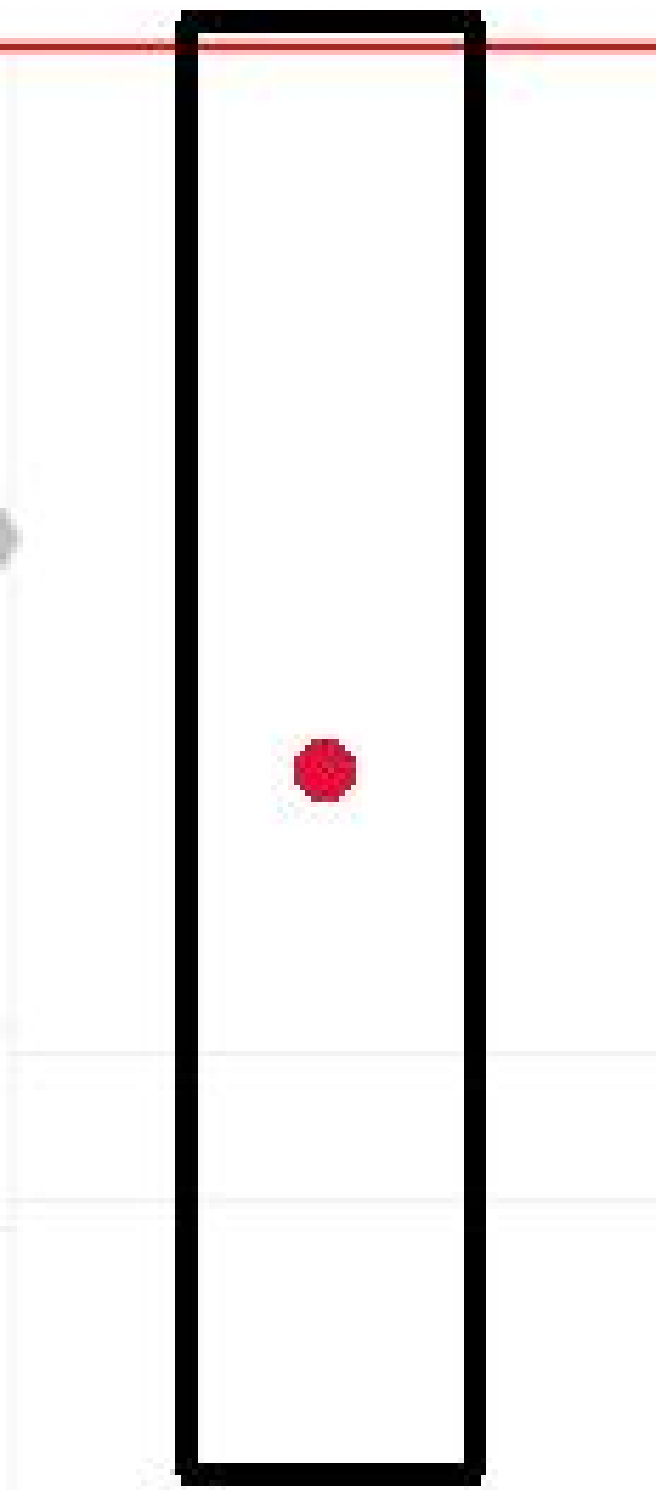

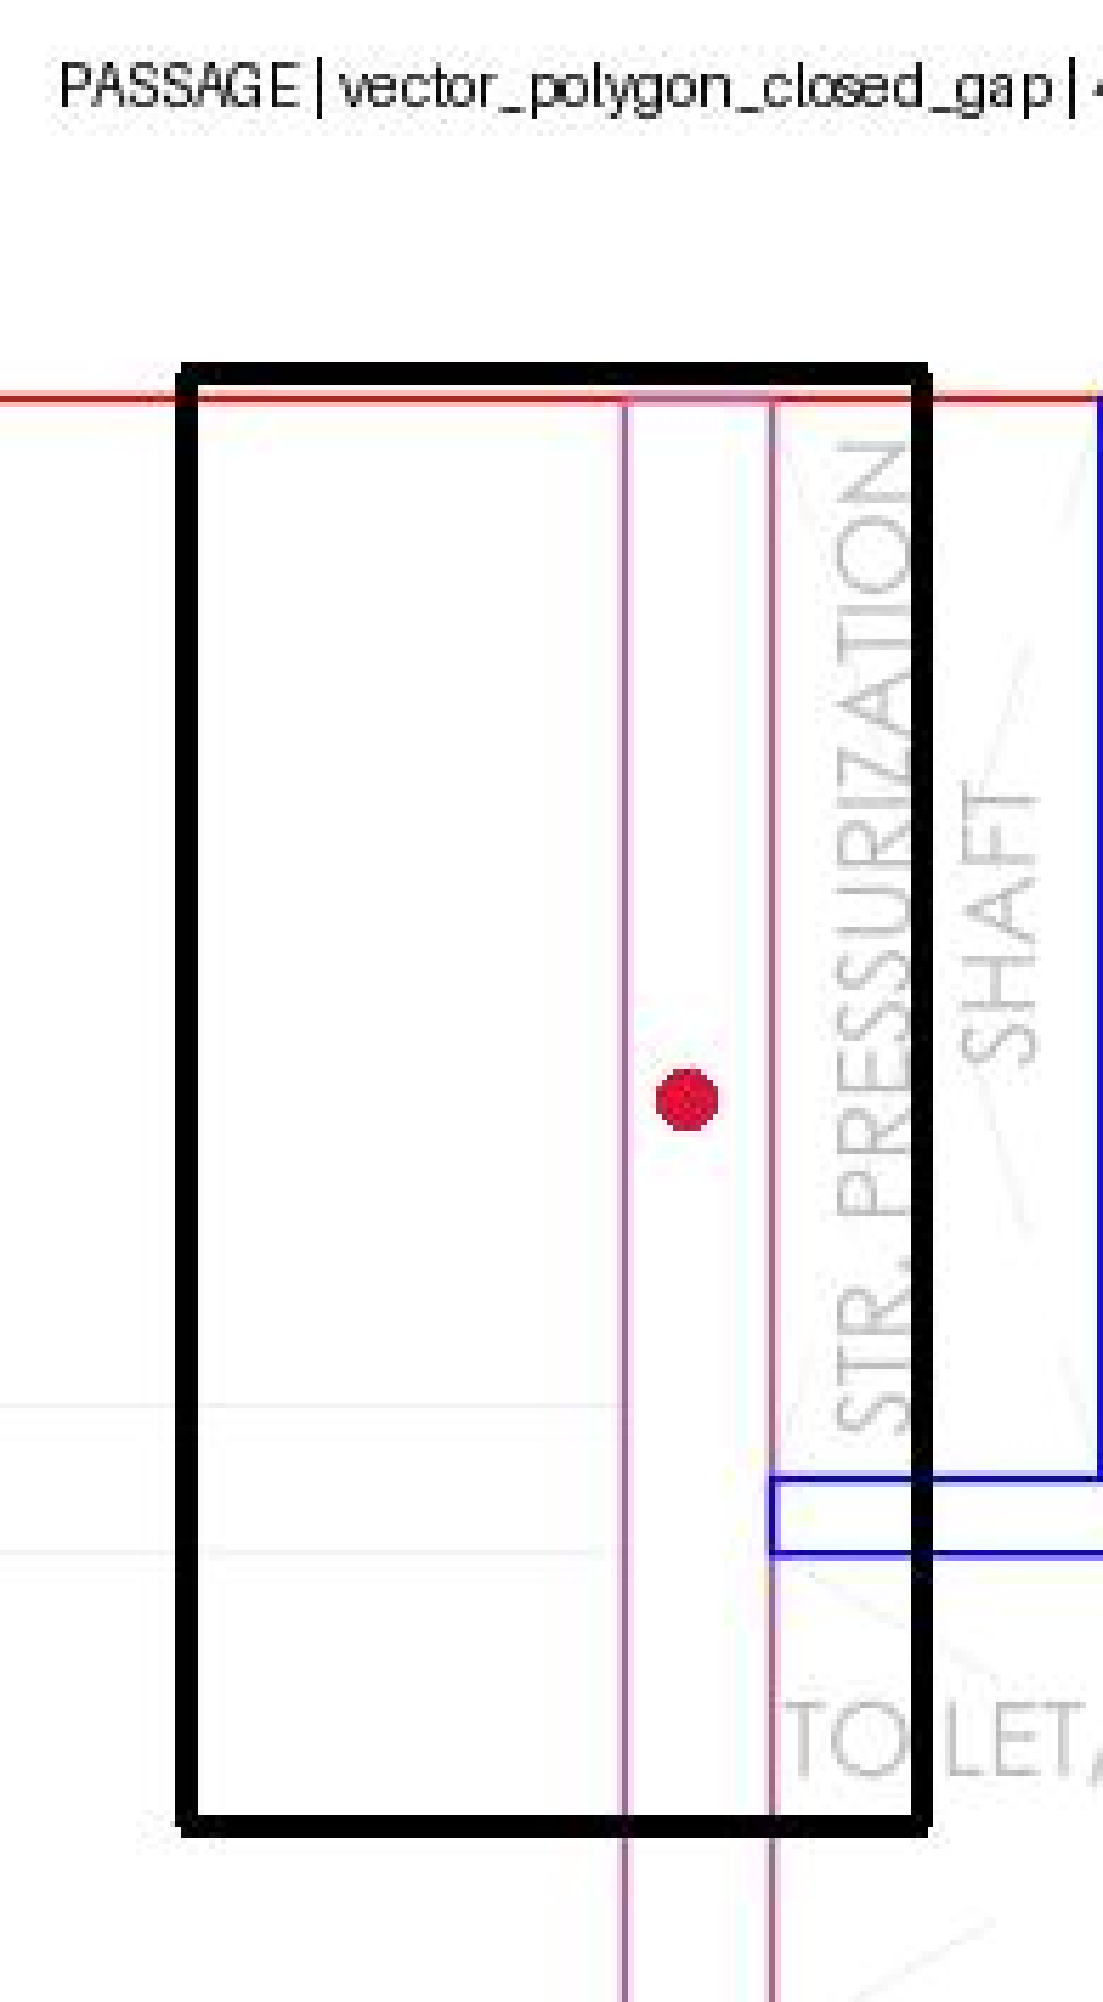
PASSAGE | vector_polygon_closed_gap |
STR. PRESSURIZATION SHAFT
TOILET

S LIFT - 2 | vector_polygon_exact | 6.12

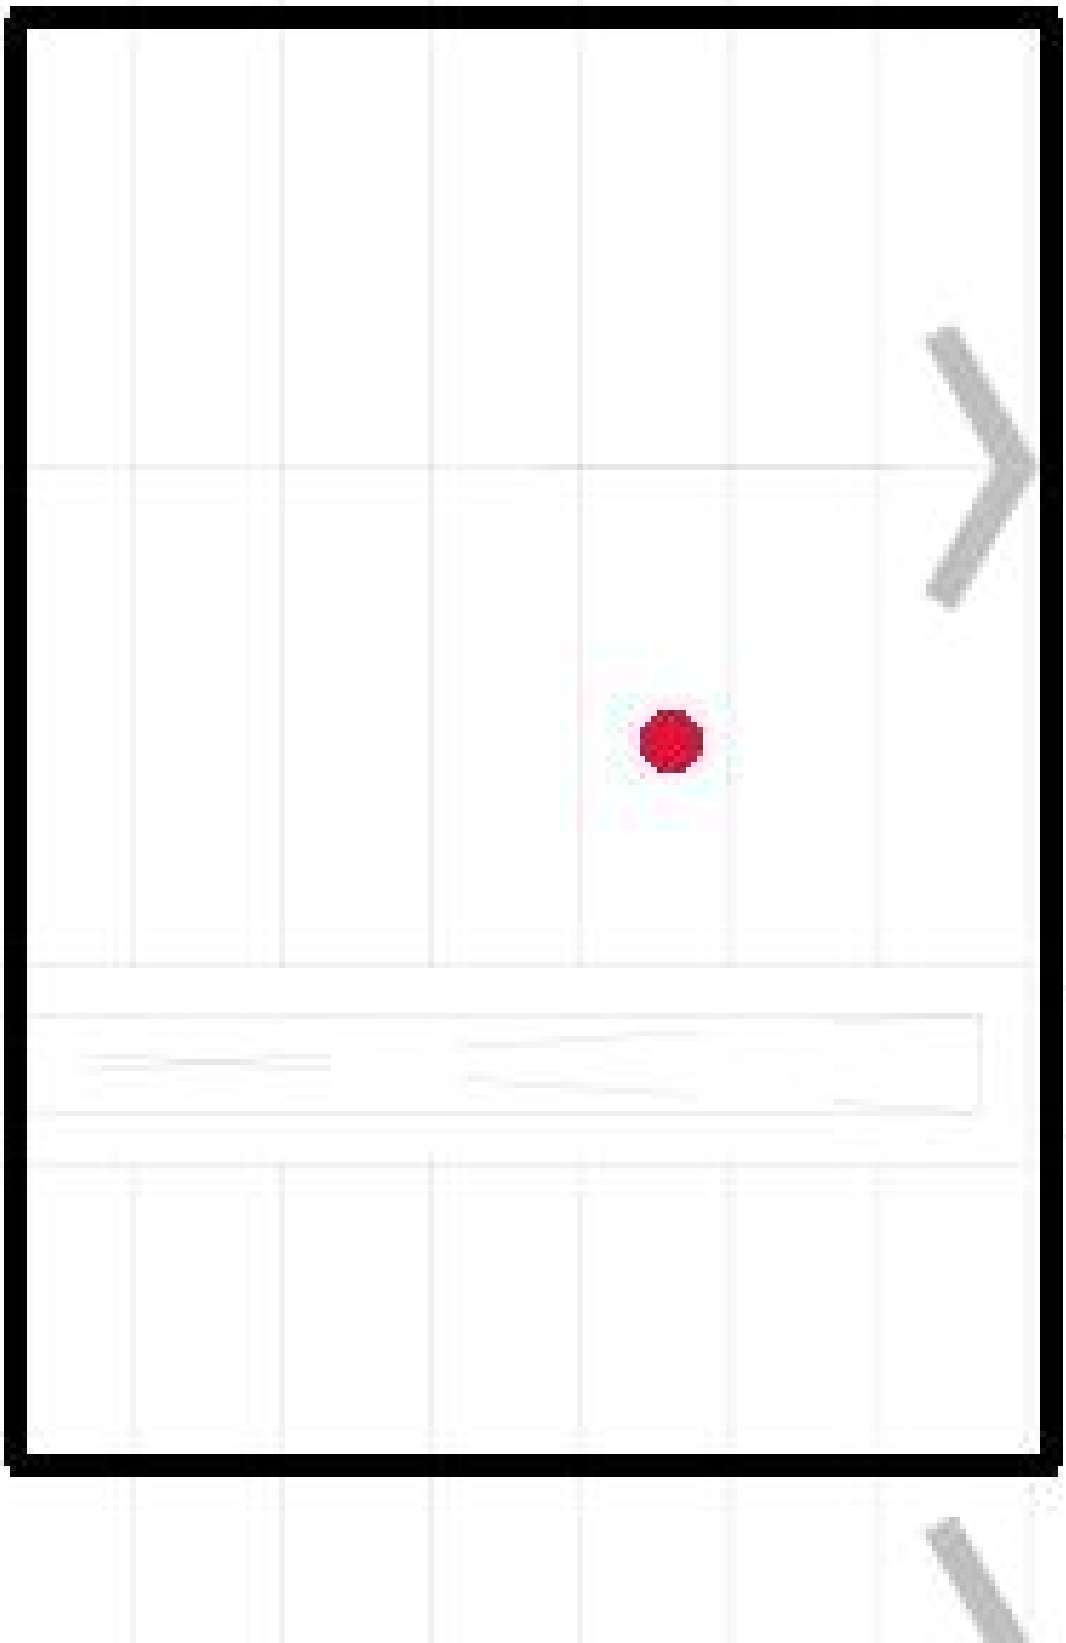

S LIFT - 1 | vector_polygon_exact | 6.13

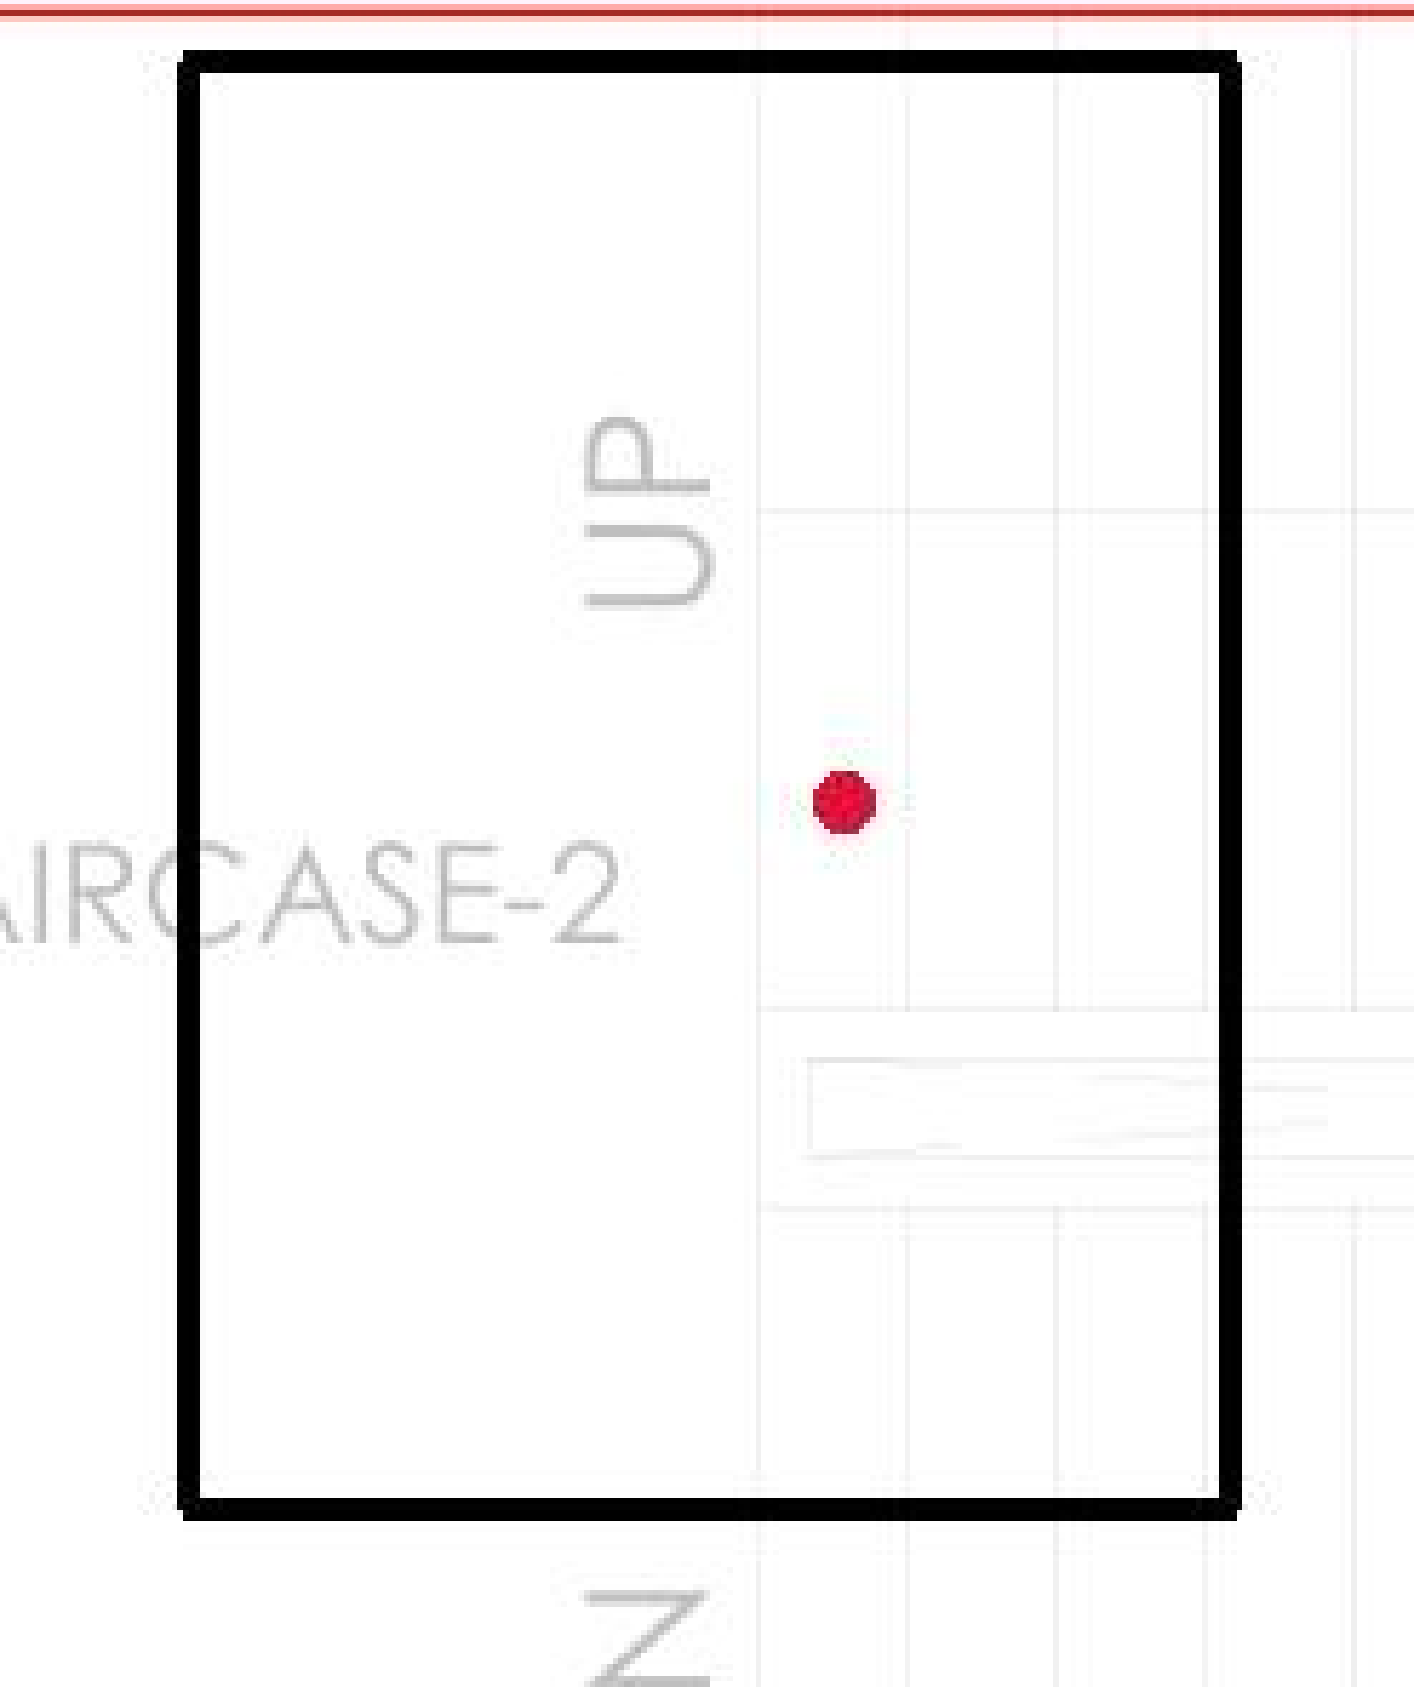

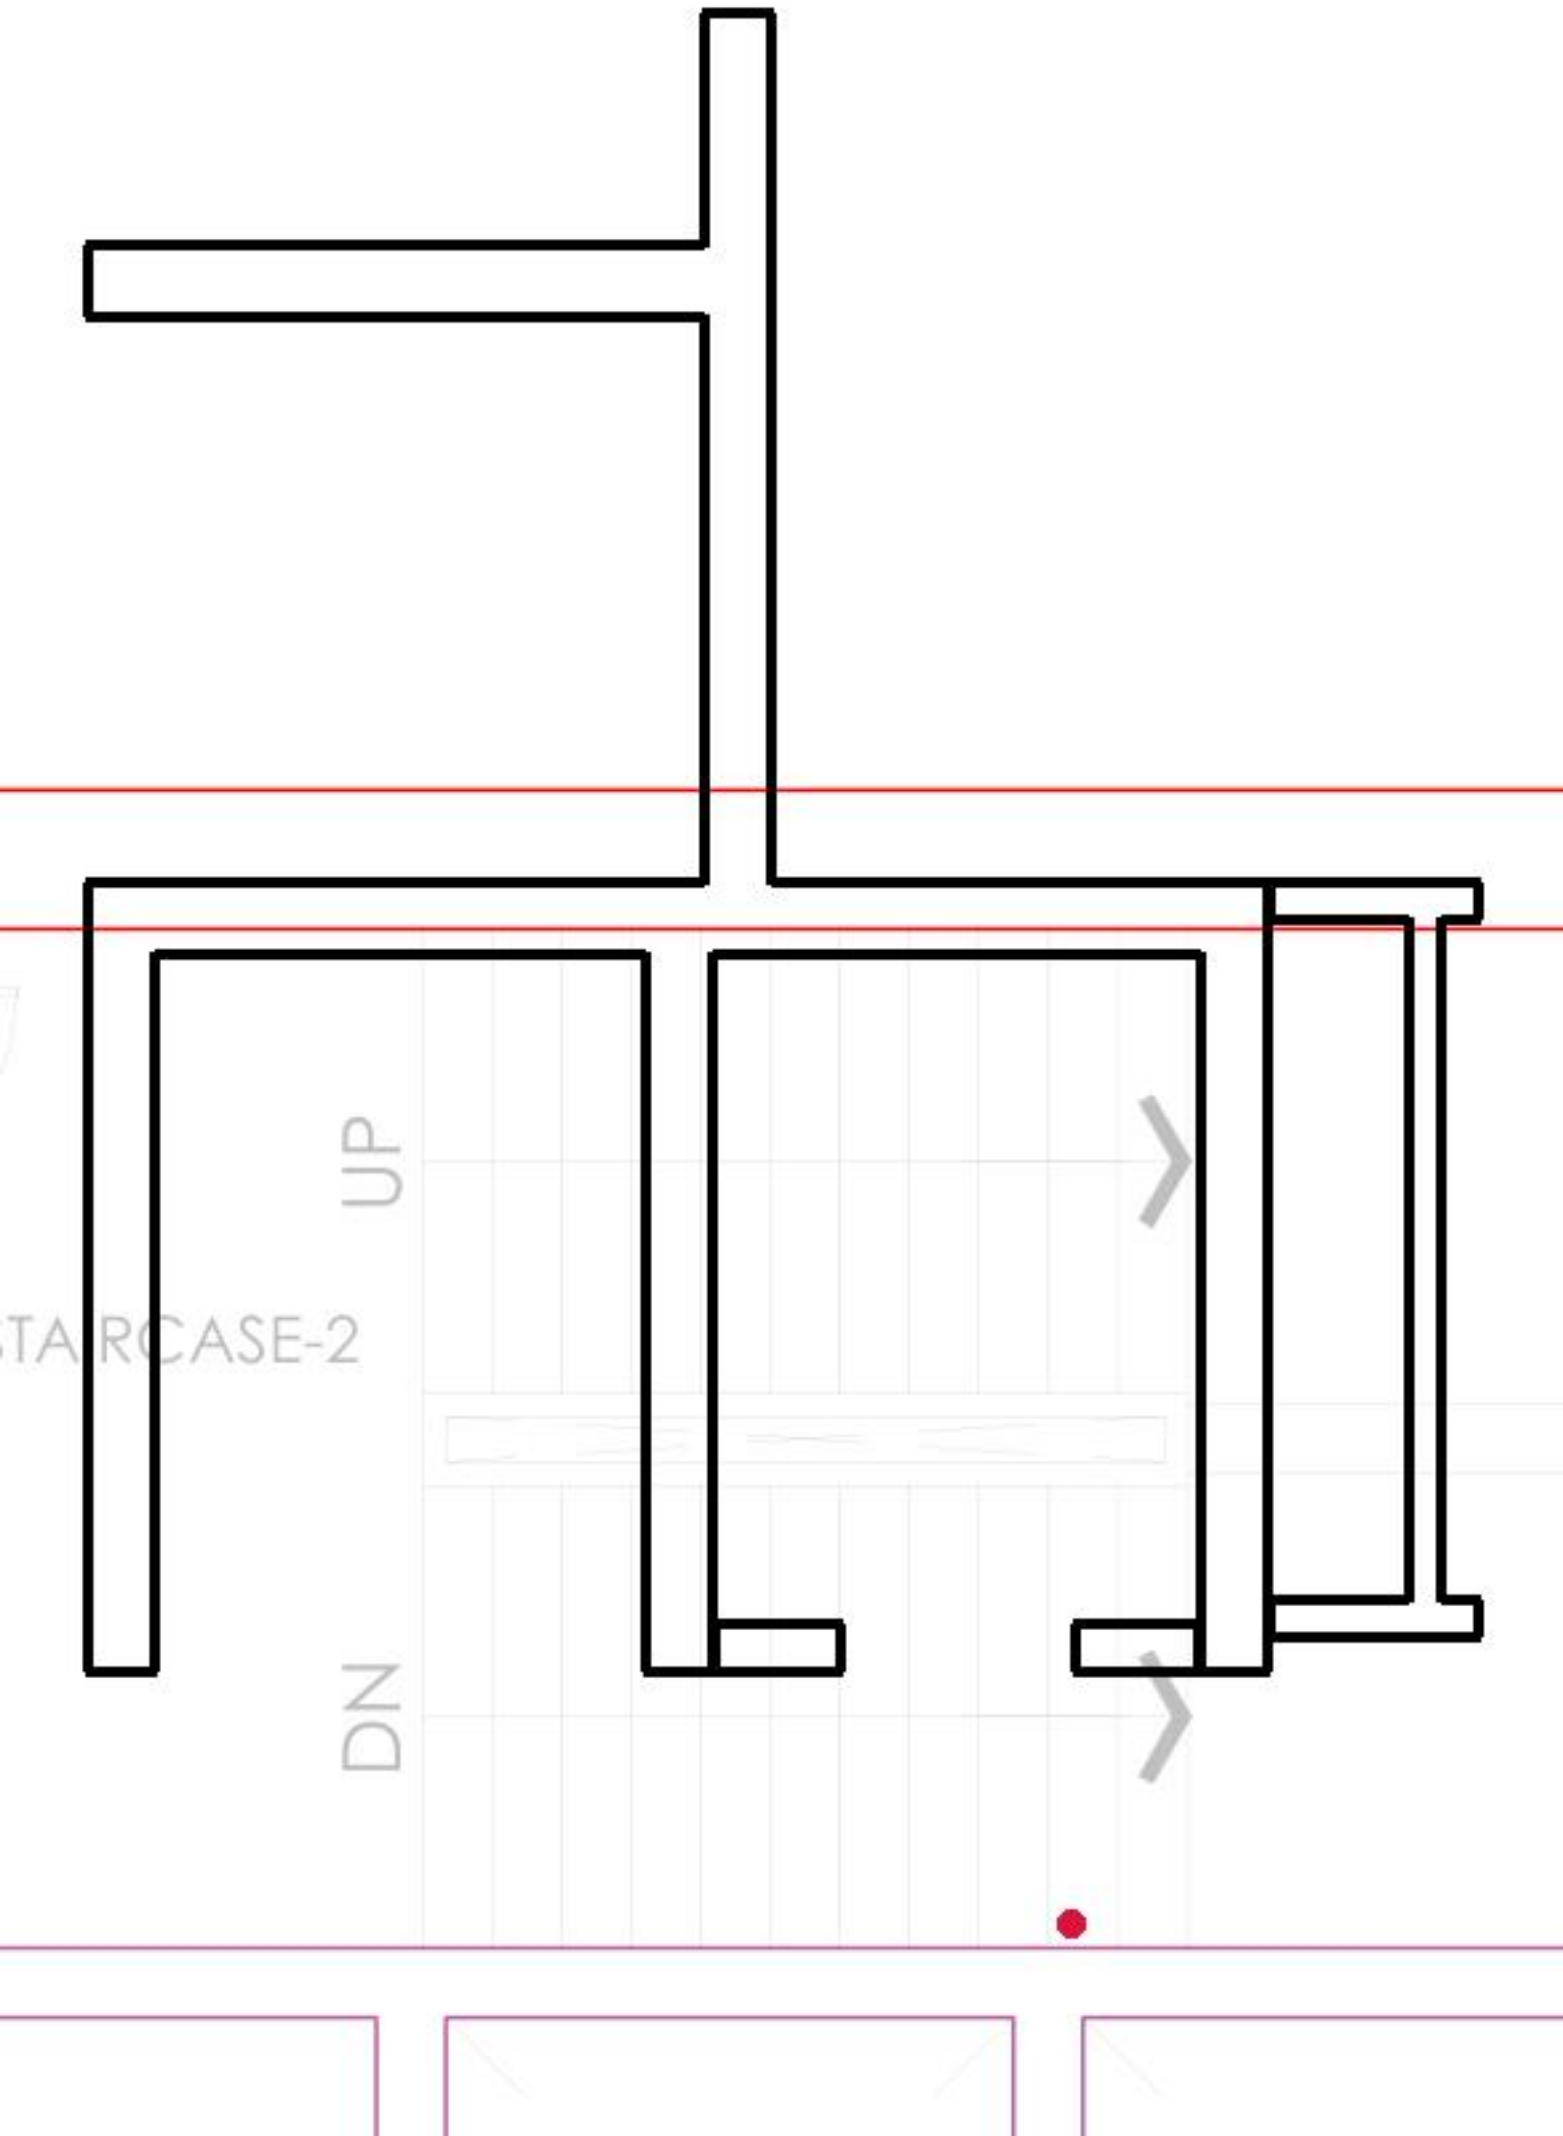
UP
STAIRCASE-2
DN

STR PRESSURIZATION SHAFT | vector_polygon_exact | 2.65

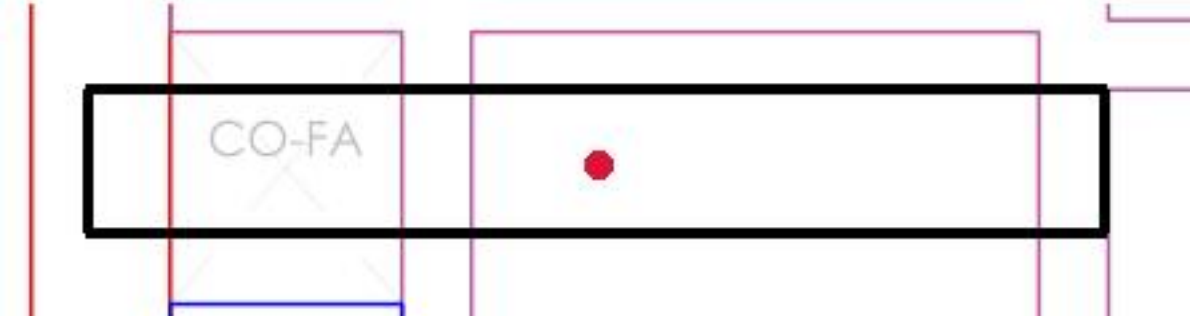

FHC | vector_polygon_exact | 1.47

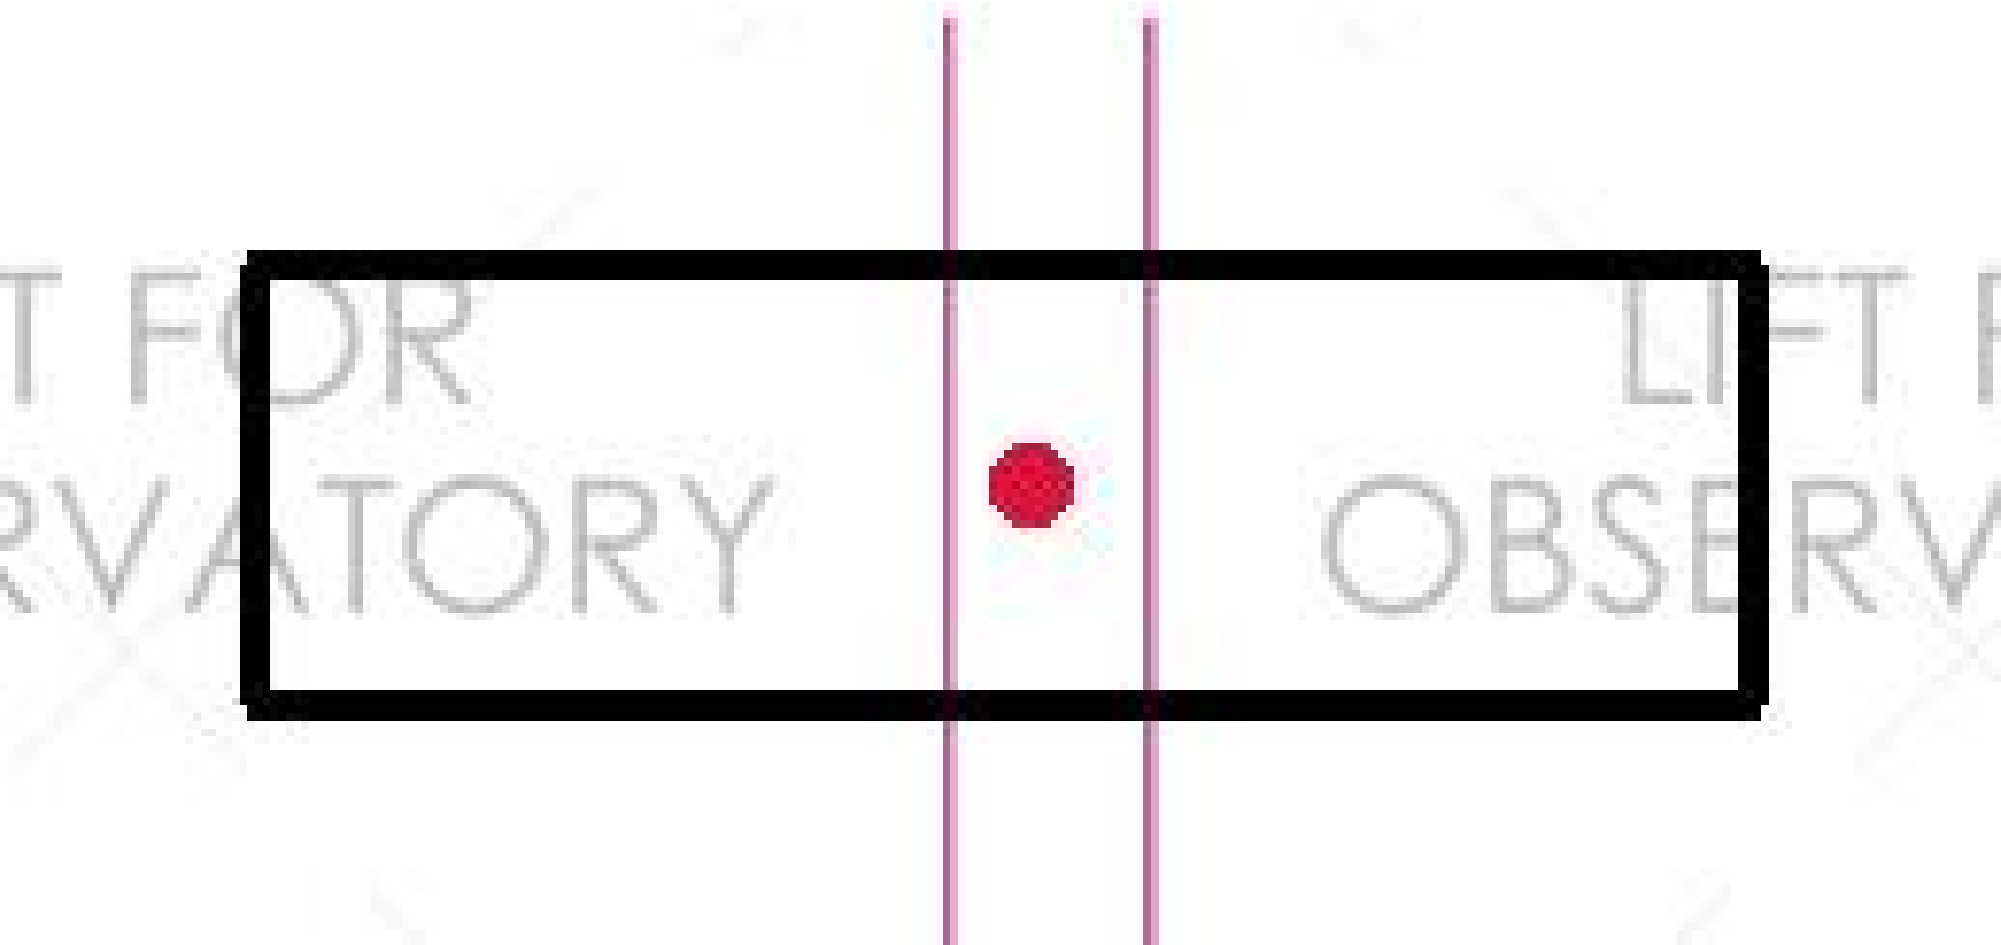

STAIRCASE-2 | vector_fragment_cluster | 20.93

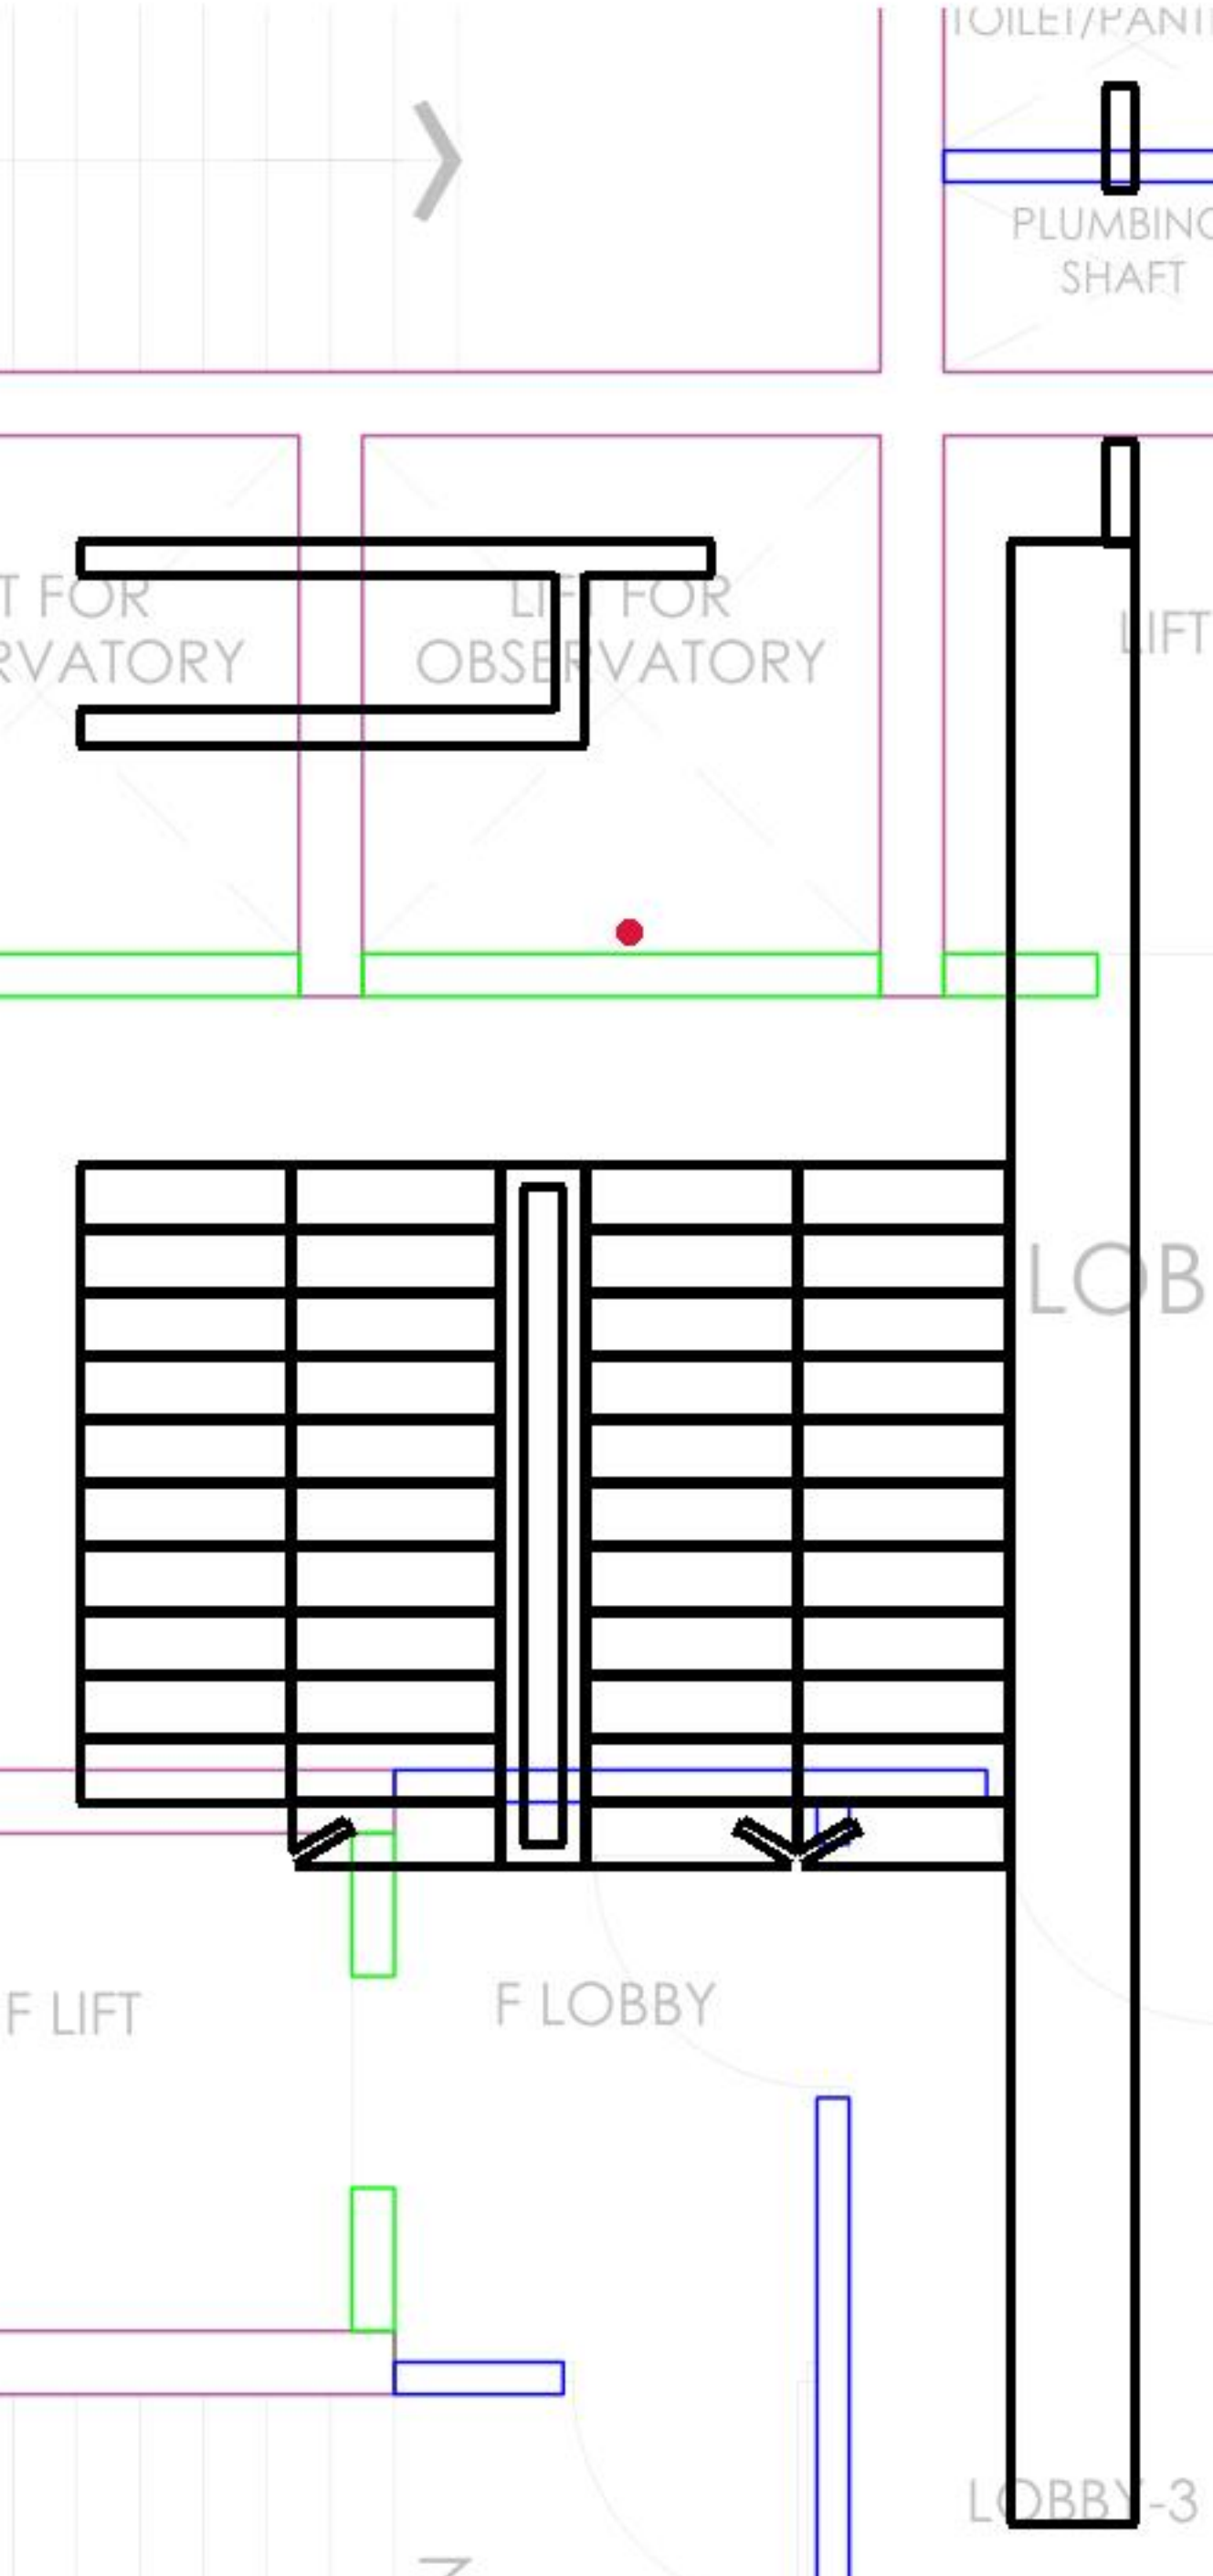

LIFT FOR OBSERVATORY | vector_polygon_exact | 6.03

 

F LIFT | vector_polygon_exact | 6.14

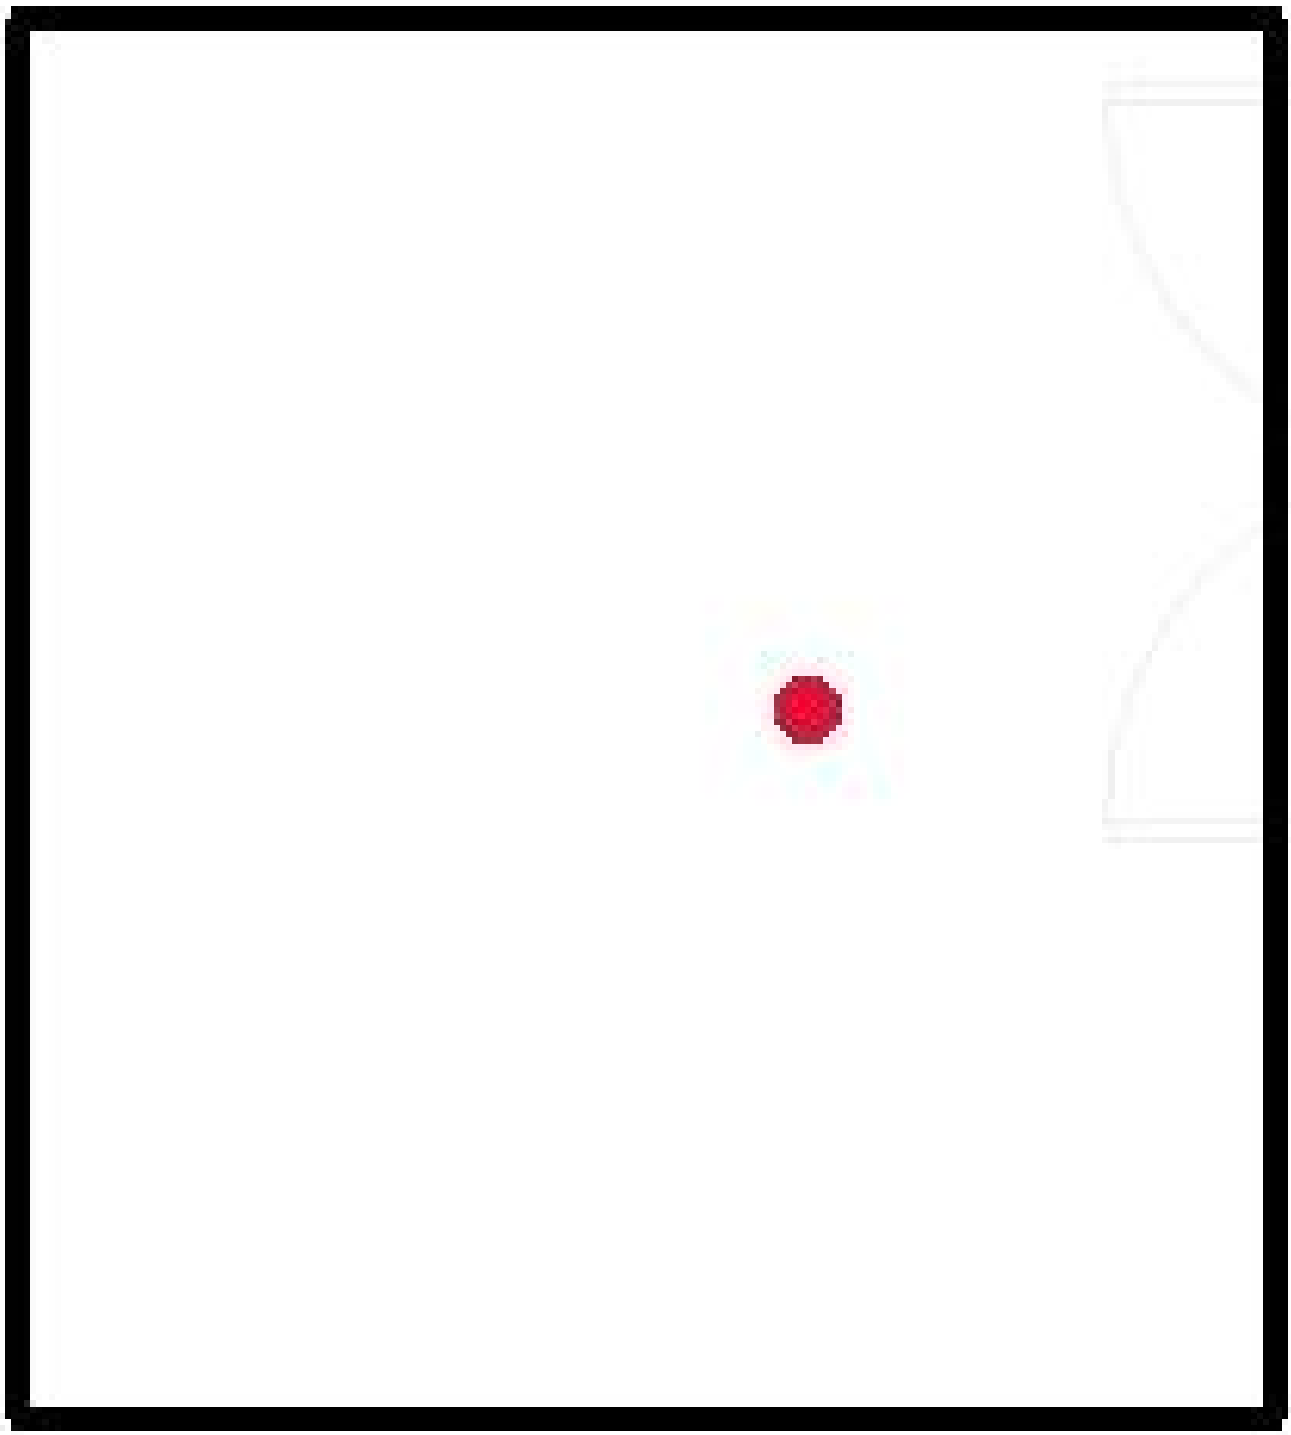

OFFICE | vector_open_residual_partition | 1203.62

OFFICE

PASSAGE

A.H.U

LOBBY. PRESSURIZATION SHAFT

S LIFT - 2

S LIFT - 1

LOBBY-4

FHC

STAIRCASE-2

UP

DN

STR. PRESSURIZATION SHAFT

PANTRY

TOILET/PANTRY EXE

PLUMBING SHAFT

M.TOILET

H.TOILET

F.TOILET

CO-FA

CO-RA

LIFT FOR OBSERVATORY

LIFT FOR OBSERVATORY

LIFT B1

LIFT B2

LIFT B3

RWS

ELV

LOBBY-1

LOBBY-2

F LIFT

F LOBBY

STR. PRESSURIZATION SHAFT

STAIRCASE-1

DN

UP

LOBBY-3

LOBBY. PRESSURIZATION SHAFT

LIFT B4

LIFT B5

LOBBY. PRESSURIZATION SHAFT

PASSAGE

A.H.U

FHC

CHW

CO-FA

ELEC

CO-RA

LIFT FOR OBSERVATORY | vector_polygon_exact | 6.03

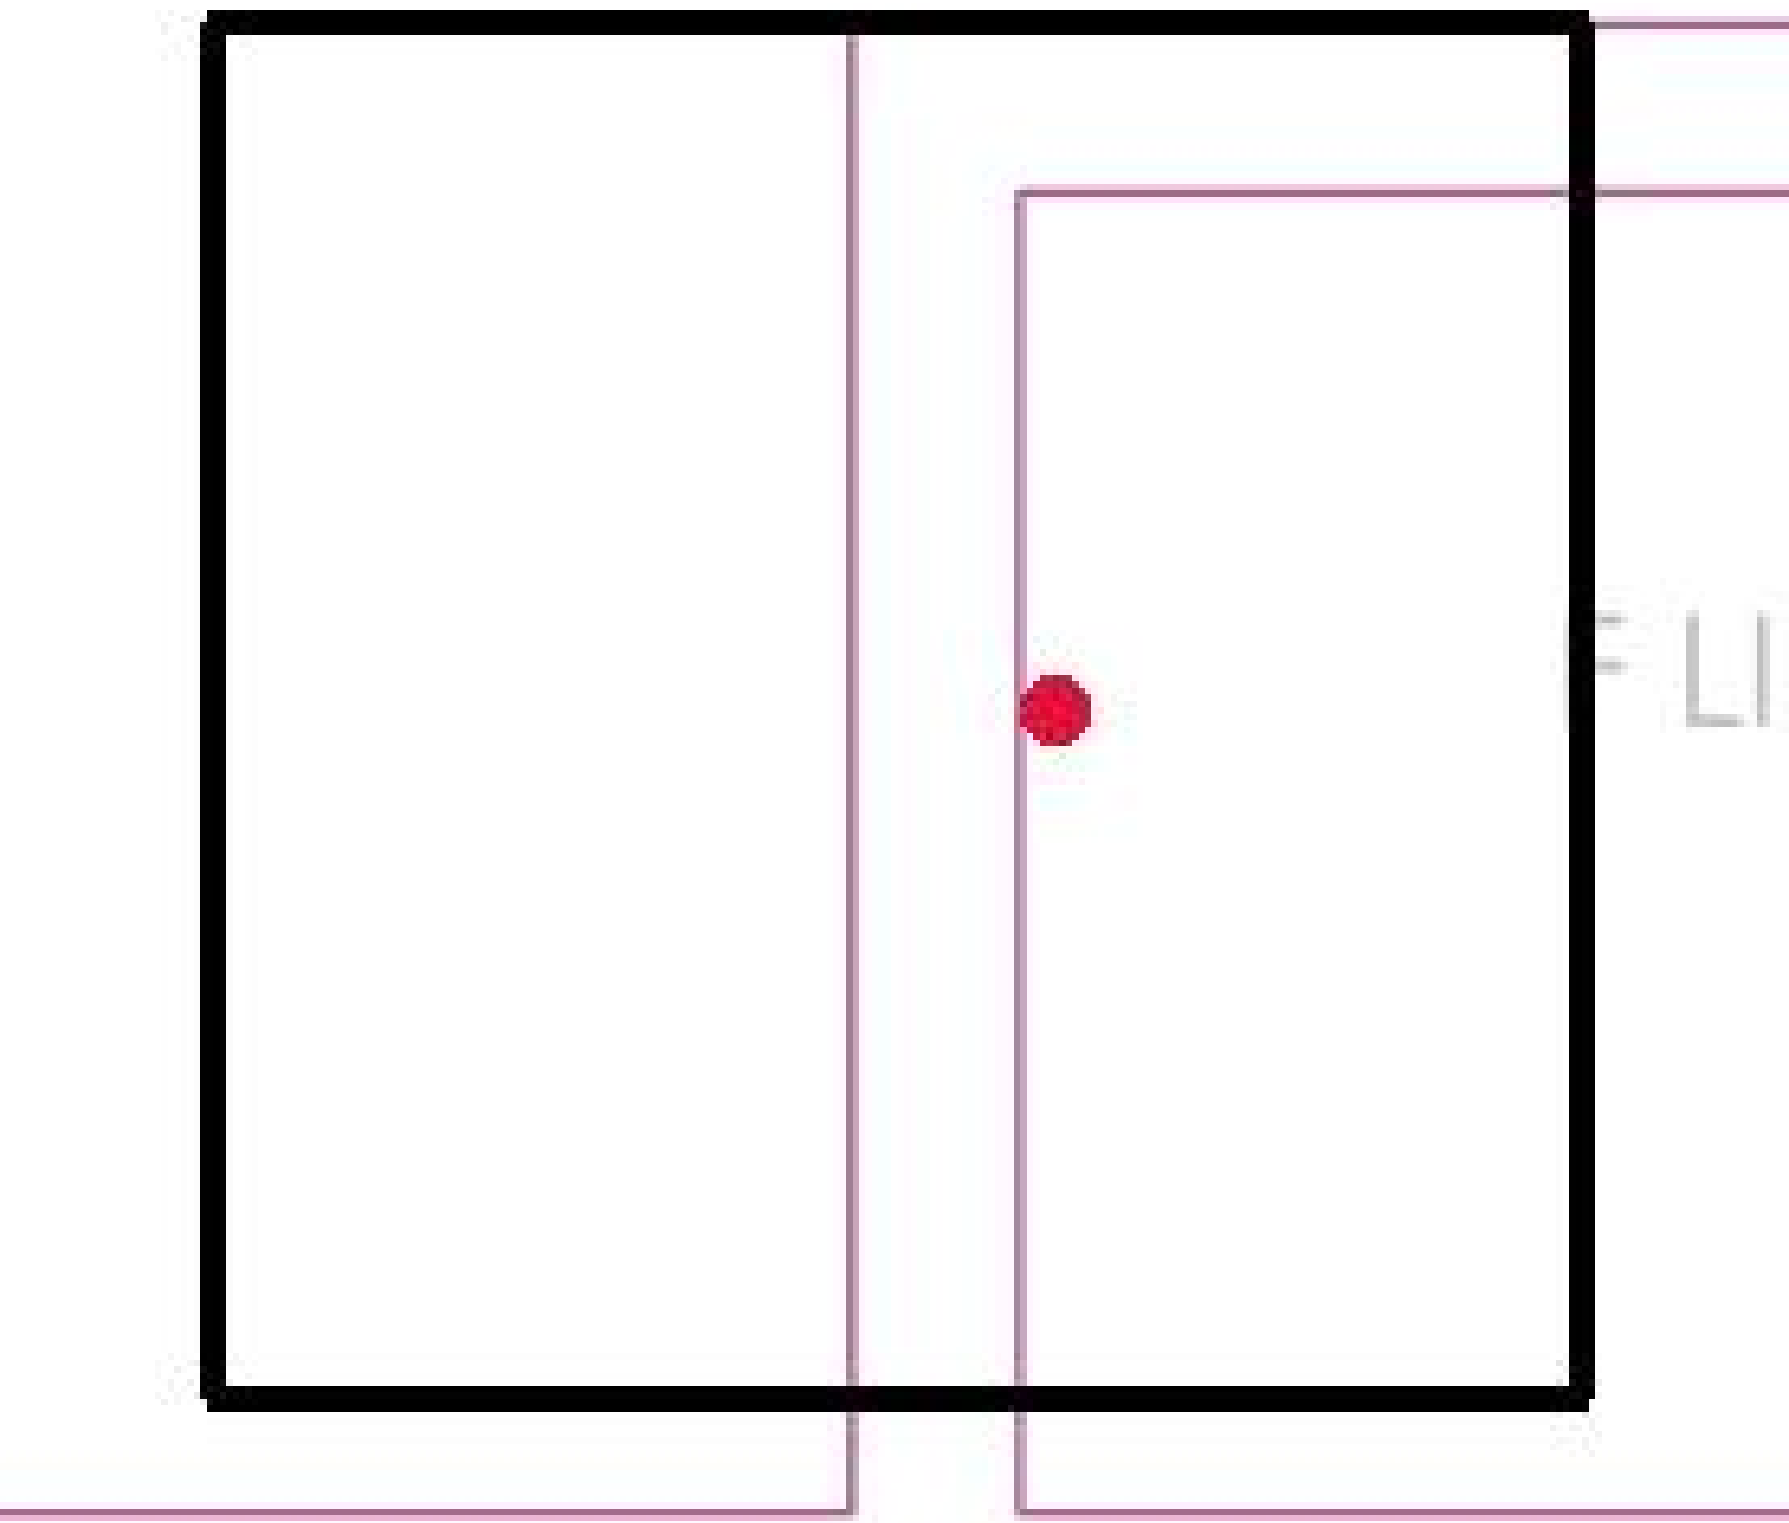

STAIRCASE-1 | vector_fragment_cluster | 28.34

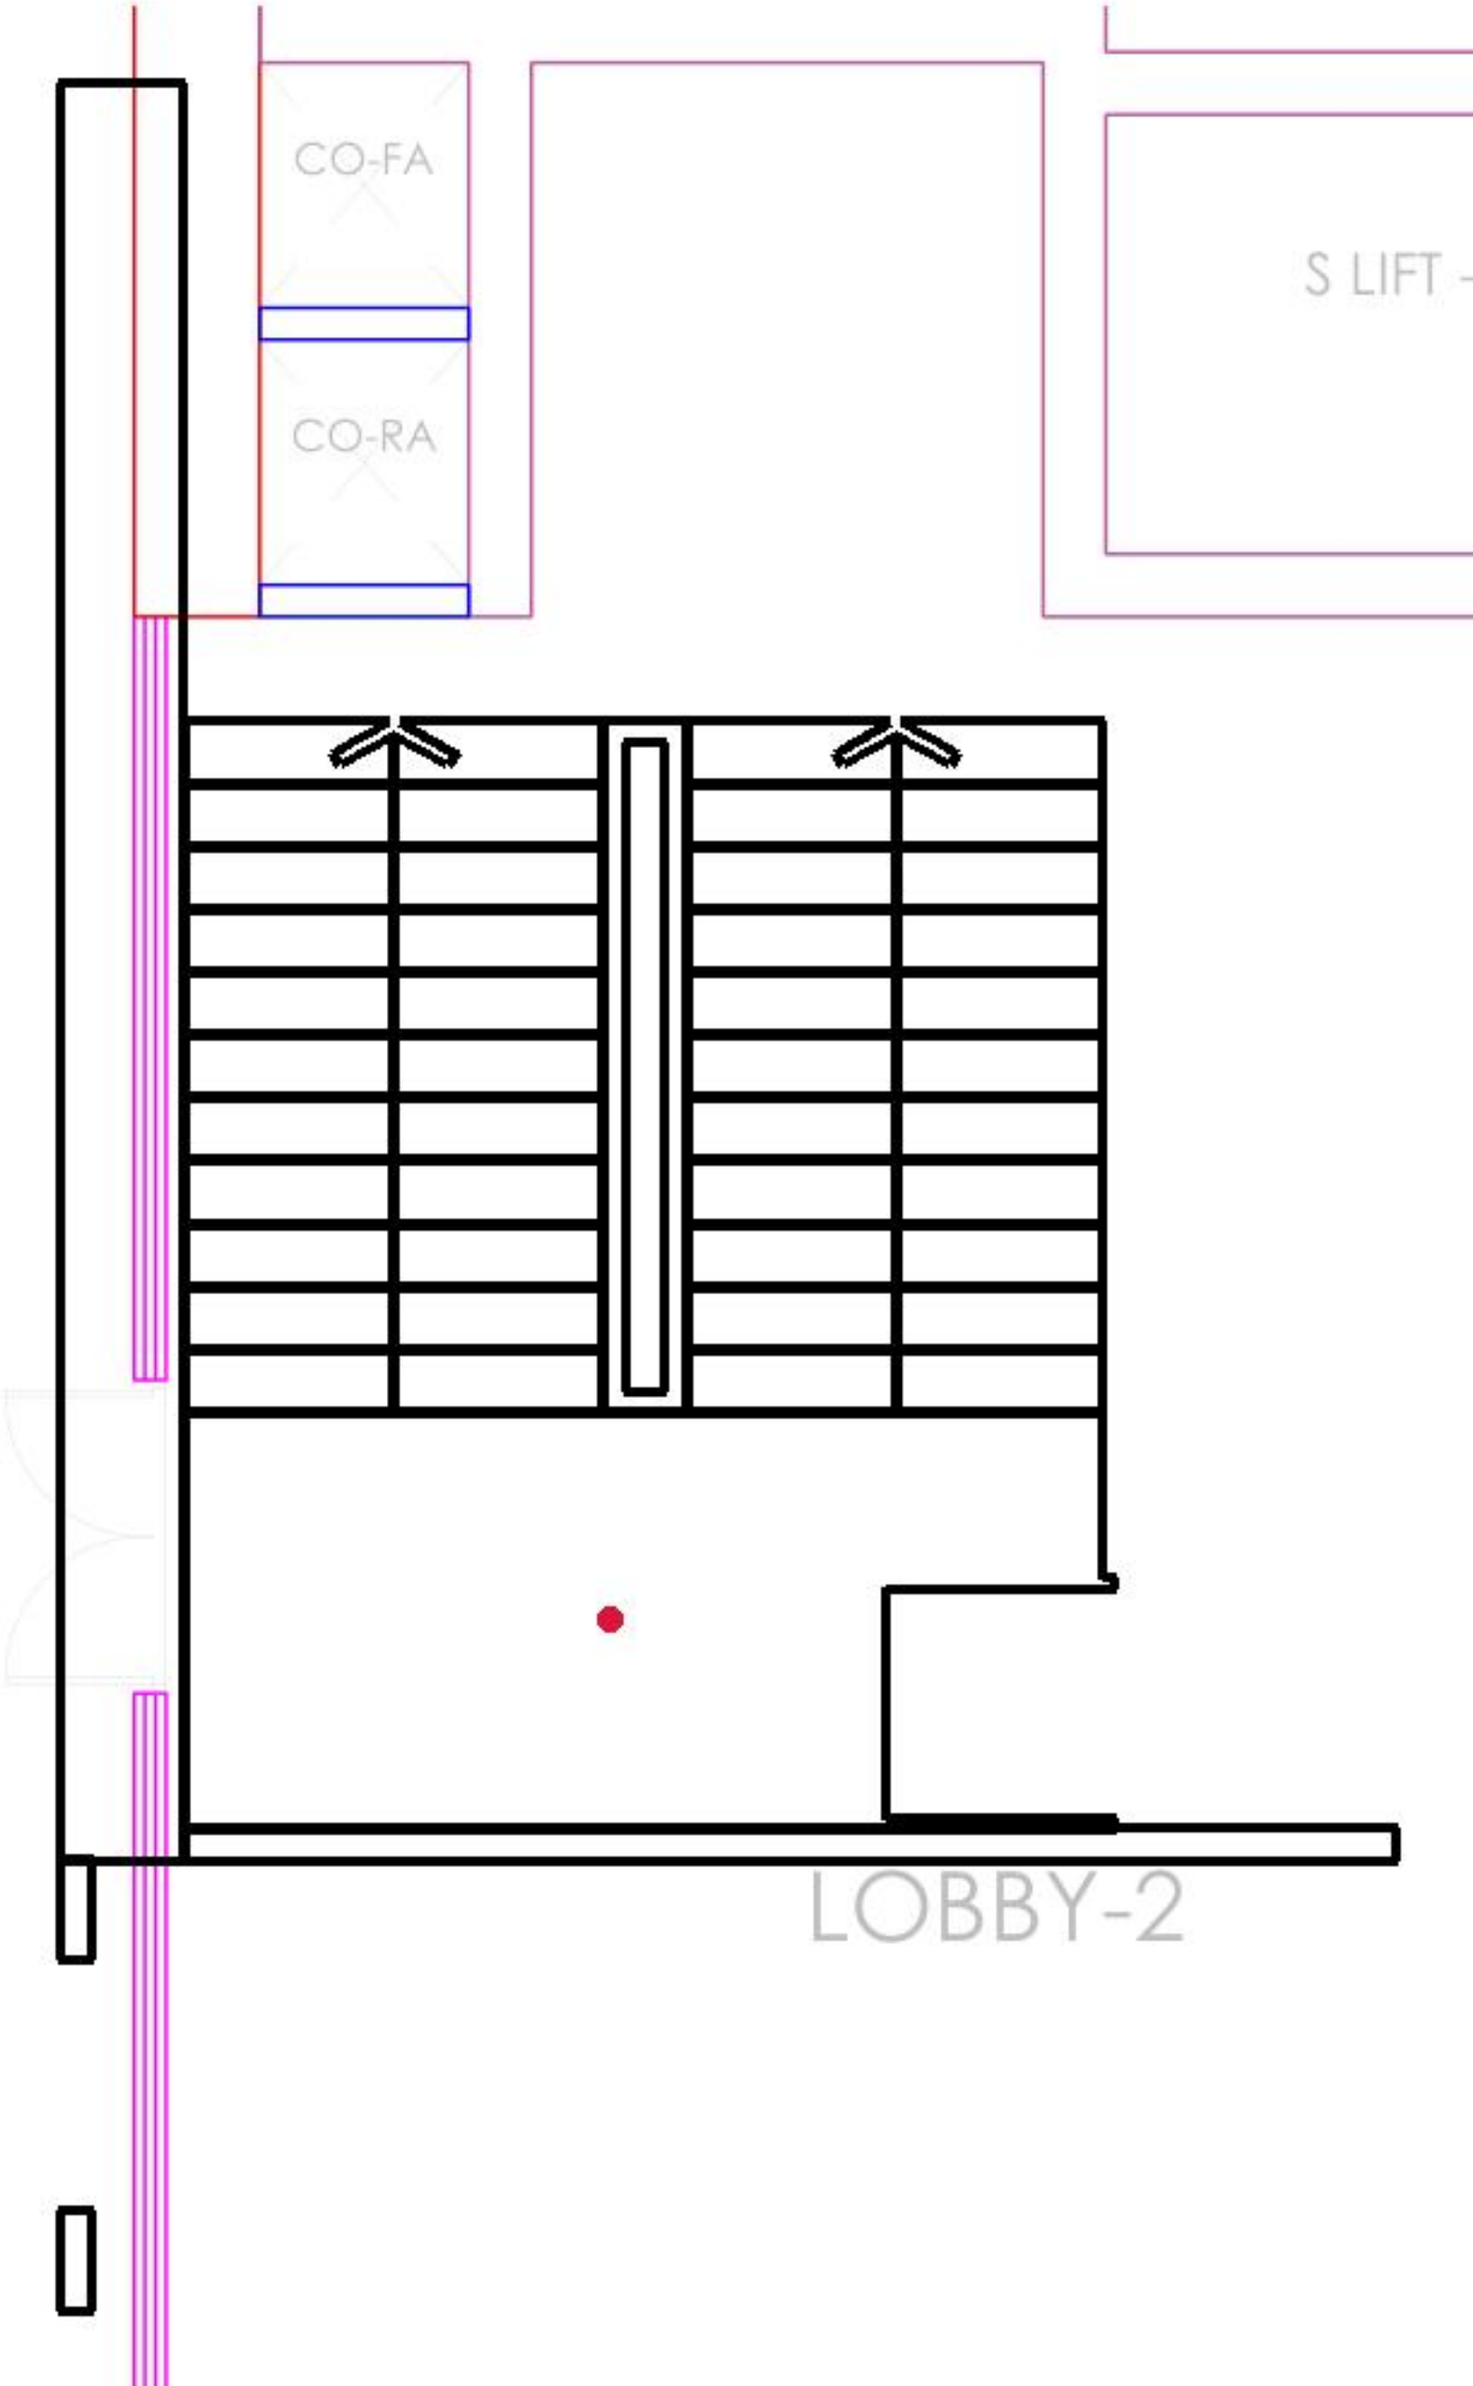

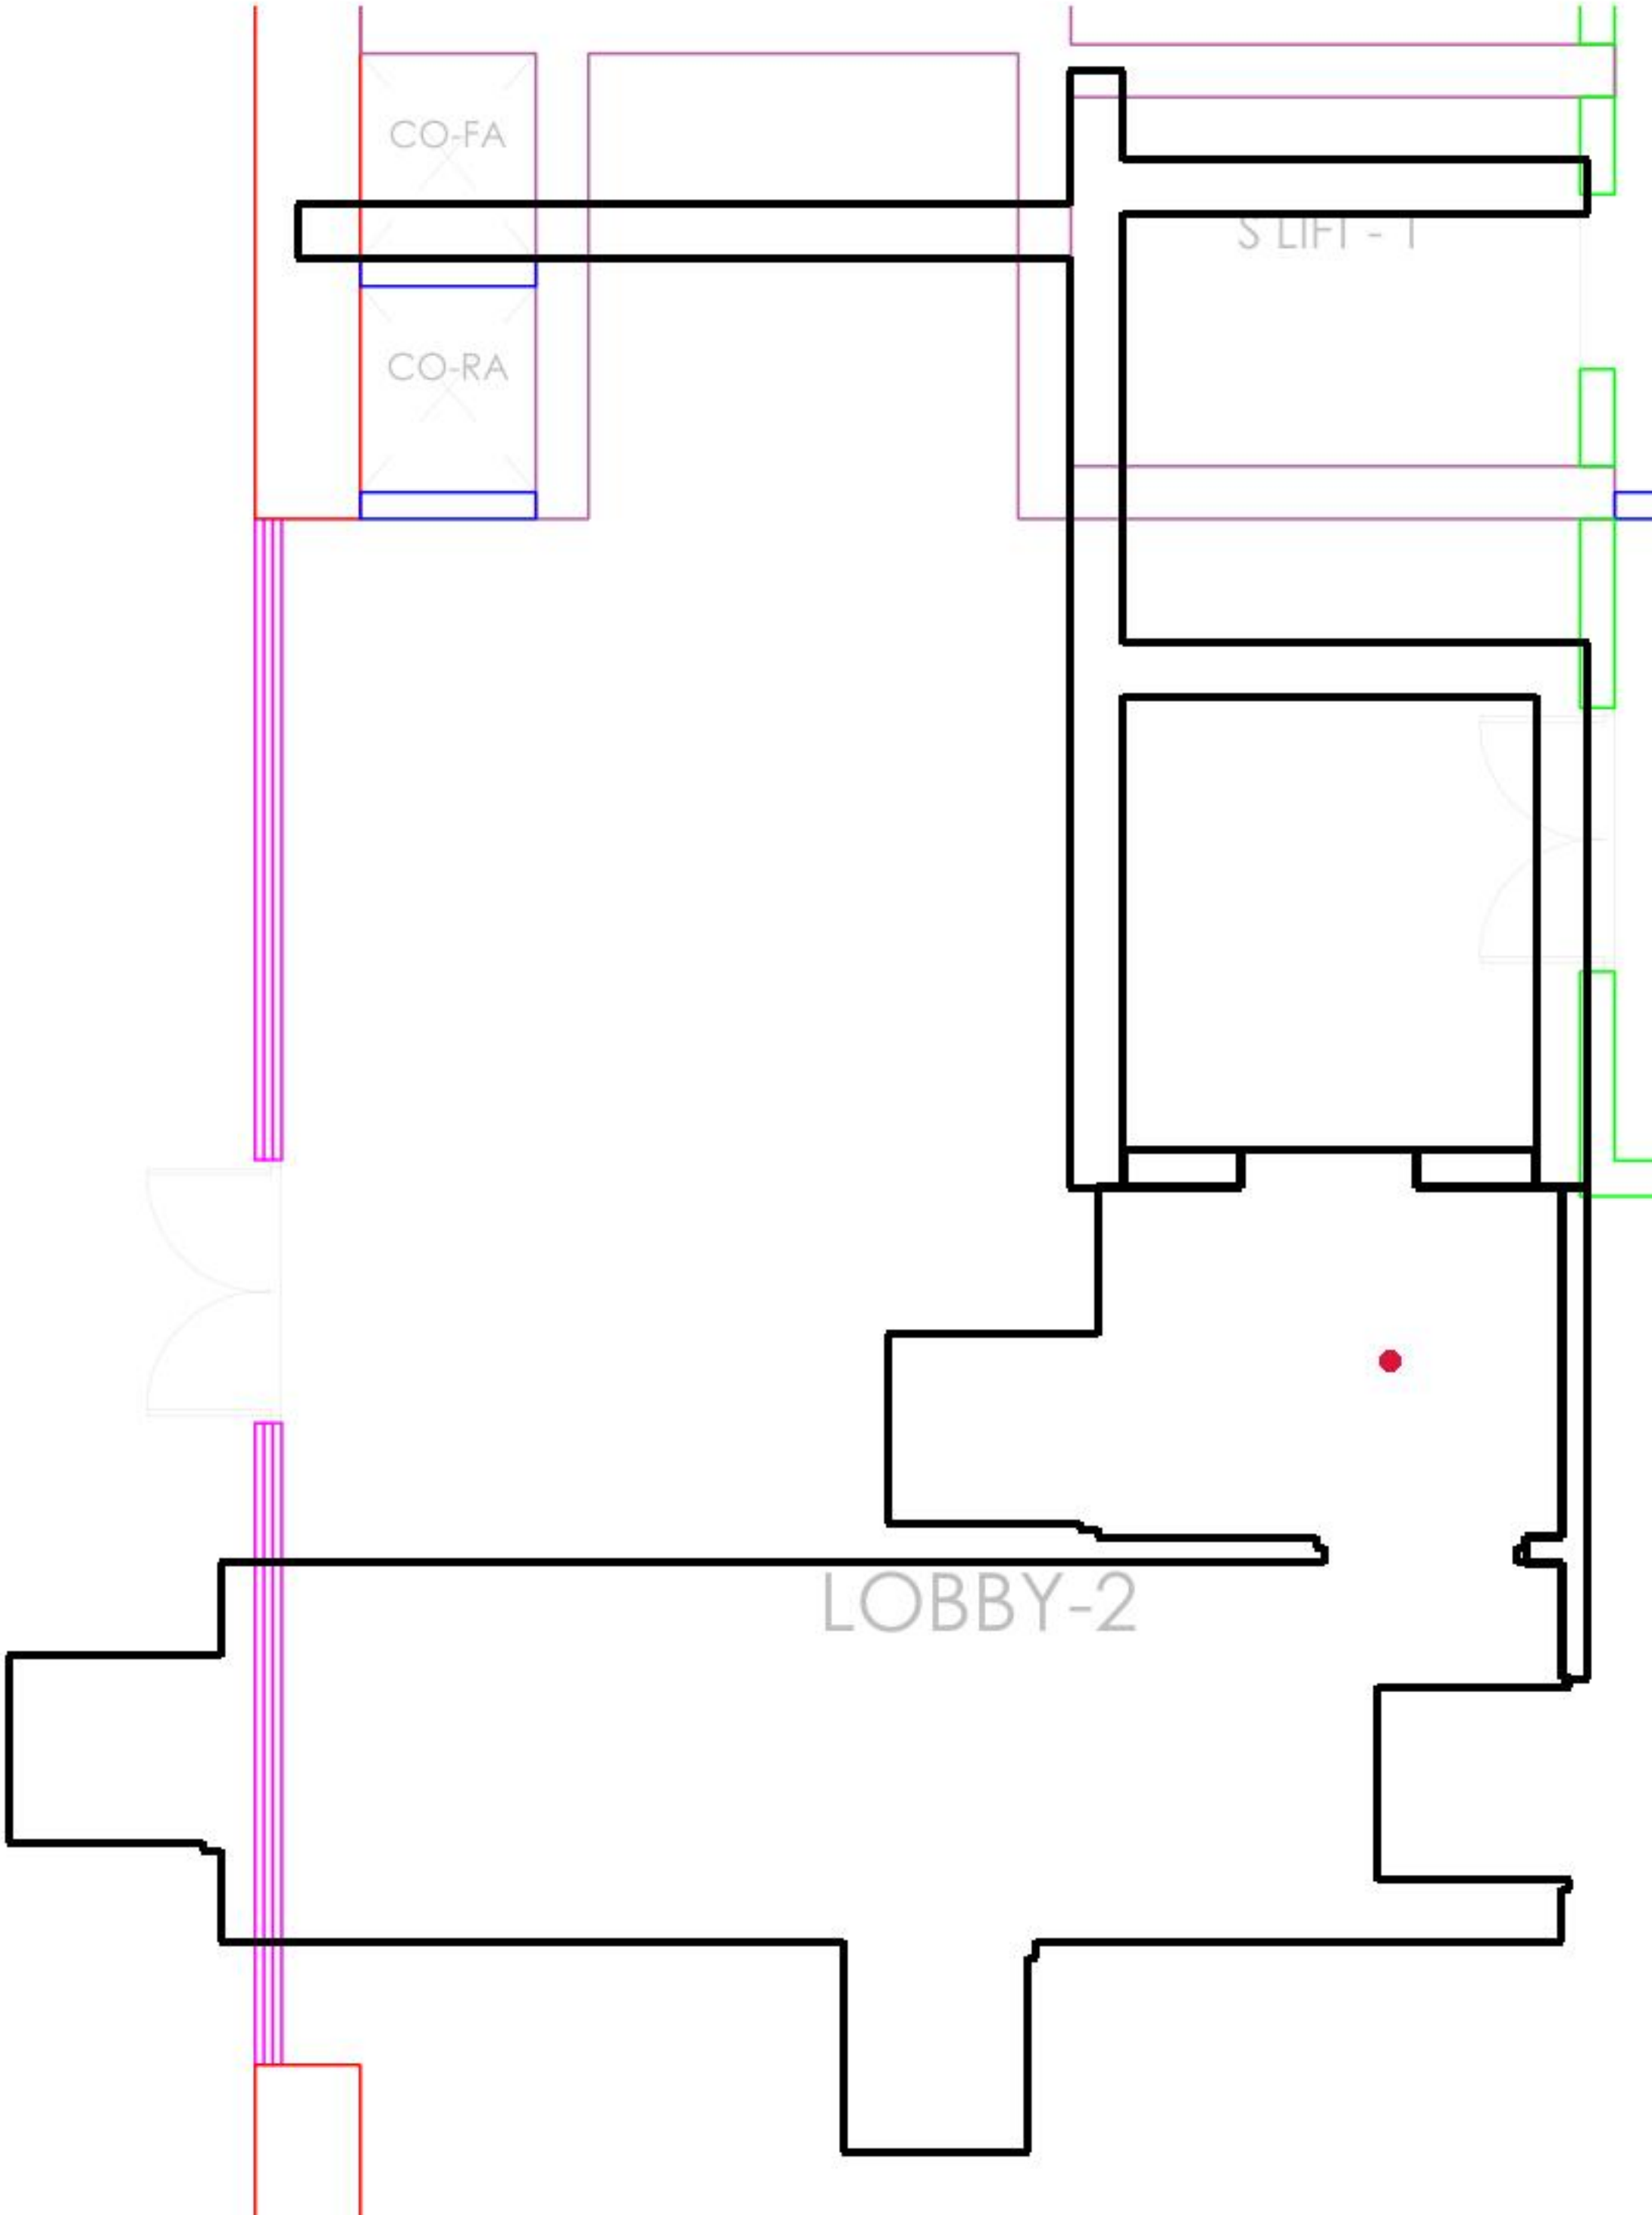
CO-FA
CO-RA
S LIFT - 1
LOBBY-2

TOILET/PANTRY EXE | vector_p

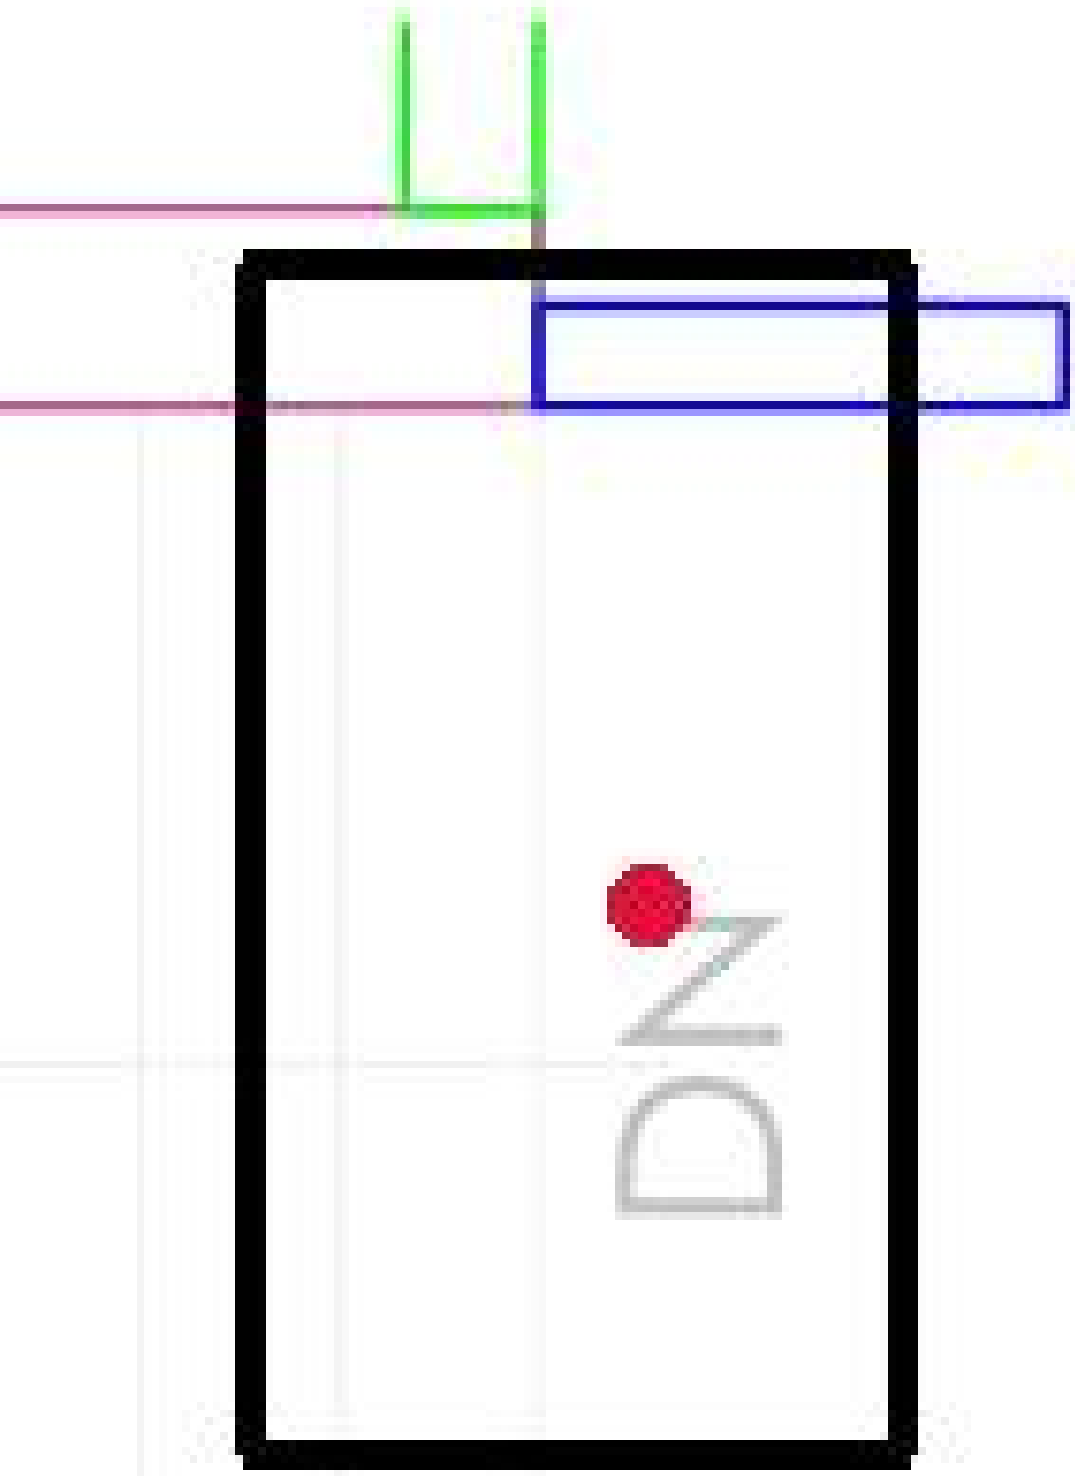

LOBBY-3 | vector_open_fragment_partition | 15.61

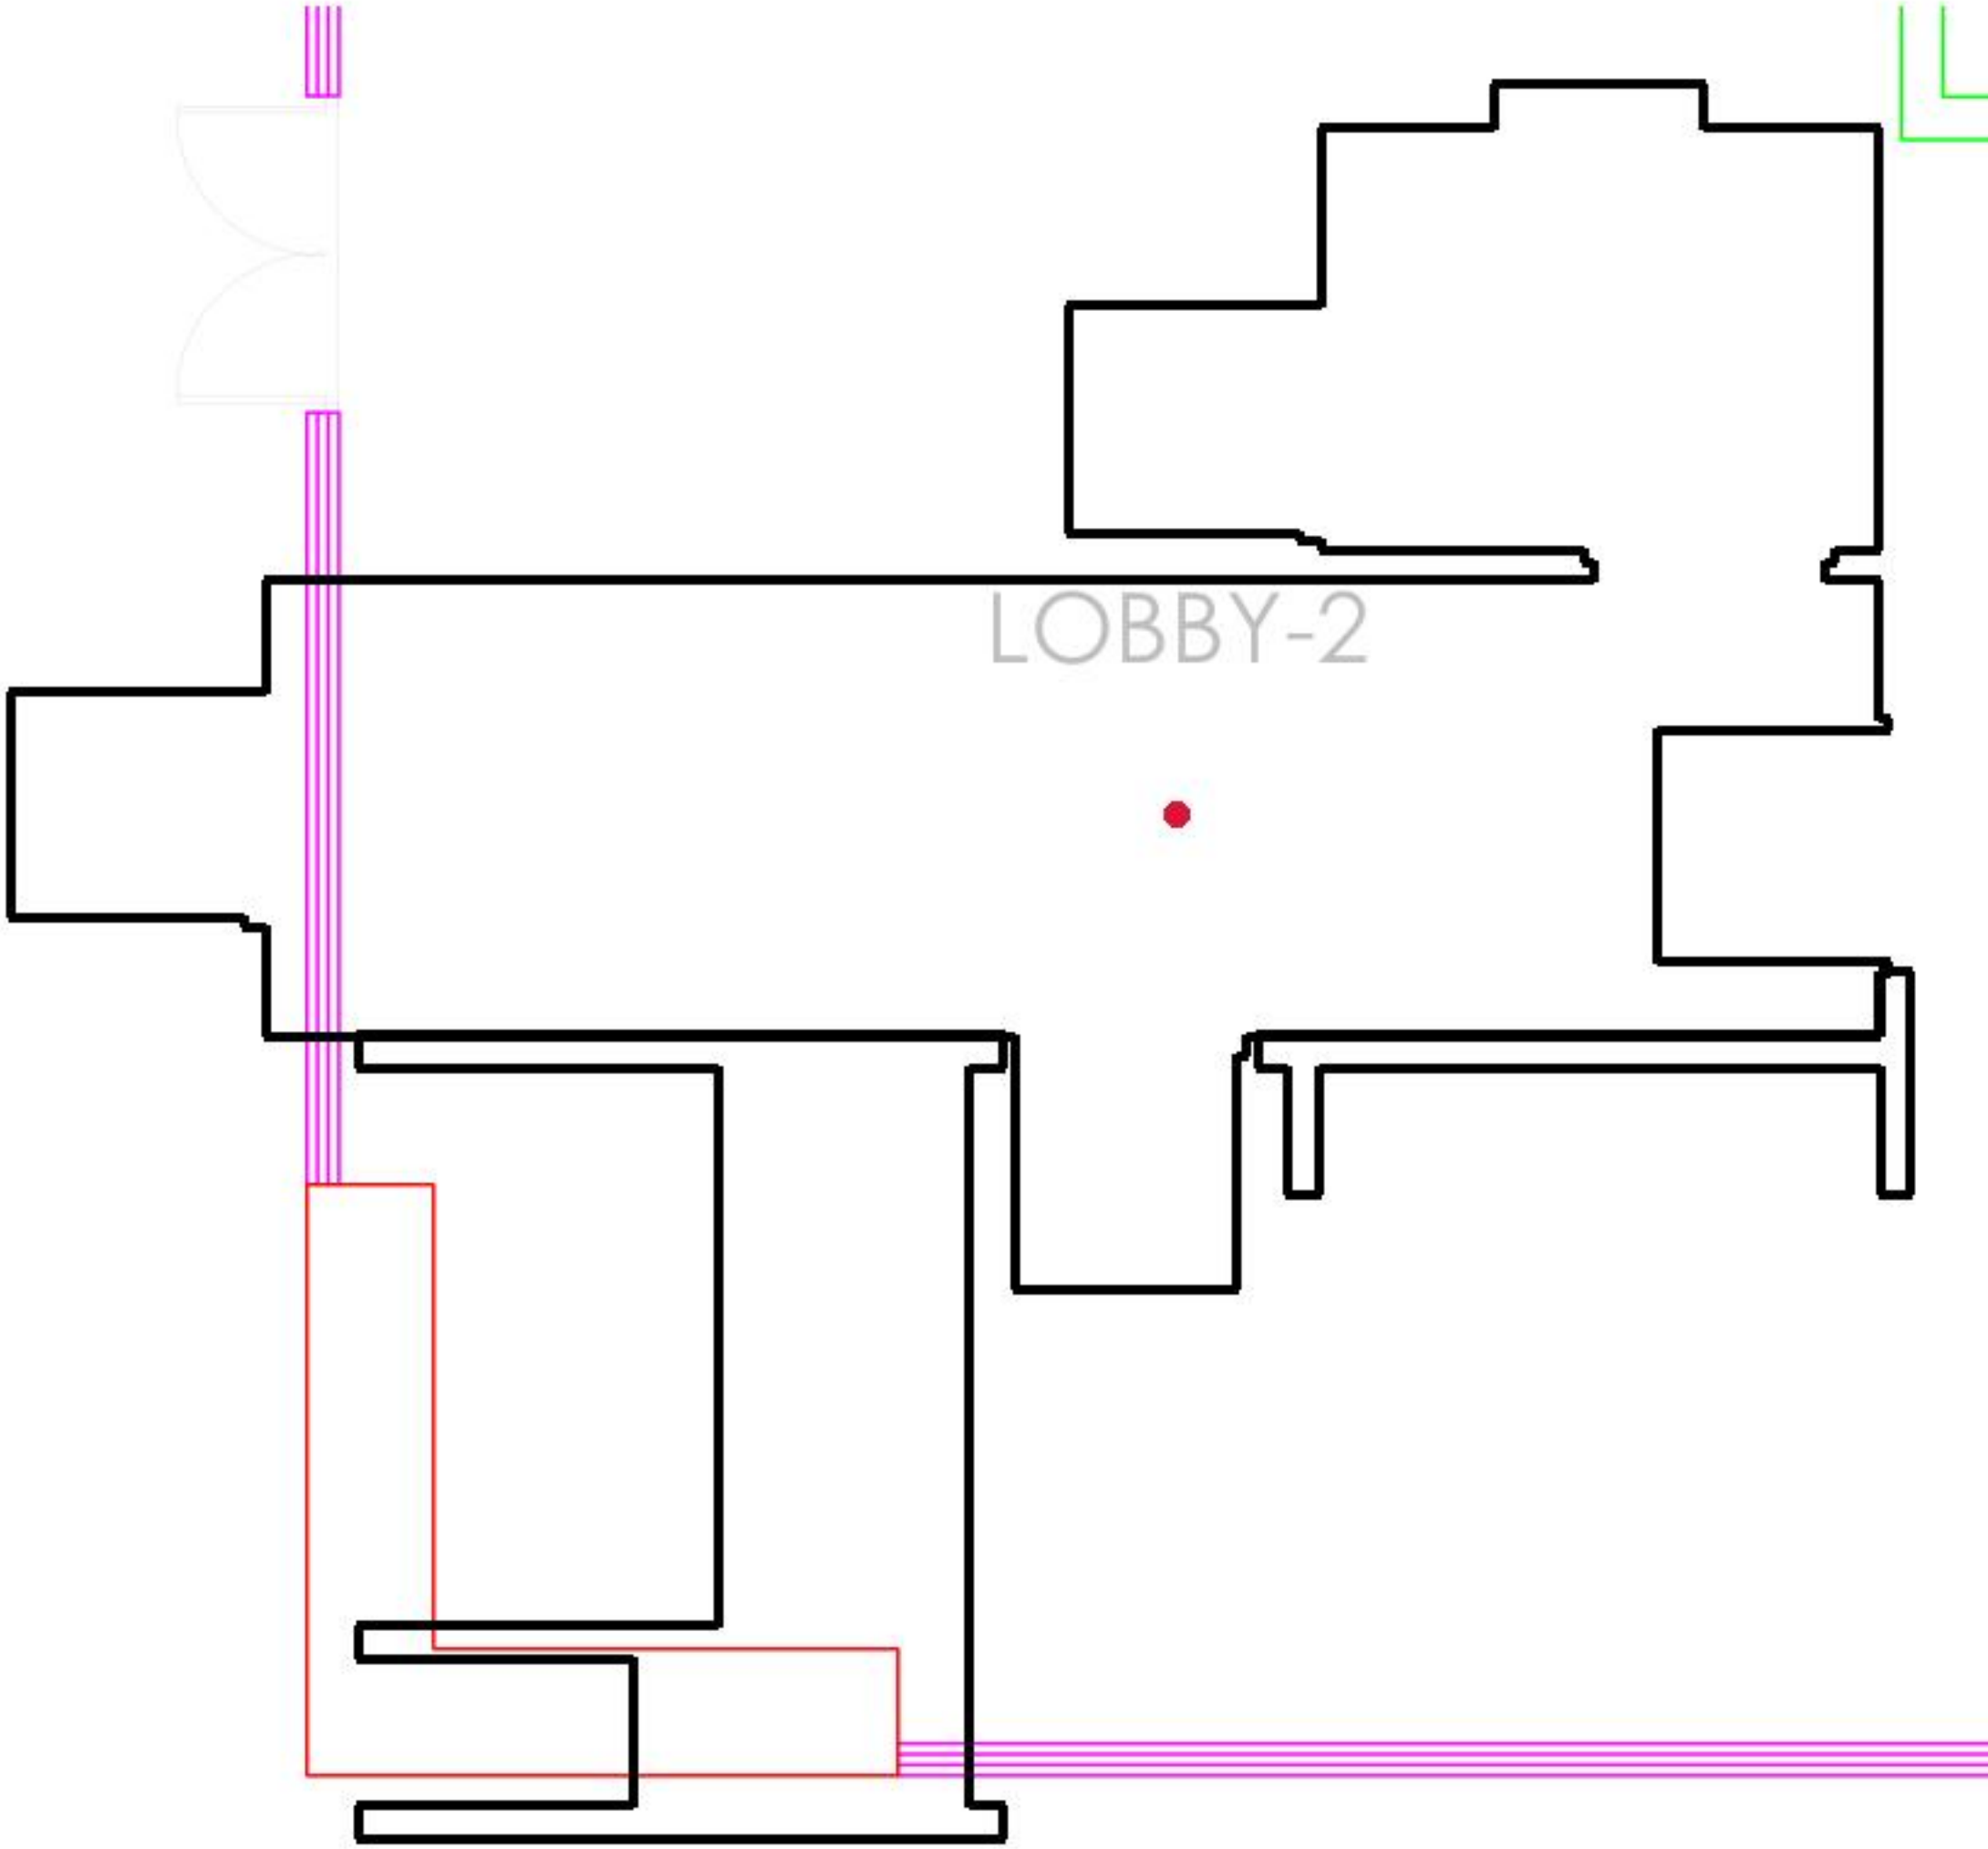

STR PRESSURIZATION SHAFT | vector_polygon_exact

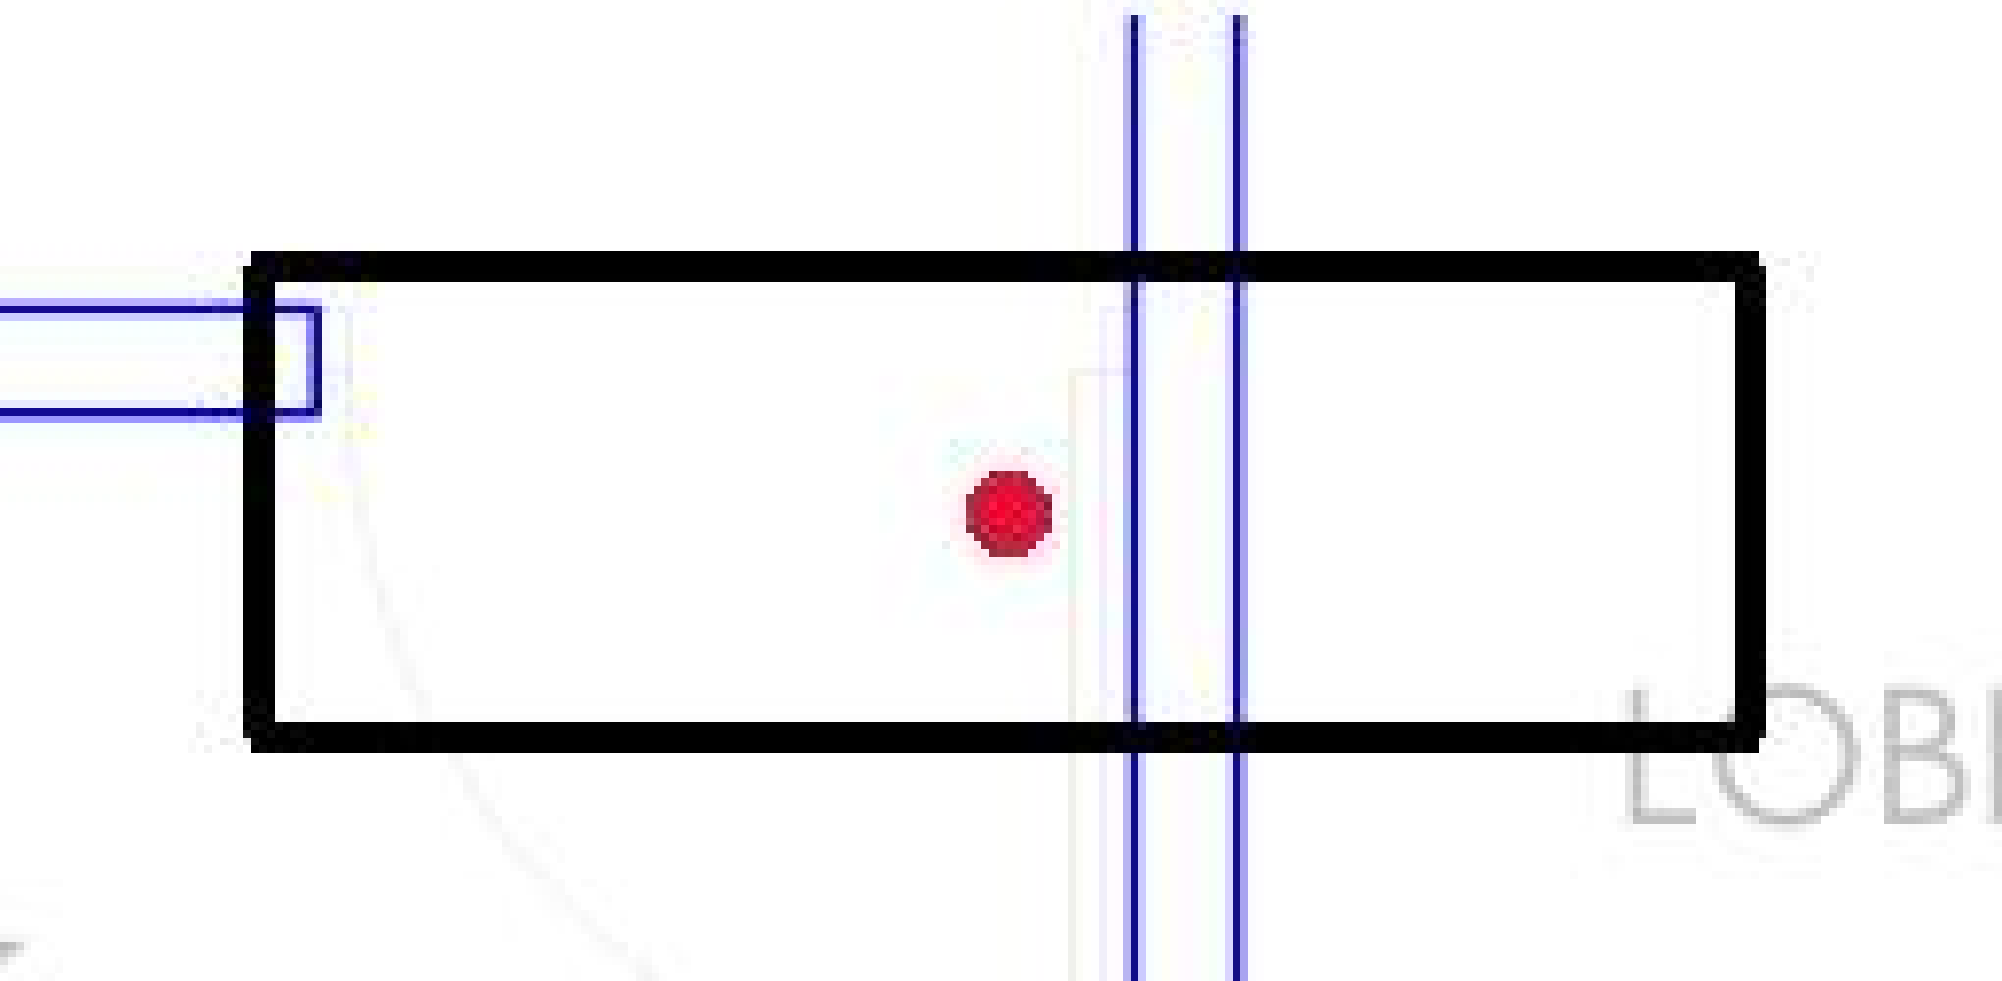

PLUMBING SHAFT | vector_p

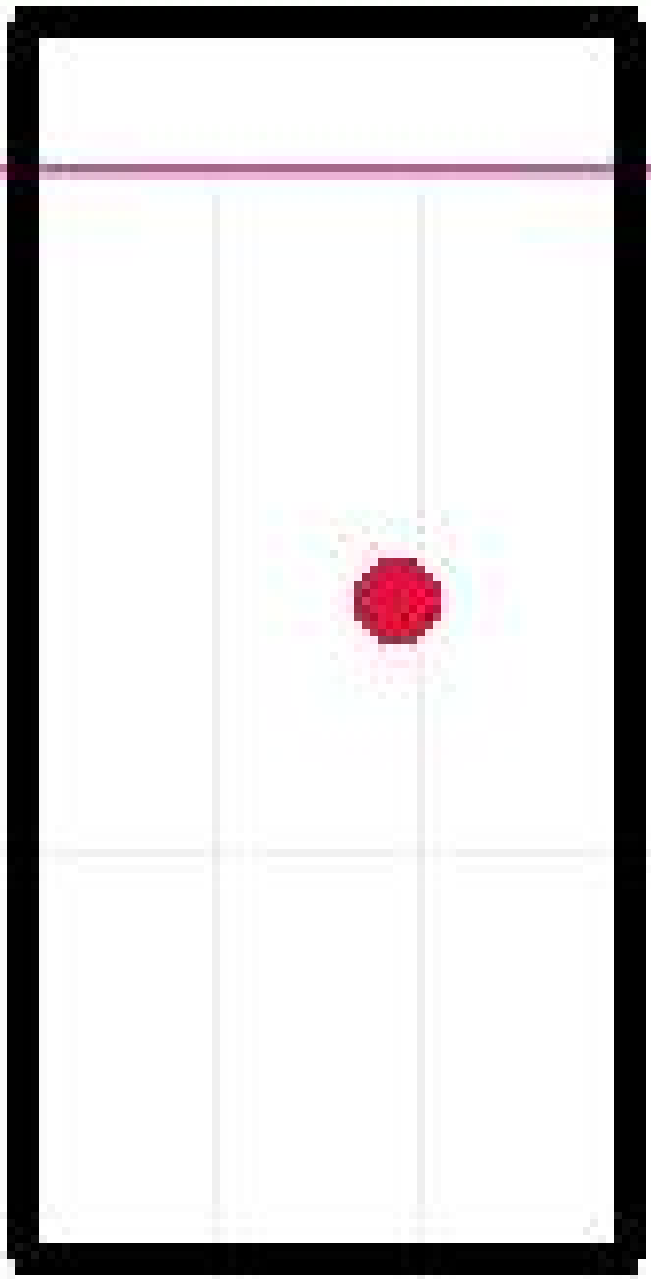

LOBBY-1 | vector_open_residual_partition | 59.64

OFFICE

PASSAGE

A.H.U

LOBBY. PRESSURIZATION SHAFT

S LIFT - 2

S LIFT - 1

LOBBY-4

FHC

STAIRCASE-2

UP

DN

STR. PRESSURIZATION SHAFT

PANTRY

TOILET/PANTRY EXE

PLUMBING SHAFT

M.TOILET

H.TOILET

F.TOILET

CO-FA

CO-RA

LIFT FOR OBSERVATORY

LIFT FOR OBSERVATORY

LIFT B1

LIFT B2

LIFT B3

RWS

ELV

LOBBY-1

LOBBY-2

F LIFT

F LOBBY

STR. PRESSURIZATION SHAFT

STAIRCASE-1

DN

UP

LOBBY-3

LOBBY. PRESSURIZATION SHAFT

LIFT B4

LIFT B5

LOBBY. PRESSURIZATION

PASSAGE

A.H.U

FHC

CHW

CO-FA

ELEC

CO-RA

LIFT B1 | vector_polygon_exact | 6.03

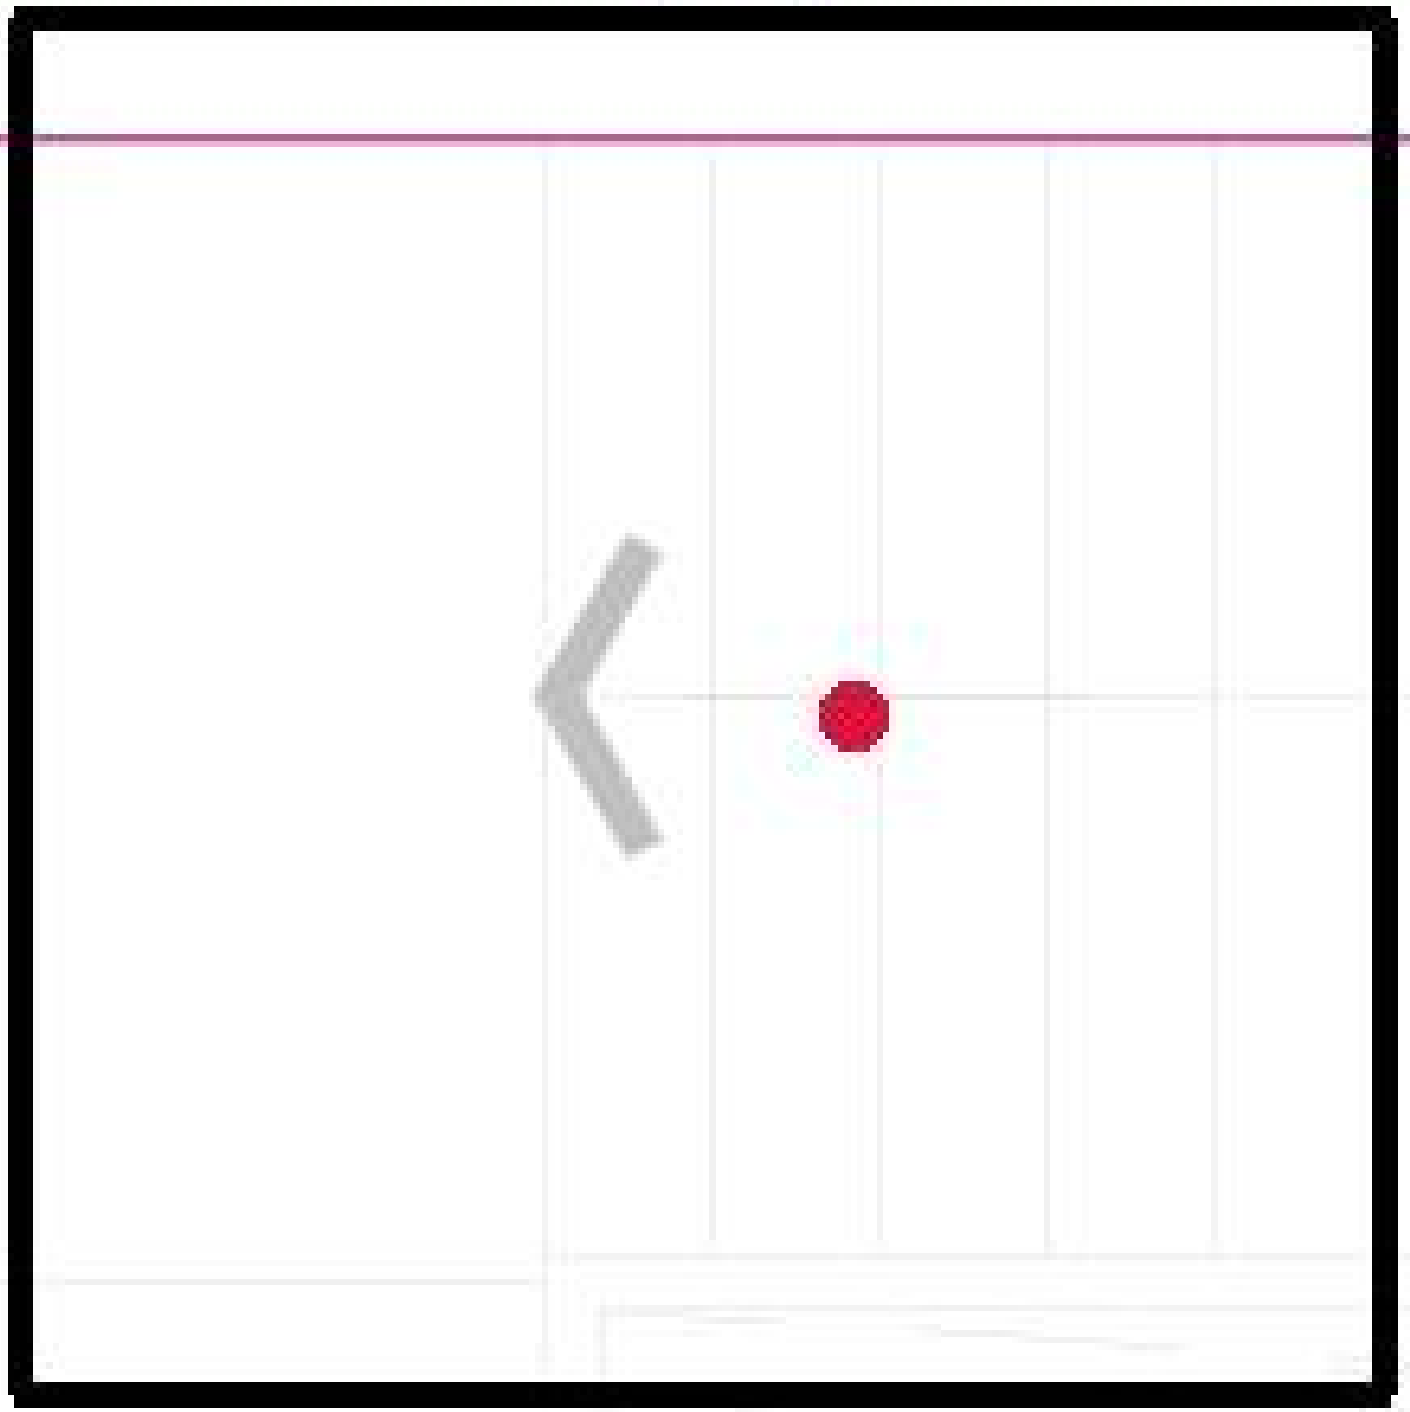

PANTRY | vector_polygon_closed_gap | 4.12

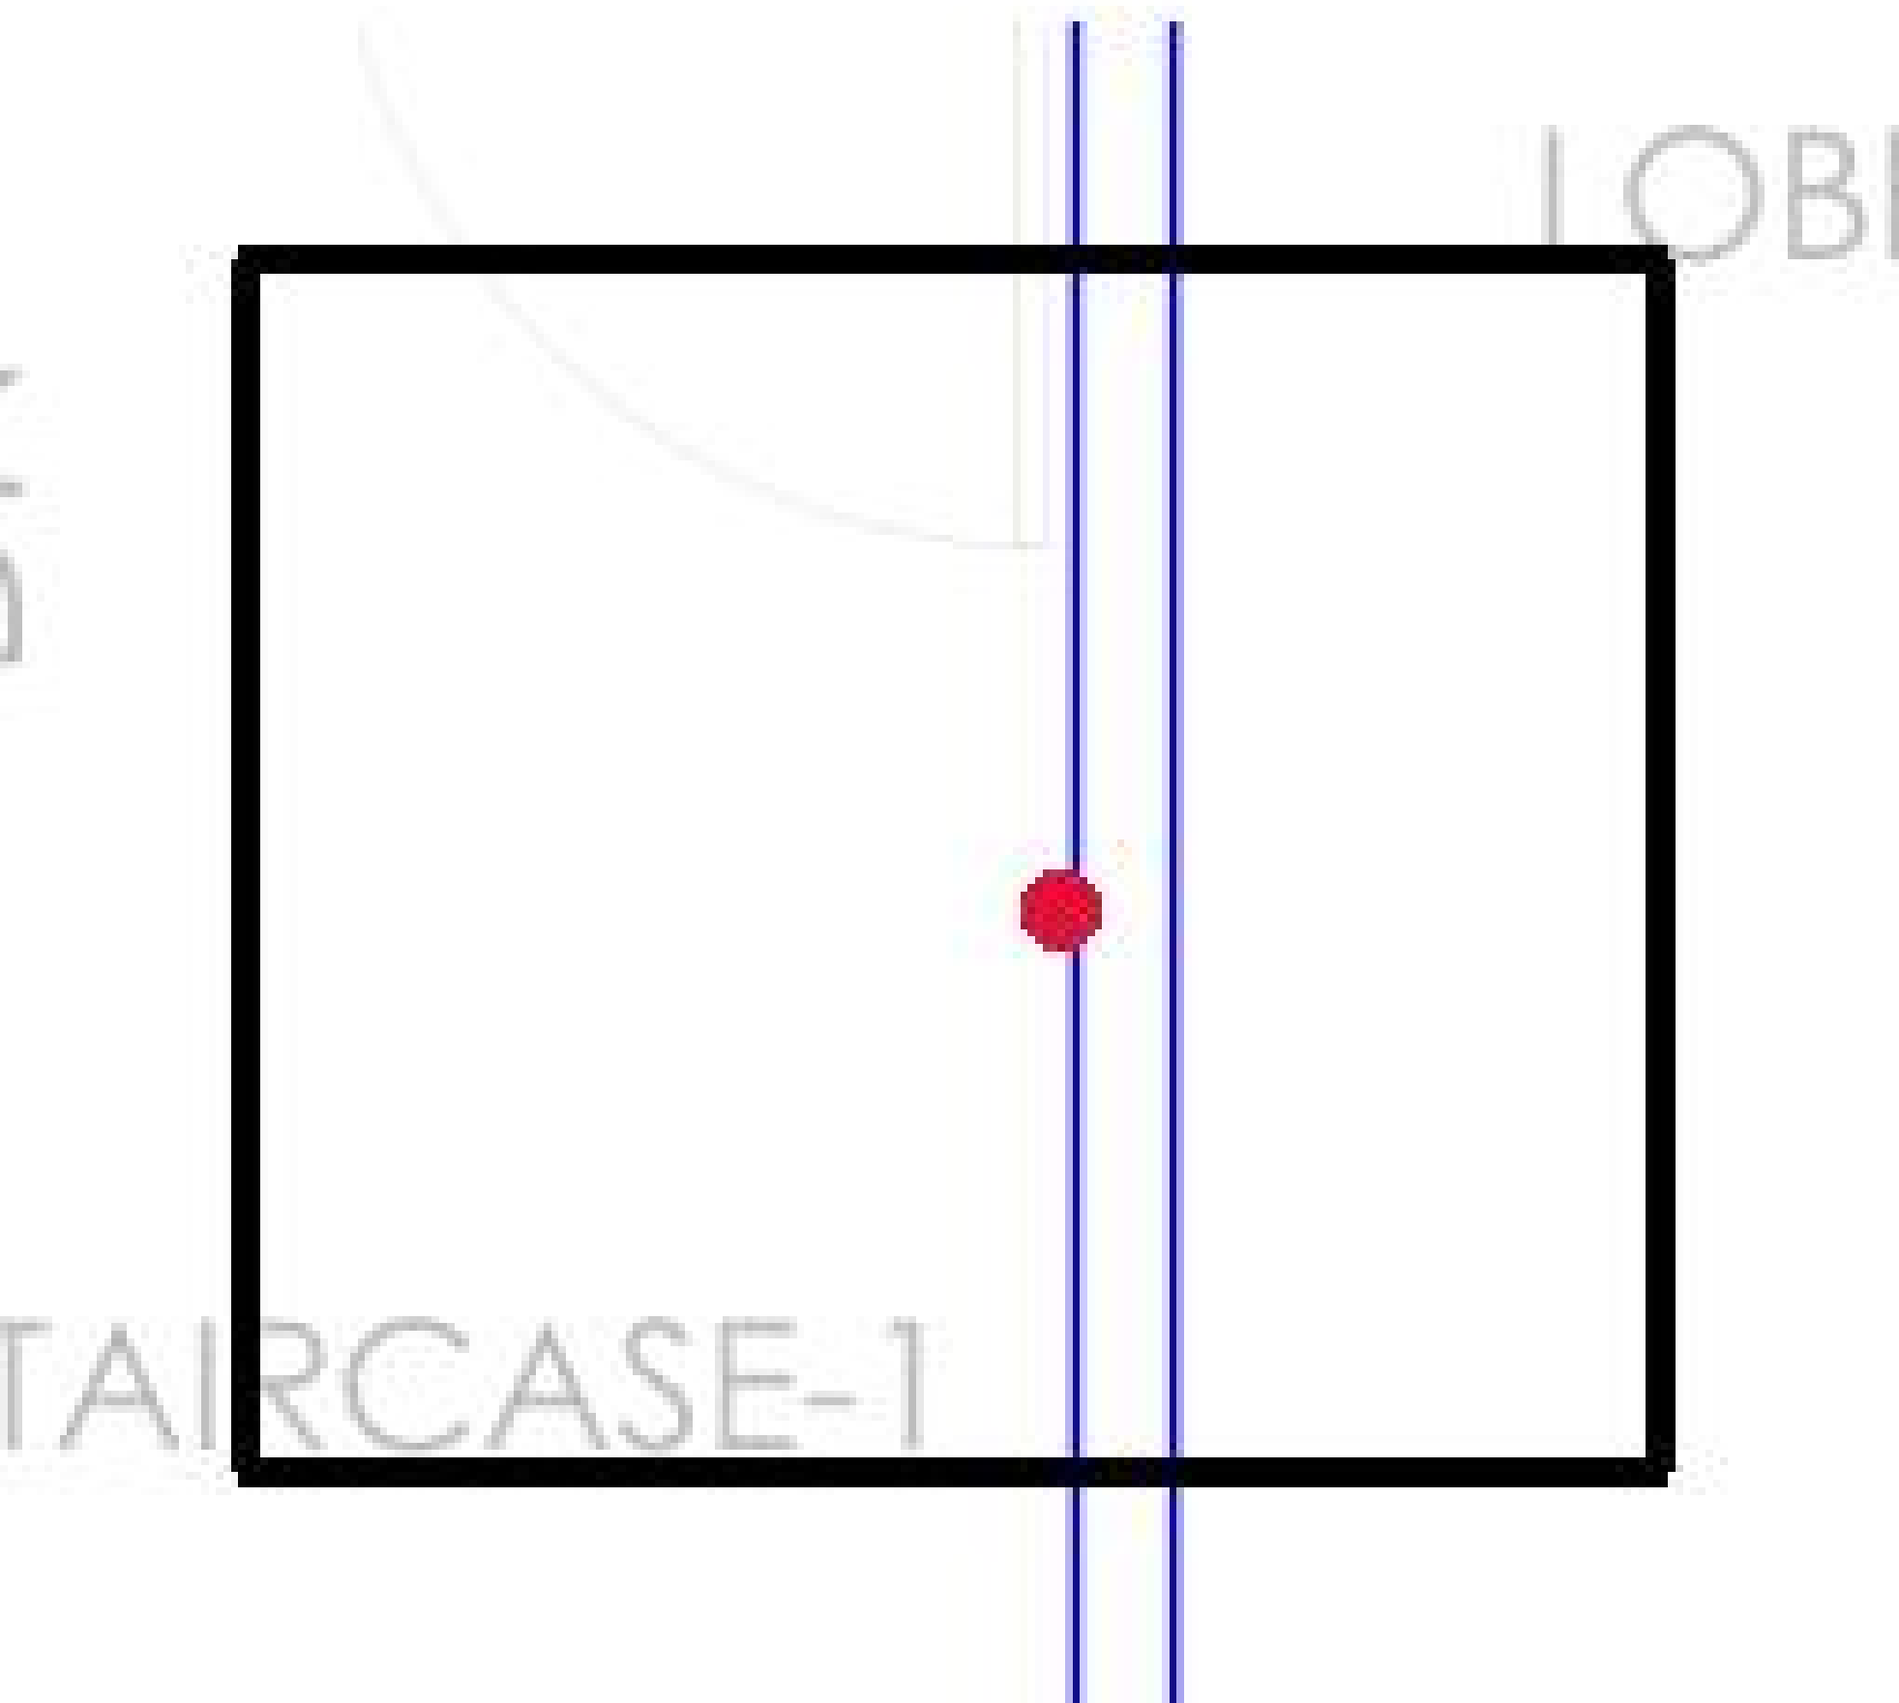

LOBBY. PRESSURIZATION SHAFT | vector_polygon_exact | 1.6

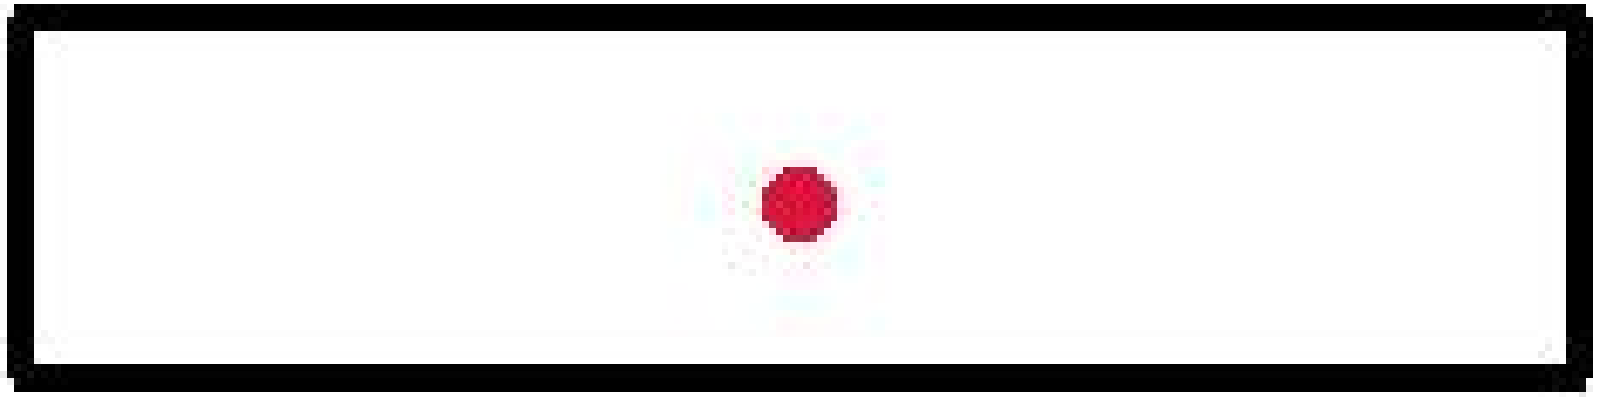

FHC | vector_polygon_exact |

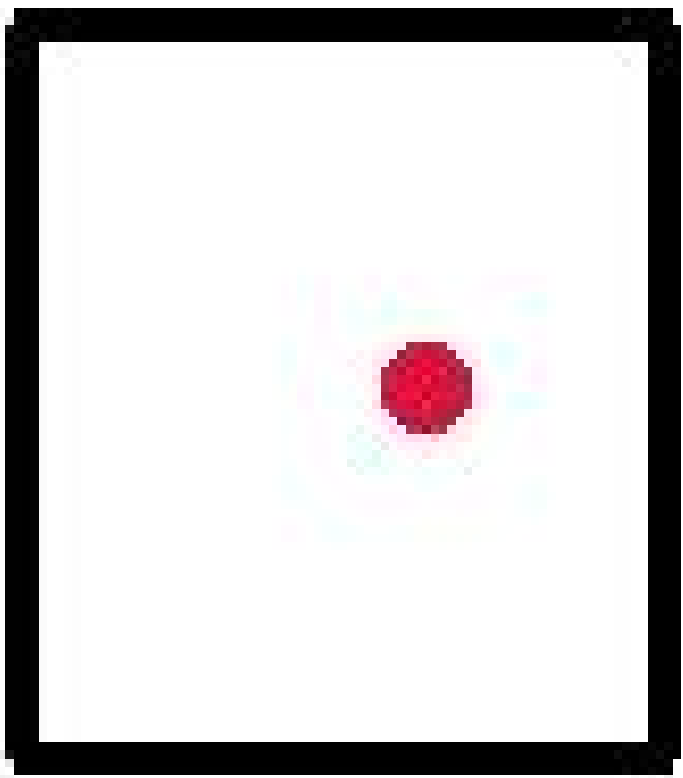

ELEC | vector_polygon_exact | 4.54

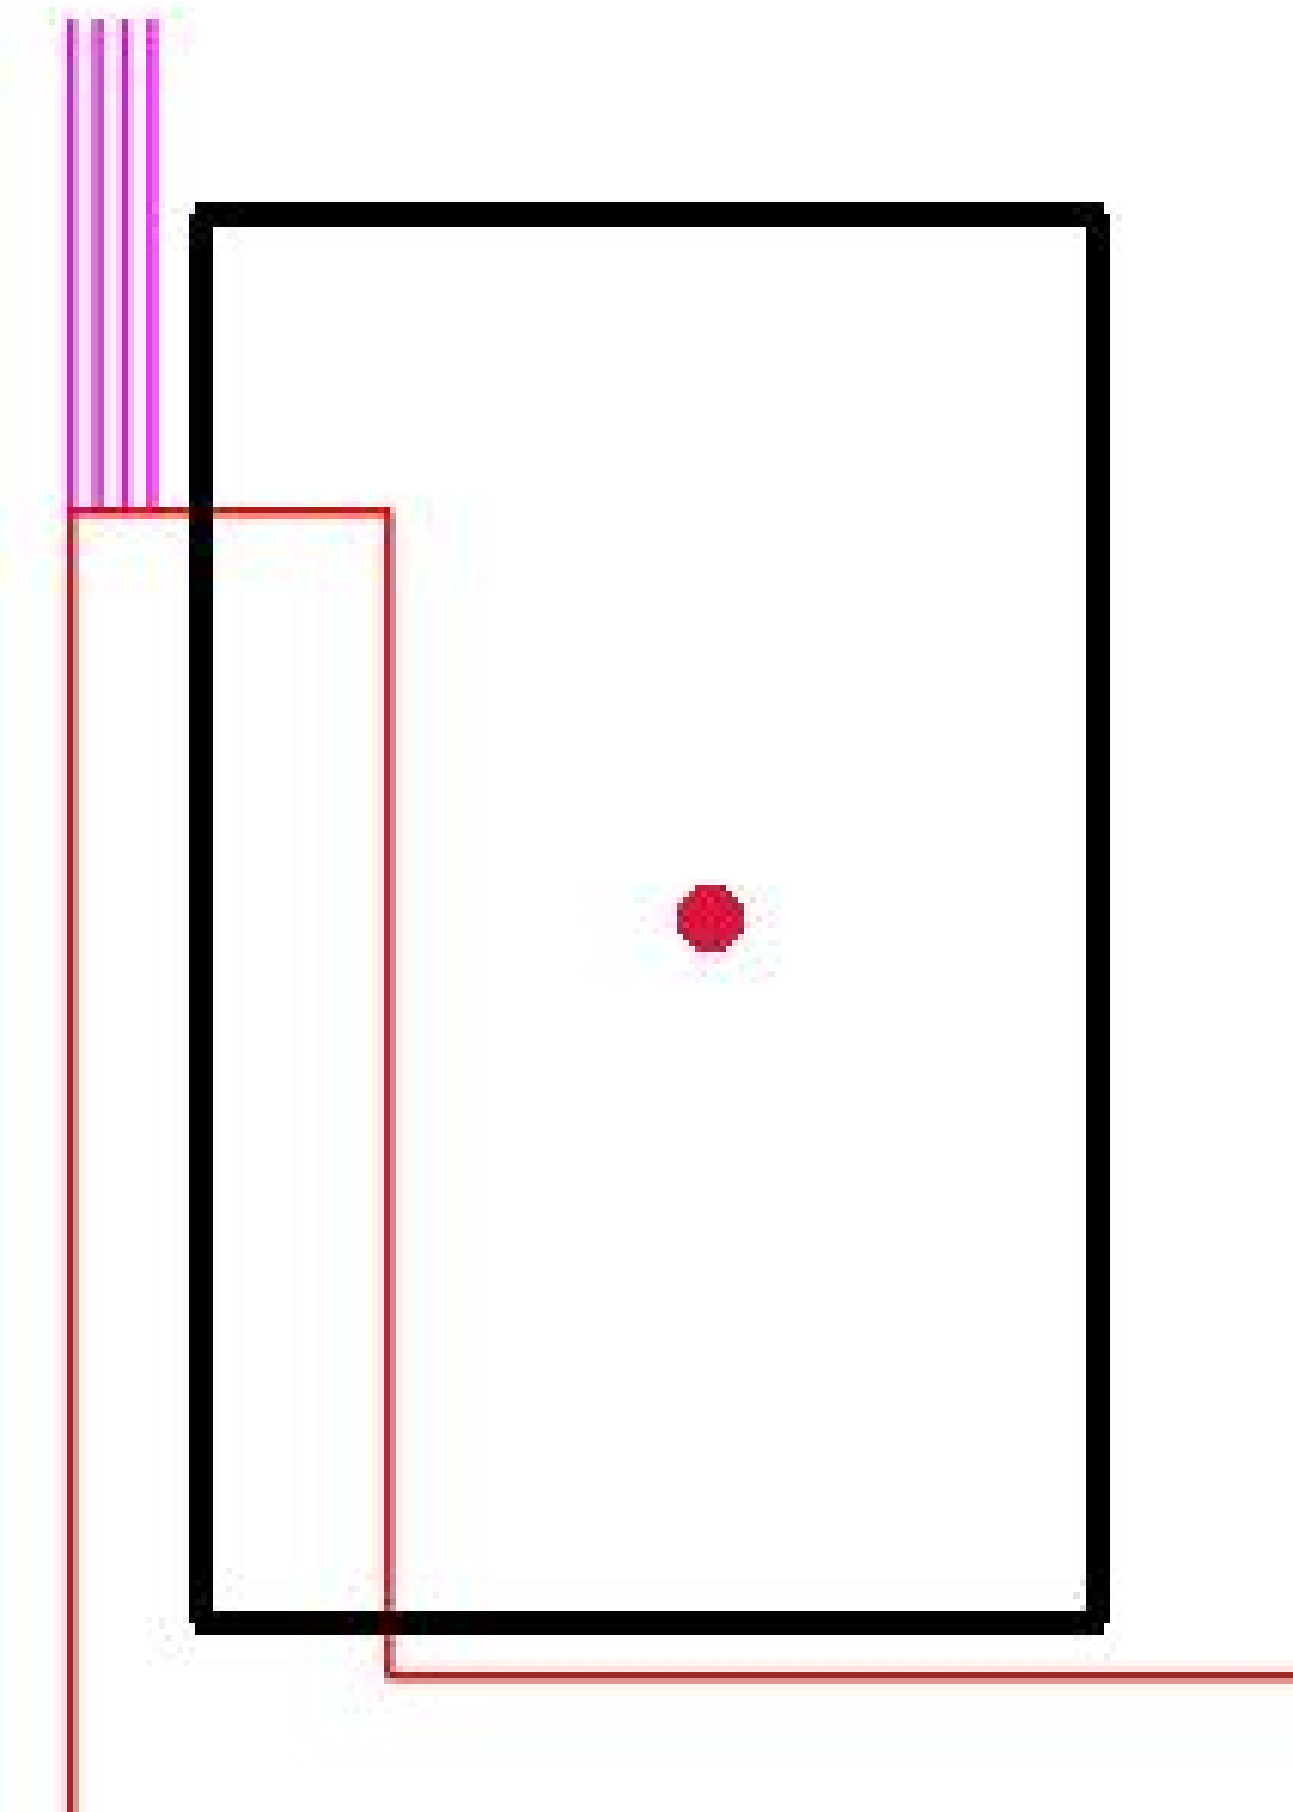

PASSAGE | vector_polygon_closed_gap | 5

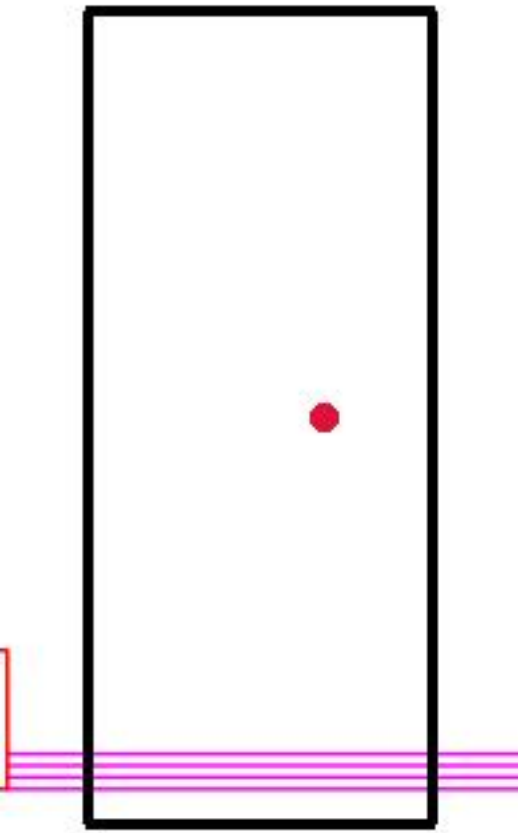

M.TOILET | vector_polygon_closed_gap | 11.98

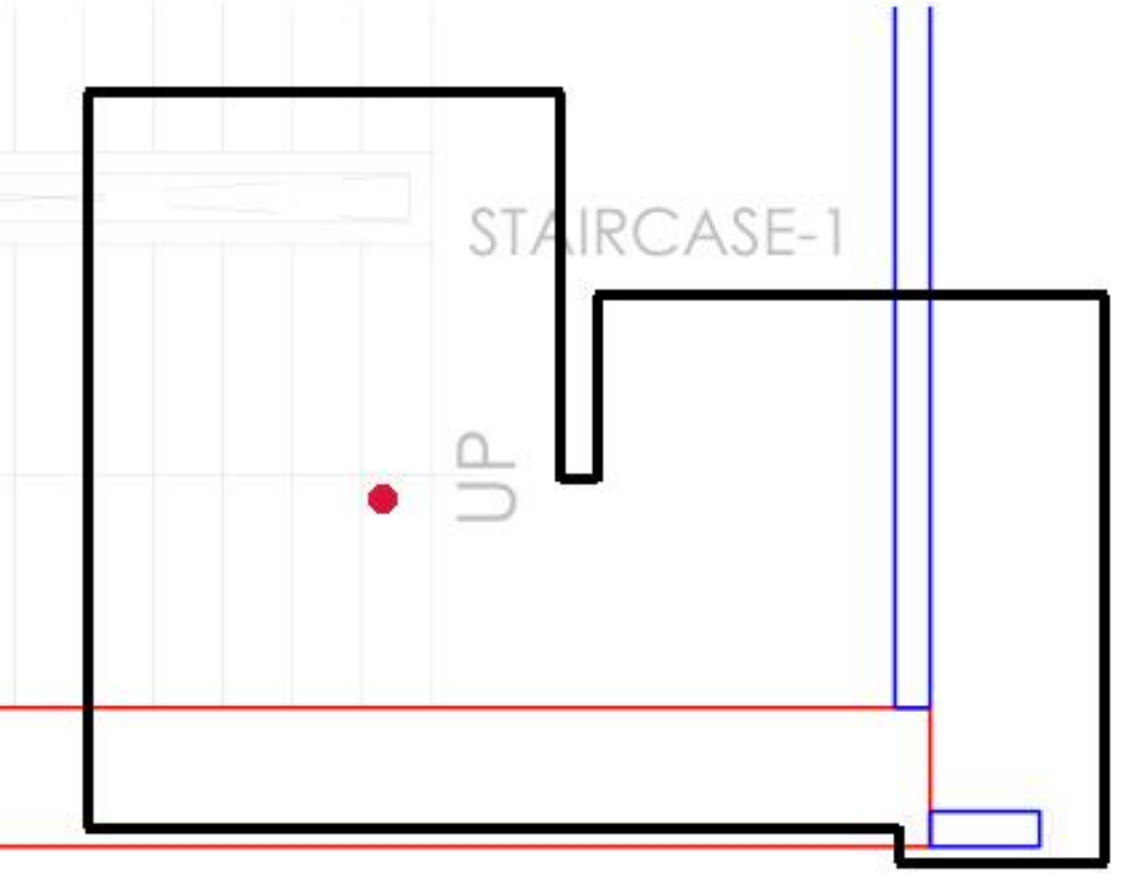

CHW | vector_polygon_exact

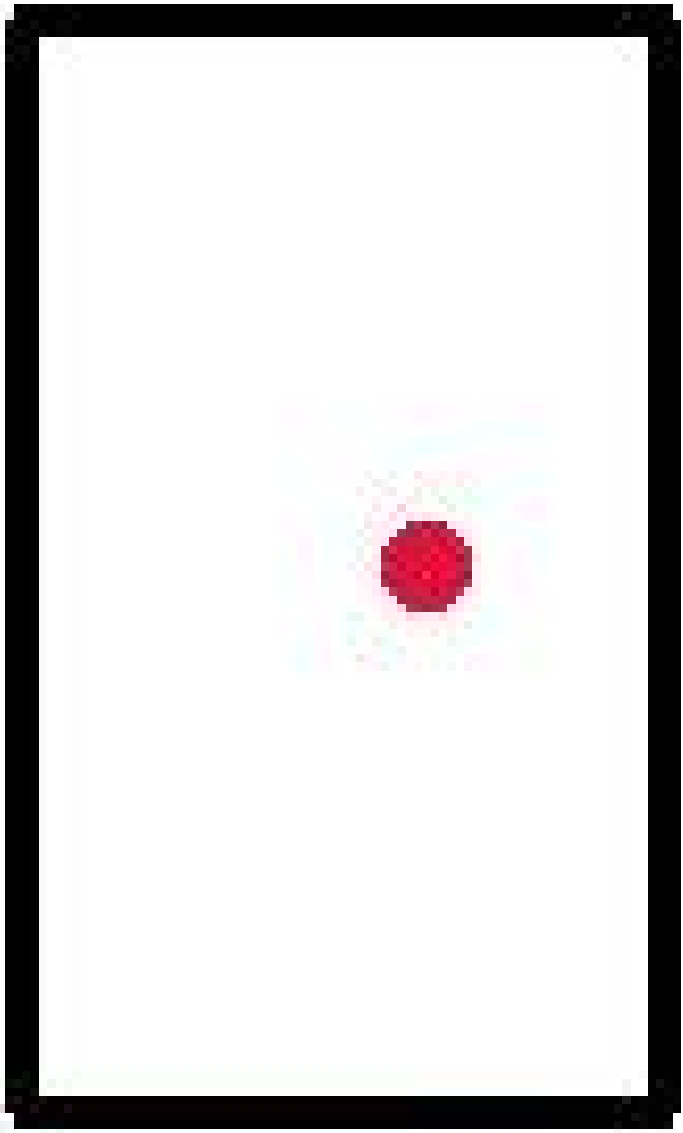

LIFT B4 | vector_polygon_exact | 6.04

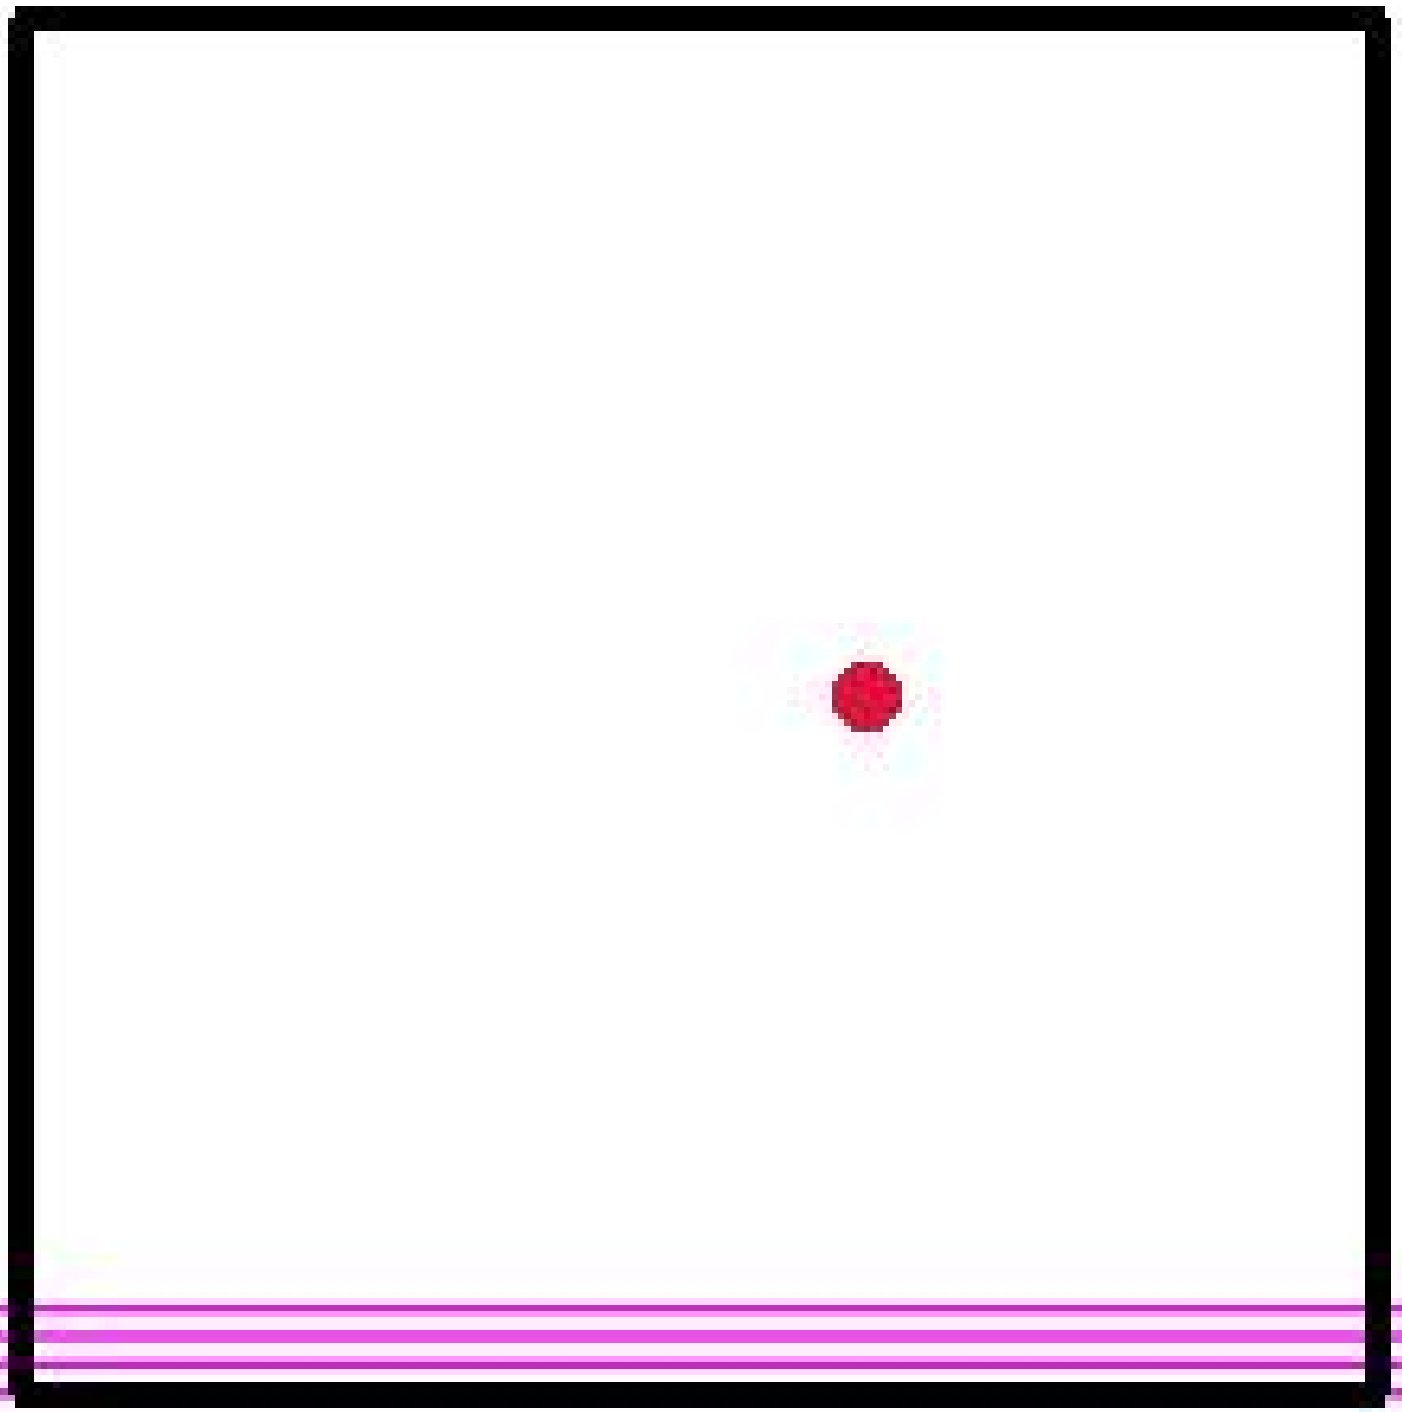

LIFT B2 | vector_polygon_exact | 6.04

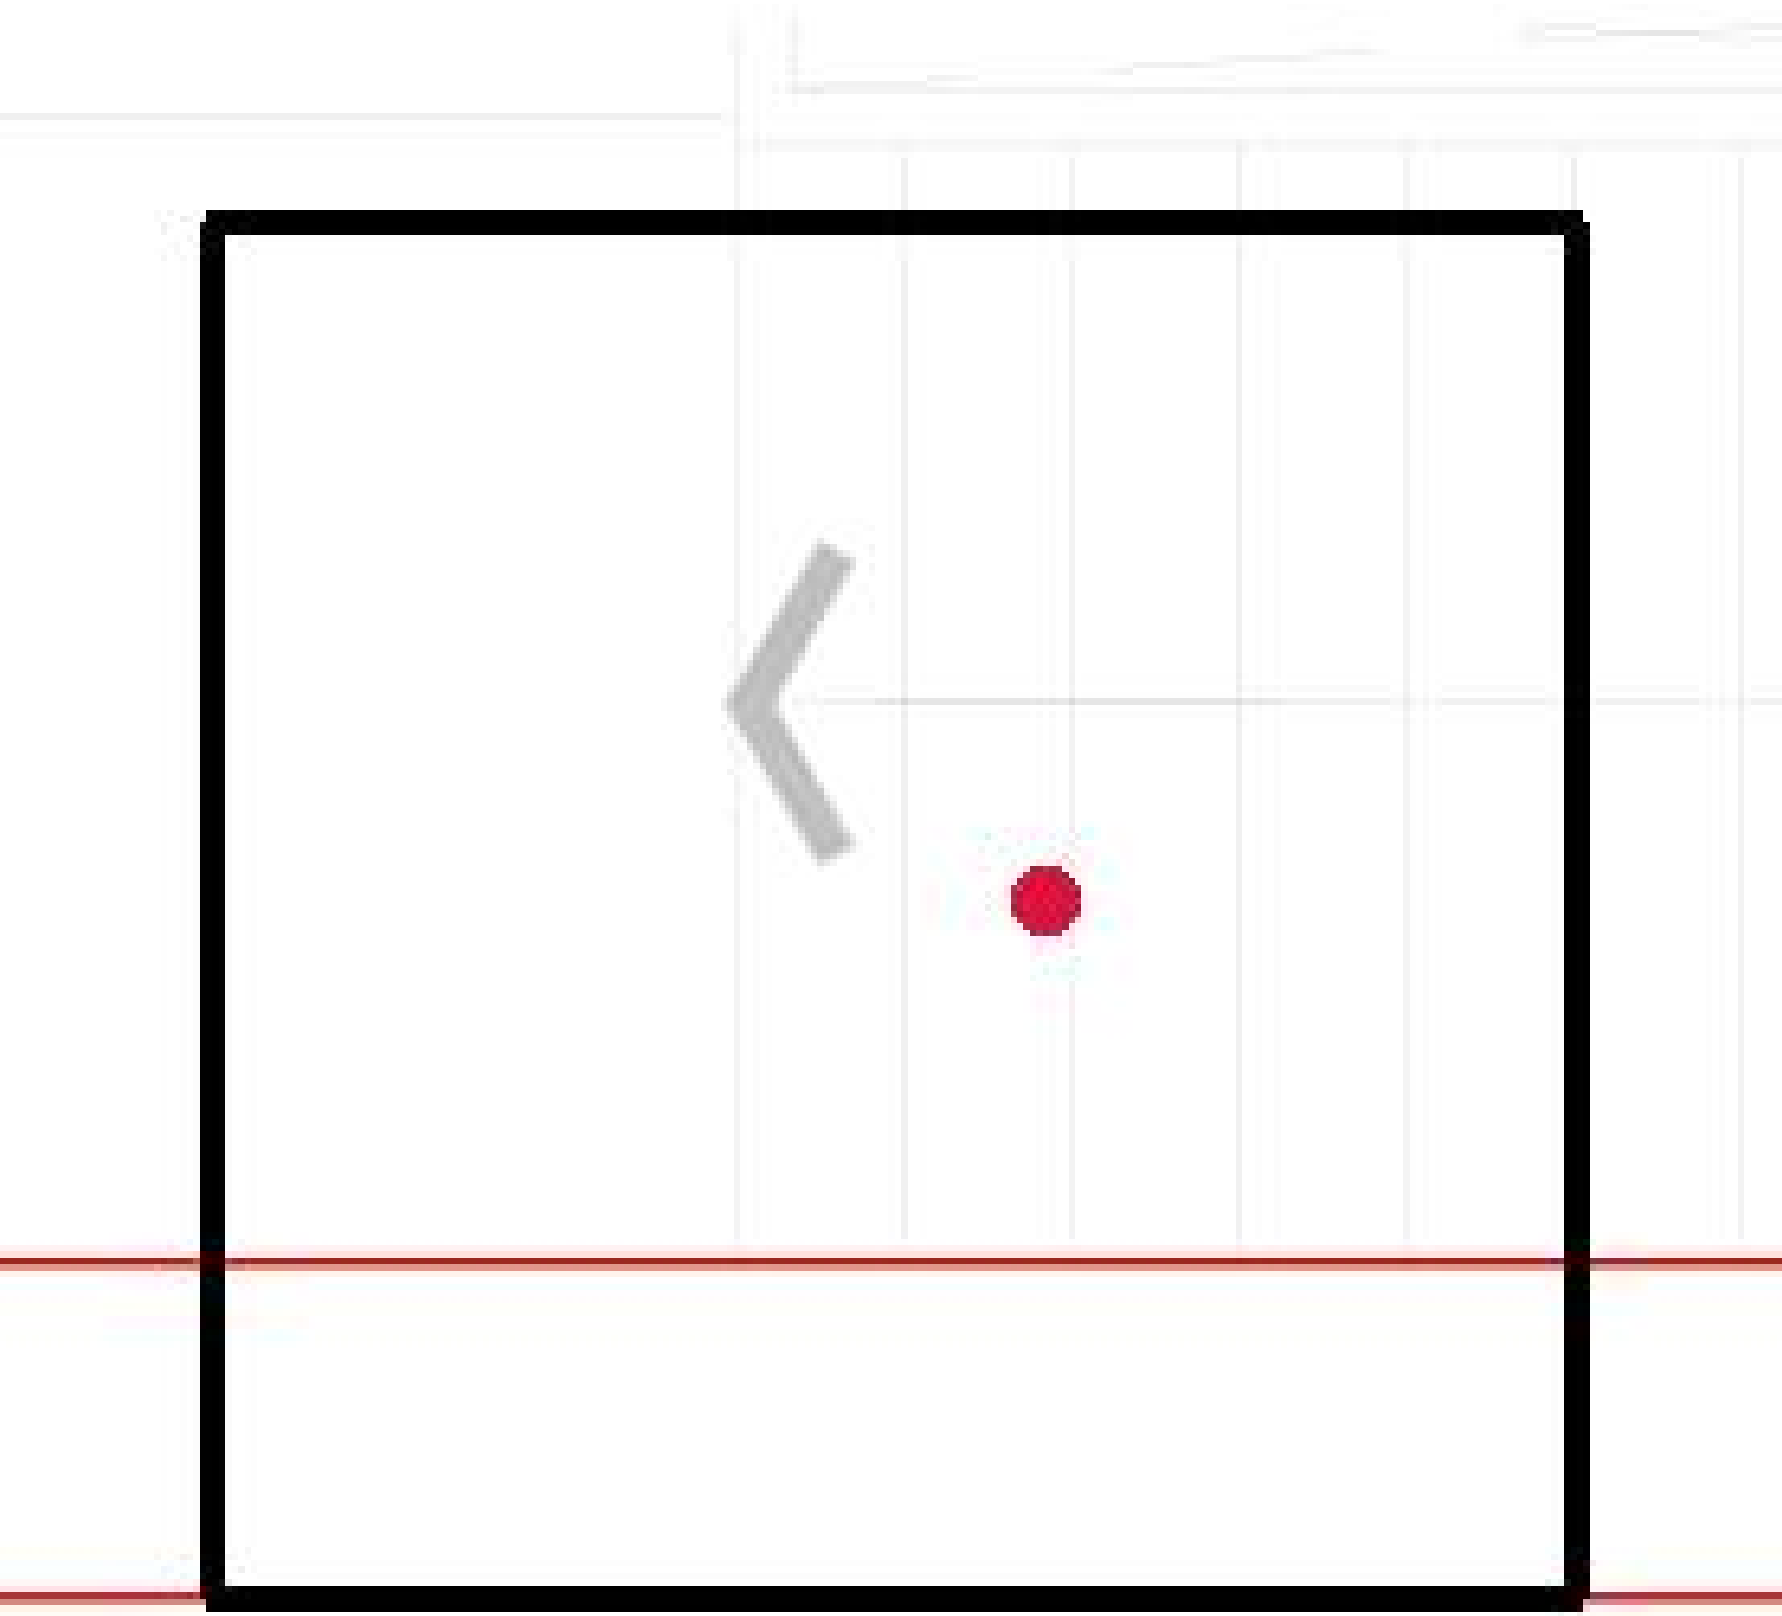

CO-RA | vector_polygon_exact | 0.92

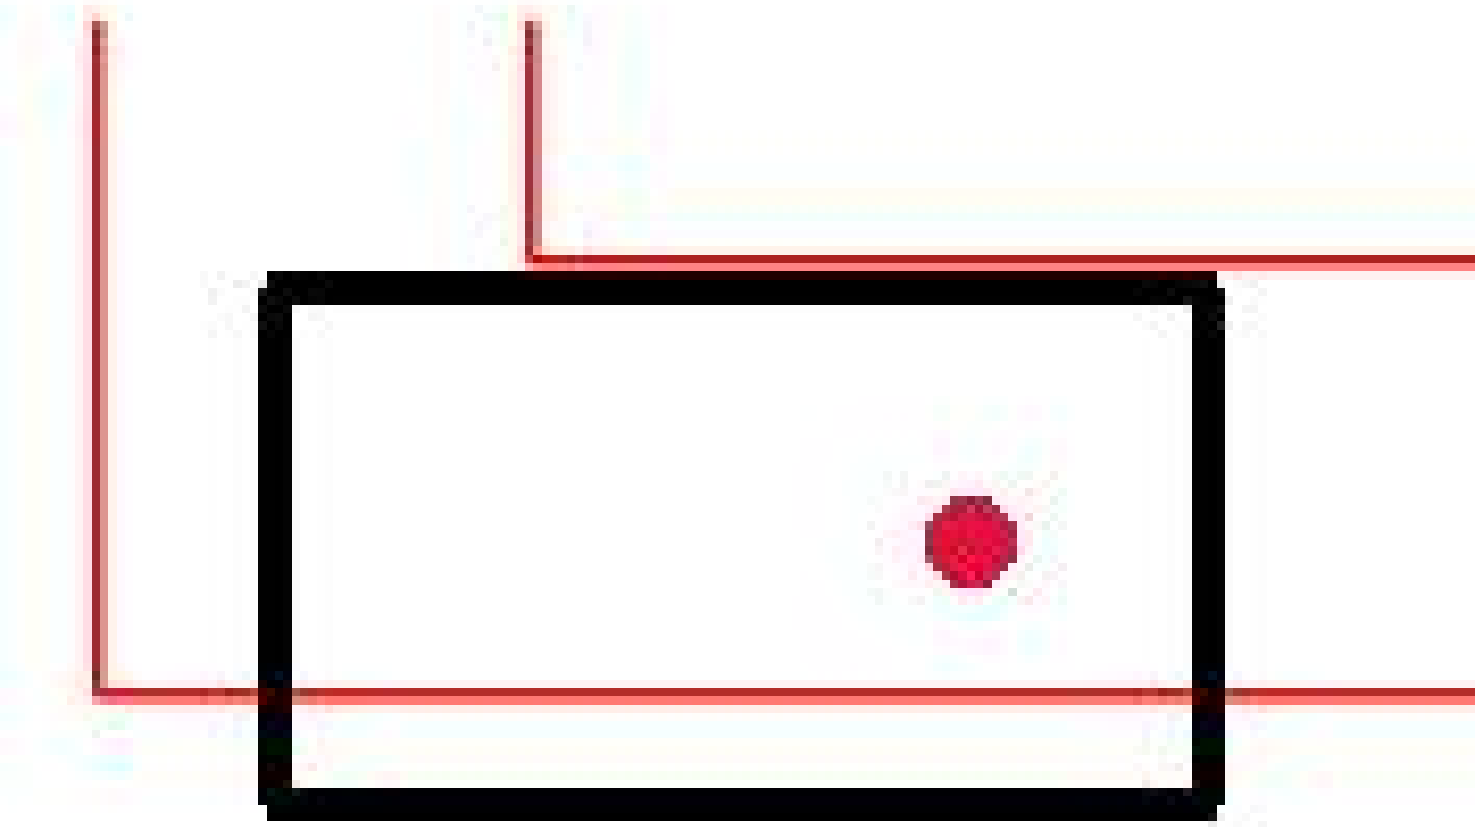

CO-FA | vector_polygon_exact | 0.92

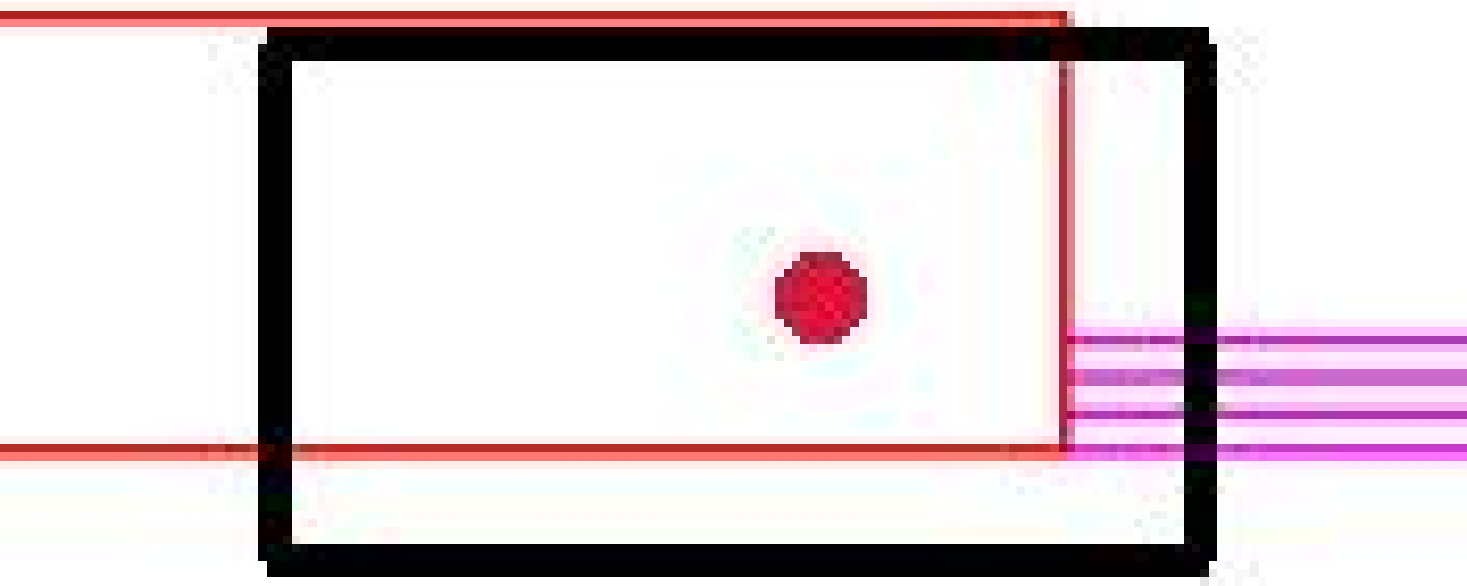

H.TOILET | vector_polygon_closed_gap | 4.15

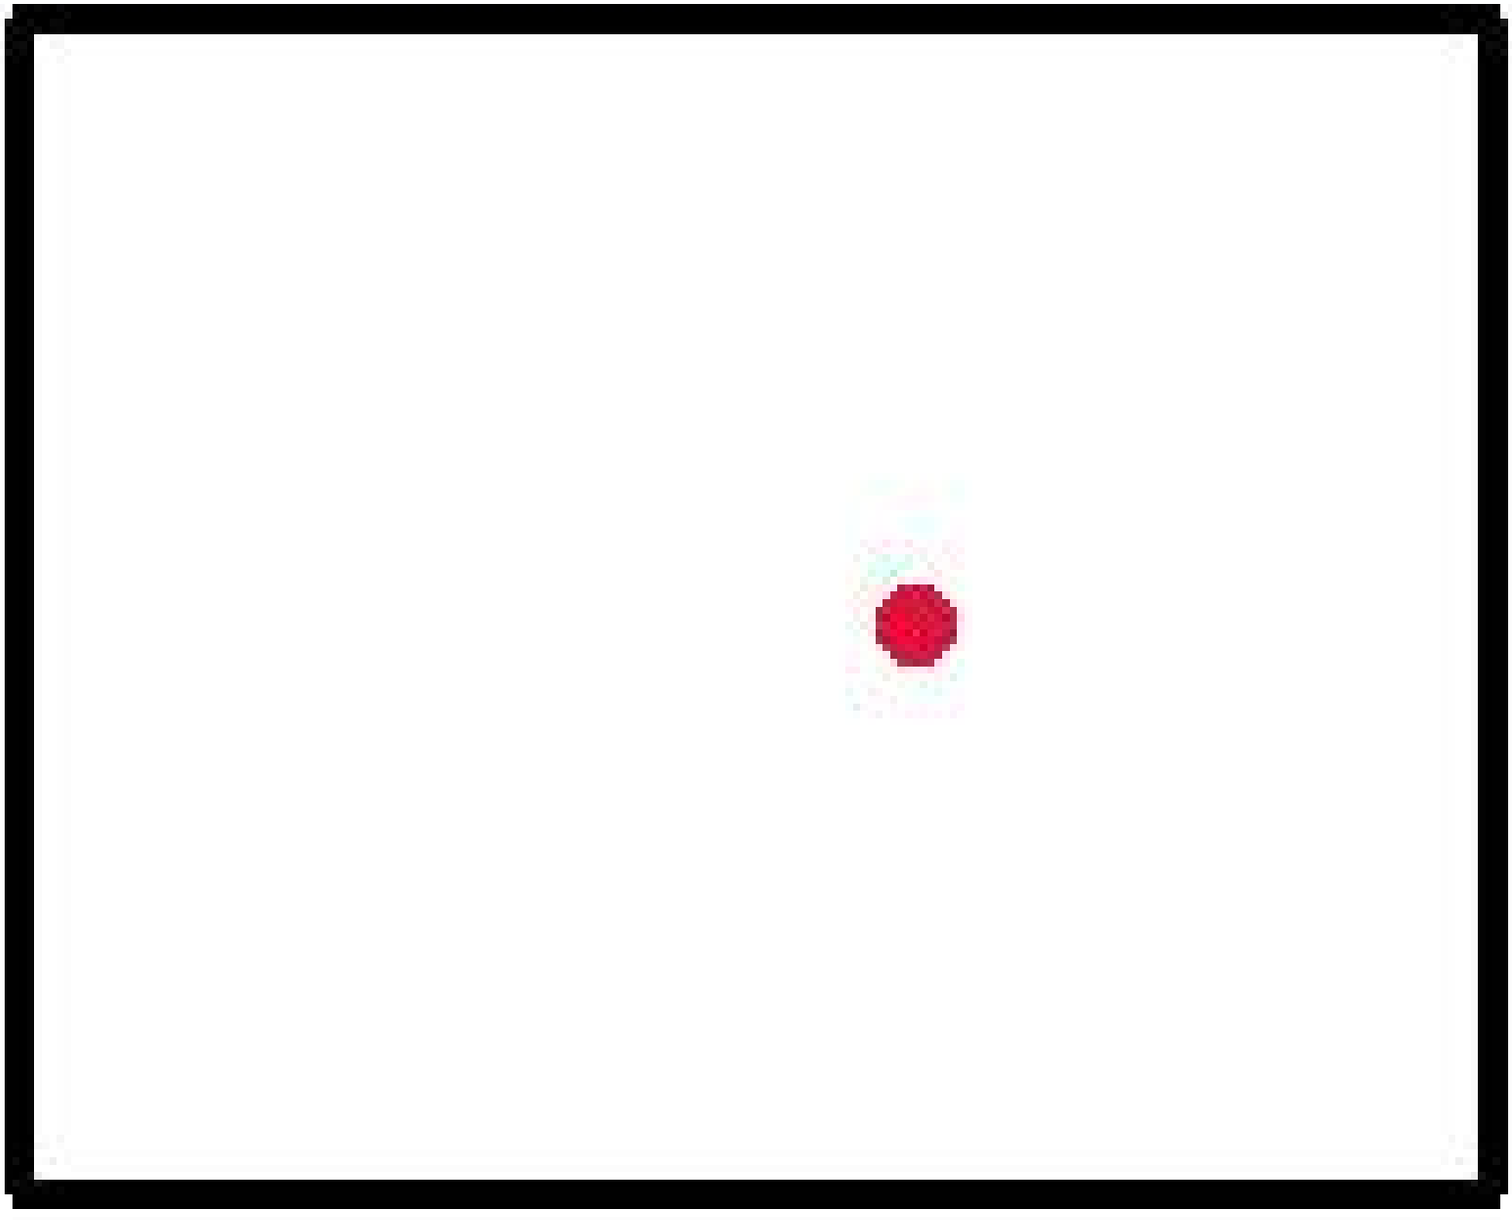

 

 

F.TOILET | vector_polygon_closed_gap | 9.08

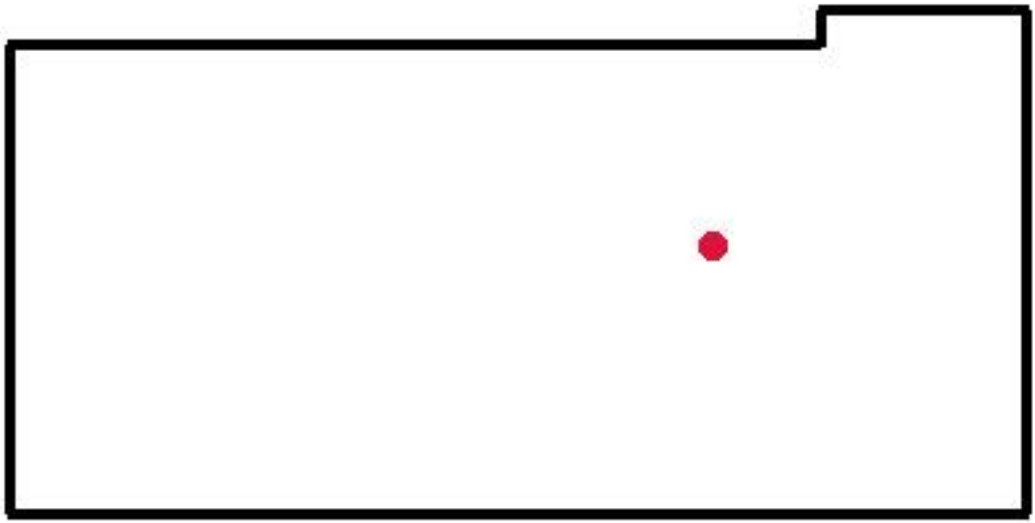

RWS | vector_polygon_exact | 1.4

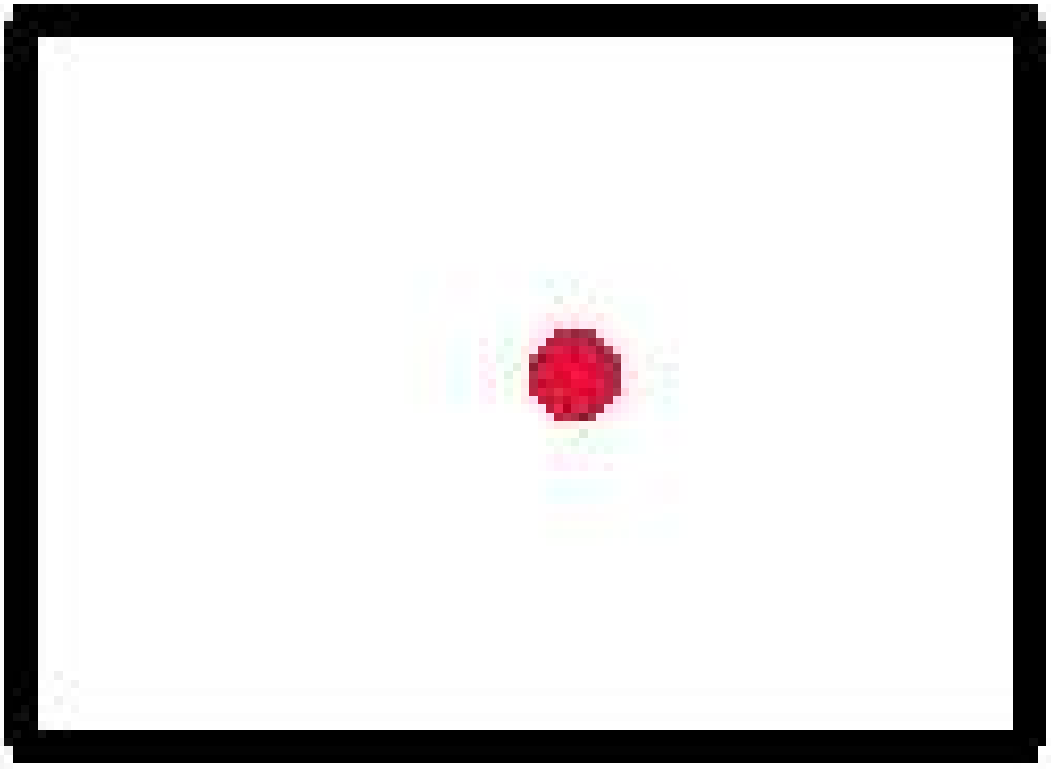

LOBBY. PRESSURIZATION | vector_polygon_exact | 2.5

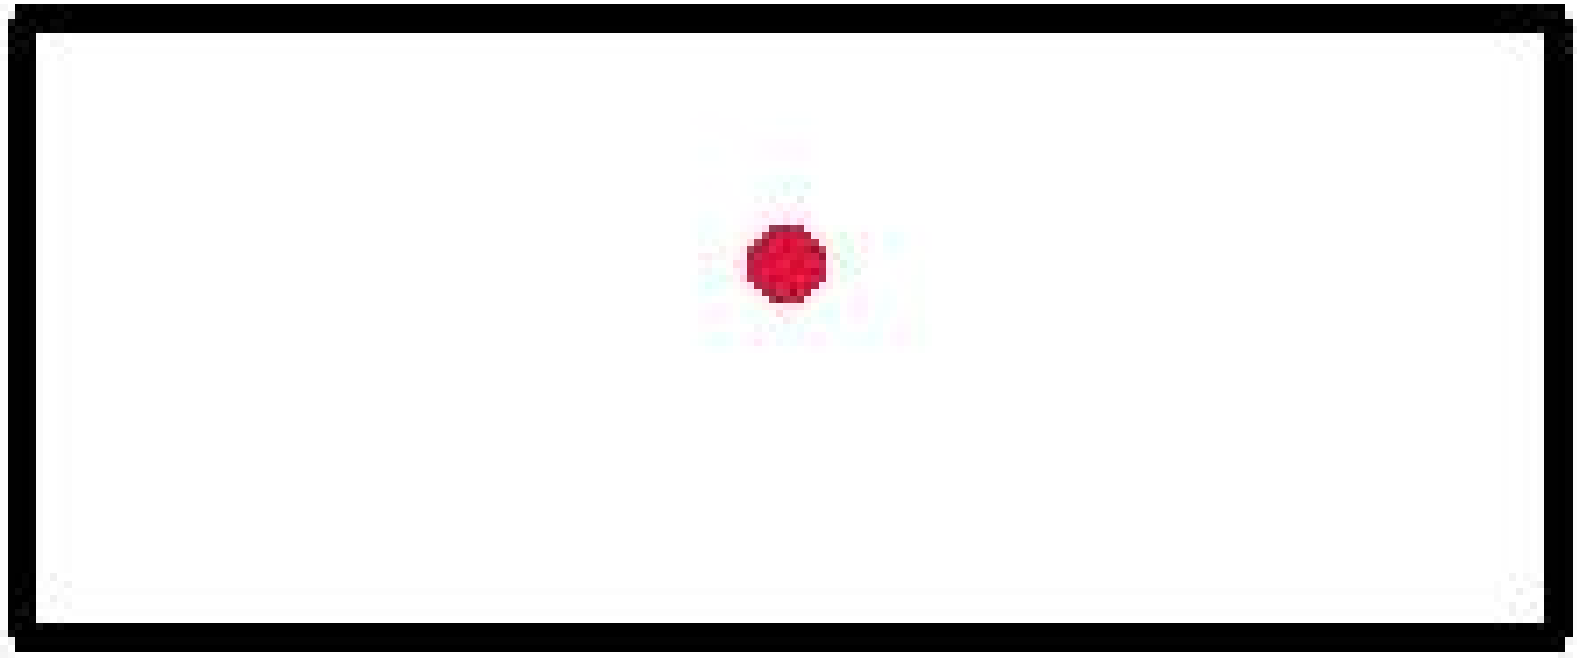
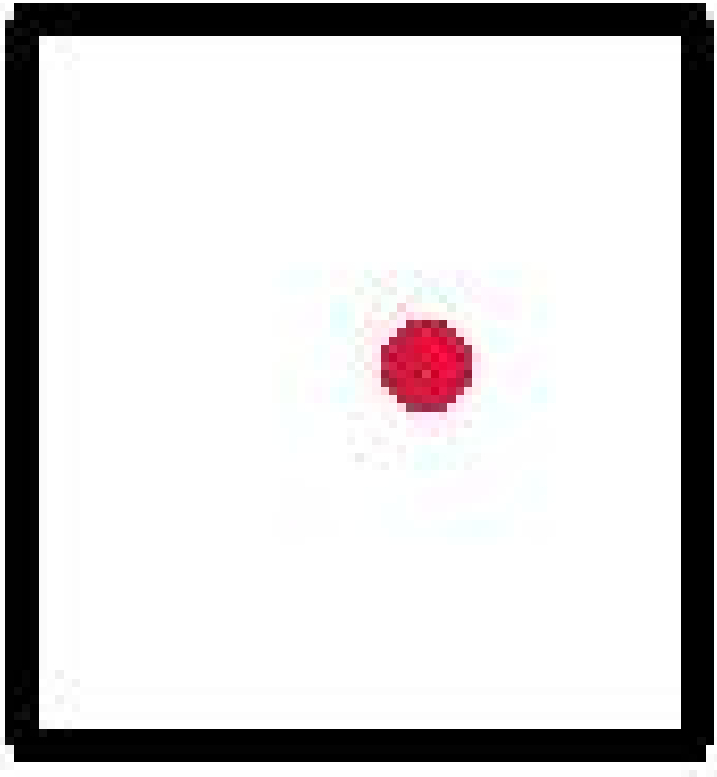
ELV | vector_polygon_exact | 0